TCC - ET

2-UNIT RESIDENCE

DRFT 2543

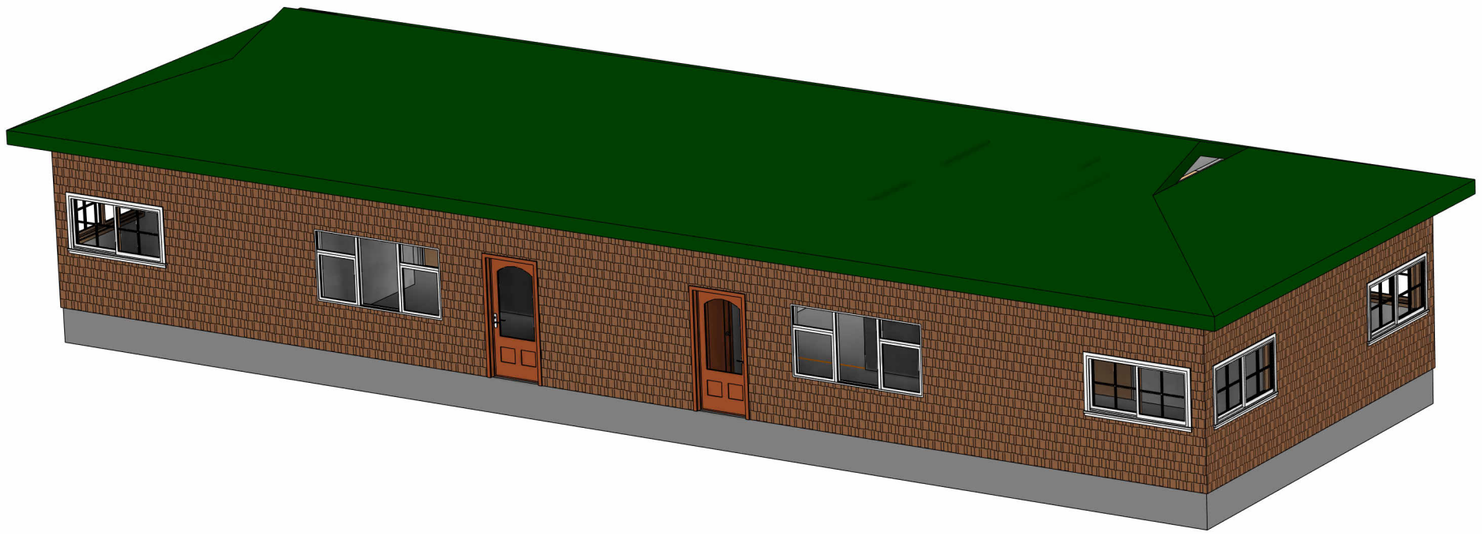

Sheet Index

Sheet Number	Sheet Name
C102	Unnamed
General	
G100	Cover
Civil	
C101	Site Plan
Structural	
S101	Structural Plans
S102	Structural Plans
Architectural	
A101	SITE PLAN AND FLOOR PLAN
A102	Architectural Floor Plans
A201	BUILDING ELEVATIONS
A202	Architectural Building Elevations
A203	Architectural Building Elevations
A204	Architectural Building Elevations
A301	BUILDING SECTIONS
A401	Architectural Enlarged Views
A501	DETAILS & SCHEDULES FINAL
A601	Architectural Schedules
Plumbing	
P101	Plumbing Plans
P102	Plumbing Plans
Mechanical	
M101	Mechanical Plans
M102	Mechanical Plans
Electrical	
E101	Power Plans
E102	Power Plans
E103	Lighting Plans
E104	Lighting Plans

Consultant
Address
Address
Address
Phone

Consultant
Address
Address
Address
Phone

Consultant
Address
Address
Address
Phone

Consultant
Address
Address
Address
Phone

Consultant
Address
Address
Address
Phone

Project Number

Date

FINAL

Issue Date

AUTODESK

5/6/2026 2:28:06 PM

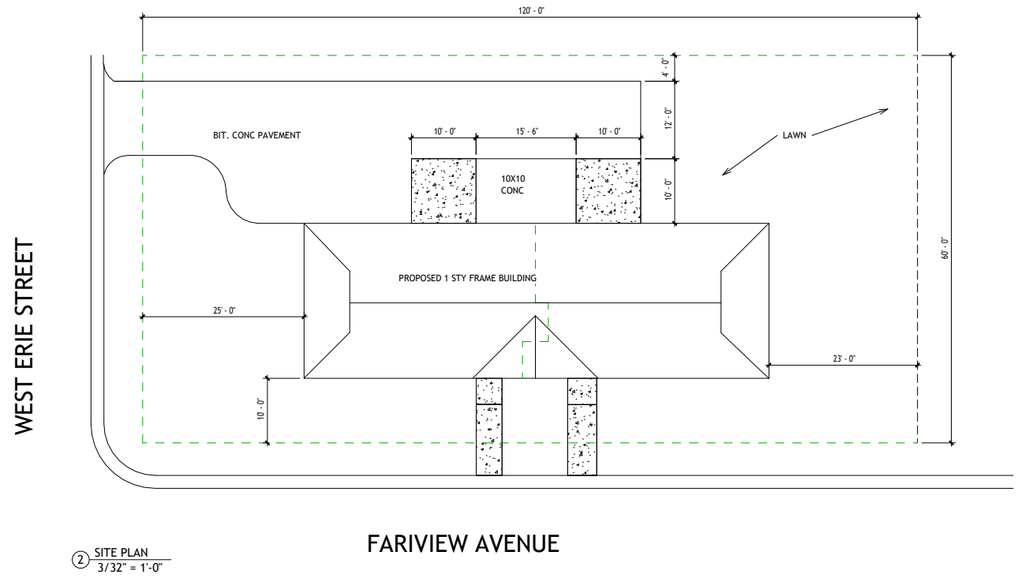

2 SITE PLAN
3/32" = 1'-0"

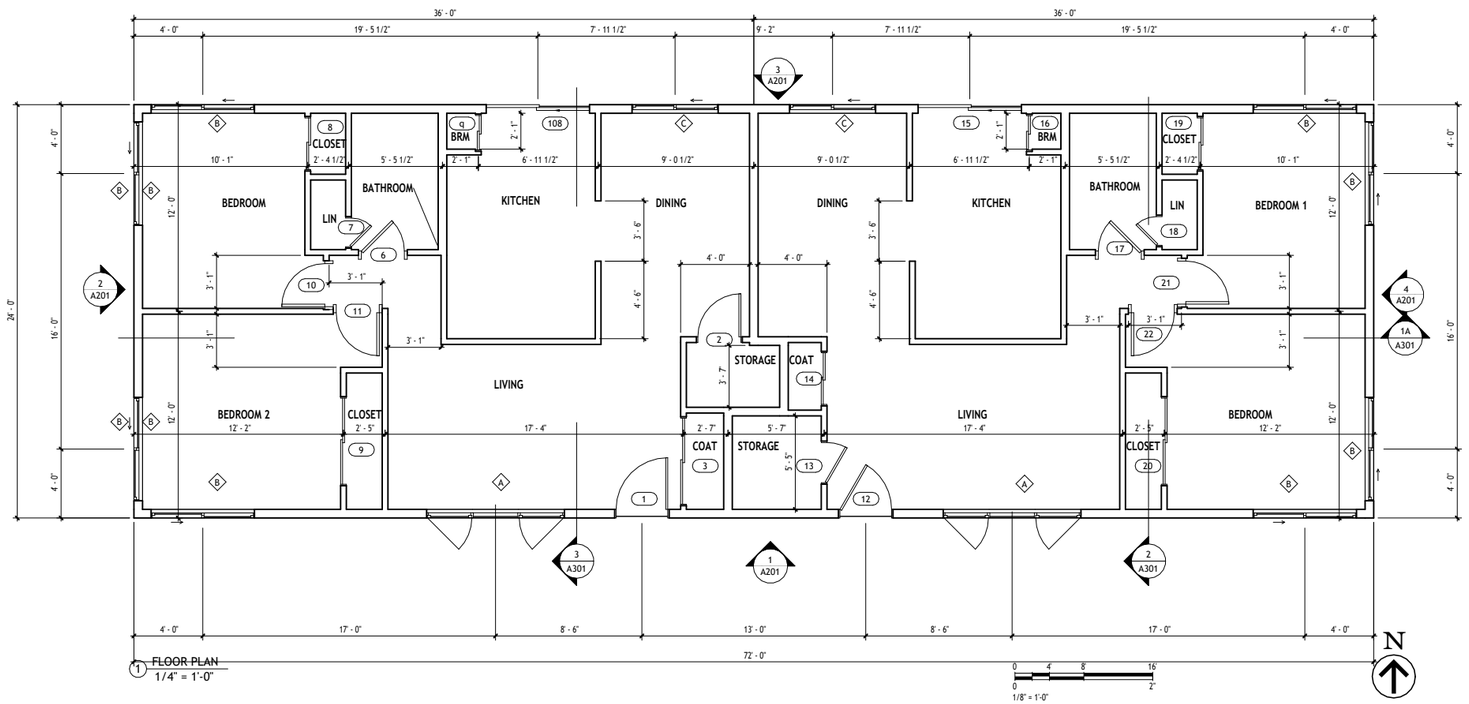

1 FLOOR PLAN
1/4" = 1'-0"

AUTODESK

www.autodesk.com/revit

Consultant
Address
Address
Phone
Fax
e-mail

Consultant
Address
Address
Phone
Fax
e-mail

Consultant
Address
Address
Phone
Fax
e-mail

Consultant
Address
Address
Phone
Fax
e-mail

Consultant
Address
Address
Phone
Fax
e-mail

No.	Description	Date

TCC - ET
2-UNIT RESIDENCE

SITE PLAN AND FLOOR PLAN

Project number	FINAL
Date	Issue Date
Drawn by	ADEL KNODE
Checked by	BRADFORD

A101

Scale	As indicated

5/6/2026 2:28:08 PM

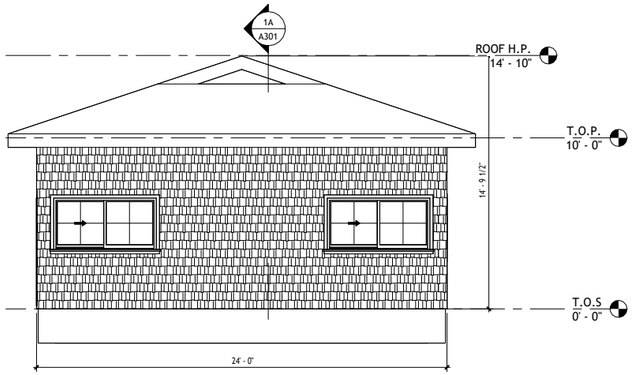

2 WEST ELEVATION
1/4" = 1'-0"

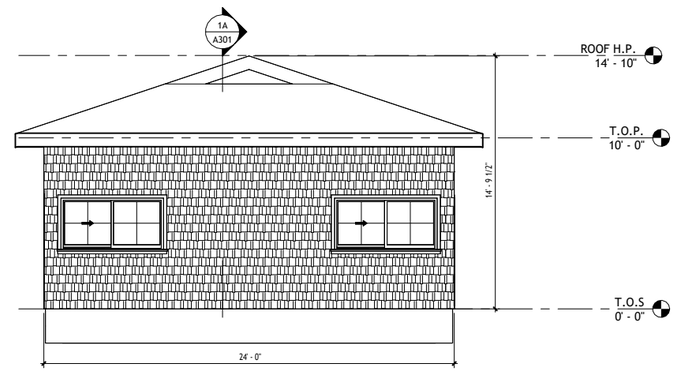

4 EAST ELEVATION
1/4" = 1'-0"

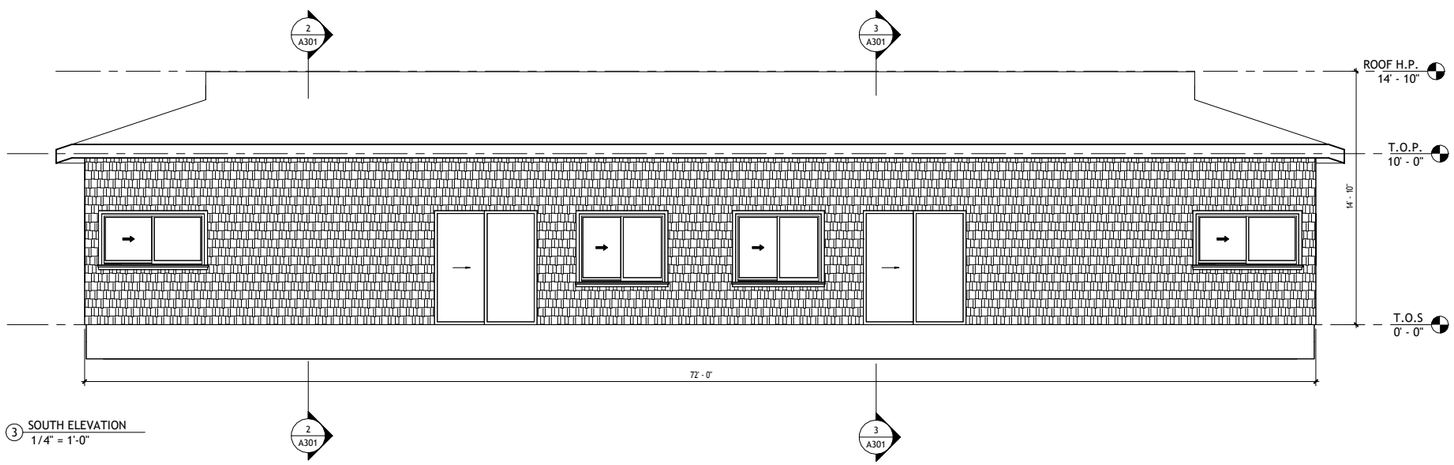

3 SOUTH ELEVATION
1/4" = 1'-0"

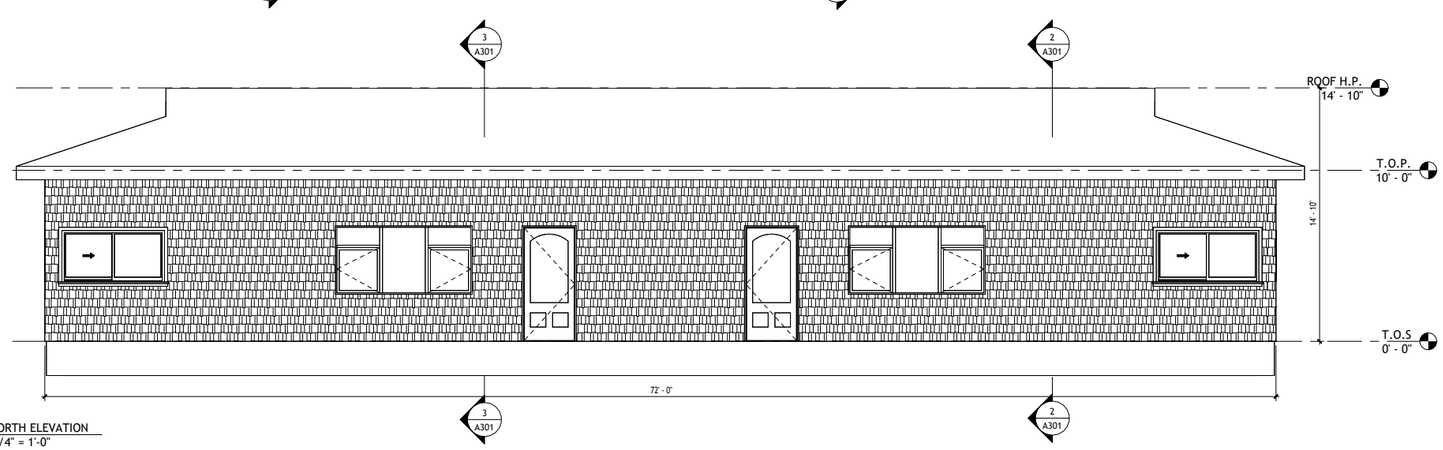

1 NORTH ELEVATION
1/4" = 1'-0"

AUTODESK

www.autodesk.com/revit

Consultant
Address
Address
Phone
Fax
e-mail

Consultant
Address
Address
Phone
Fax
e-mail

Consultant
Address
Address
Phone
Fax
e-mail

Consultant
Address
Address
Phone
Fax
e-mail

Consultant
Address
Address
Phone
Fax
e-mail

NOTE: ACTUAL SHEET SET SIZE IS D - 22" X 34"

No.	Description	Date

TCC - ET
2-UNIT RESIDENCE
BUILDING ELEVATIONS

Project number	FINAL
Date	Issue Date
Drawn by	ADEL KNODE
Checked by	BRADFORD

A201

Scale	1/4" = 1'-0"

5/6/2026 2:28:08 PM

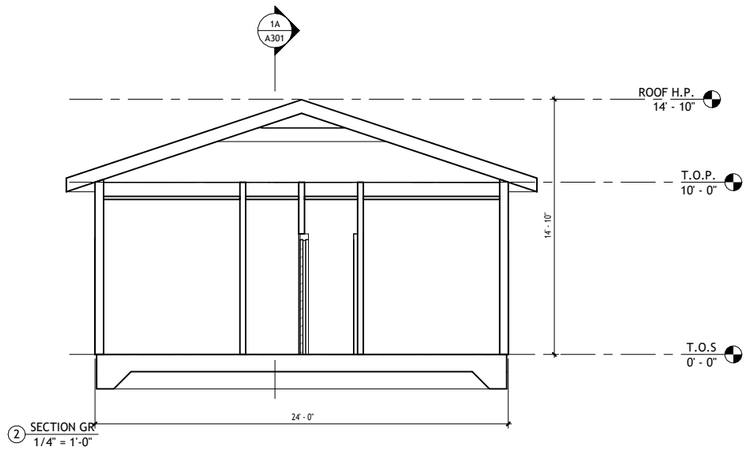

2 SECTION GR
1/4" = 1'-0"

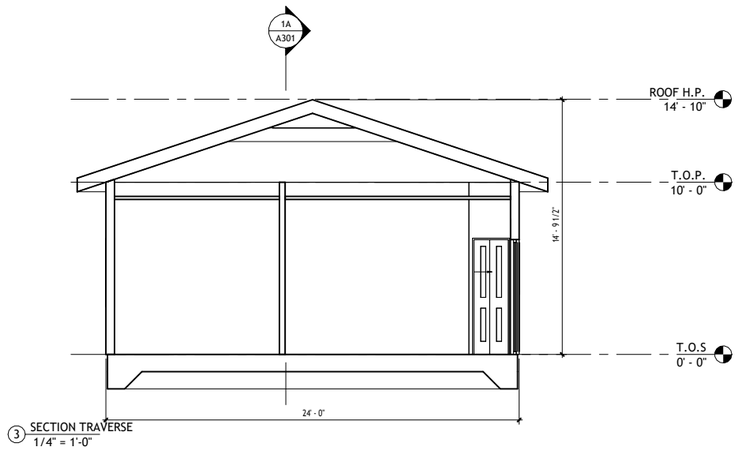

3 SECTION TRAVERSE
1/4" = 1'-0"

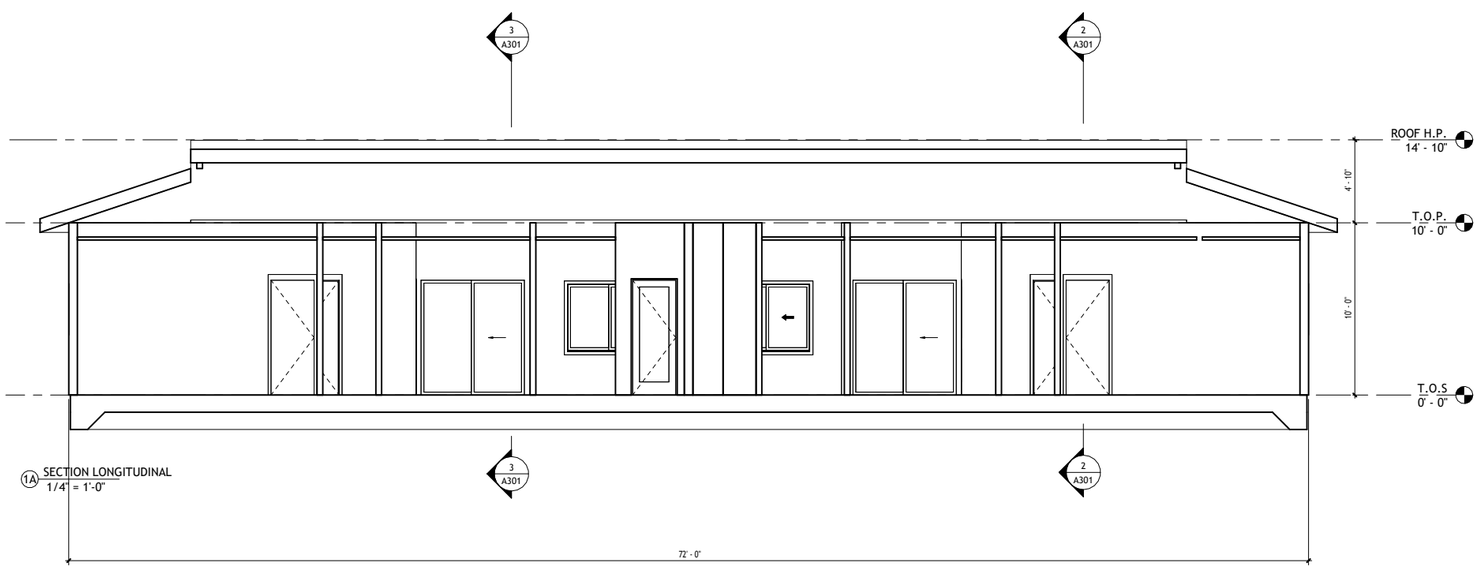

1A SECTION LONGITUDINAL
1/4" = 1'-0"

AUTODESK

www.autodesk.com/revit

Consultant
Address
Address
Phone
Fax
e-mail

Consultant
Address
Address
Phone
Fax
e-mail

Consultant
Address
Address
Phone
Fax
e-mail

Consultant
Address
Address
Phone
Fax
e-mail

Consultant
Address
Address
Phone
Fax
e-mail

NOTE: ACTUAL SHEET SET SIZE IS D - 22" X 34"

No.	Description	Date

TCC - ET
2-UNIT RESIDENCE
BUILDING SECTIONS

Project number	FINAL
Date	Issue Date
Drawn by	ADEL KNODE
Checked by	BRADFORD

A301

Scale	1/4" = 1'-0"

5/6/2026 2:28:08 PM

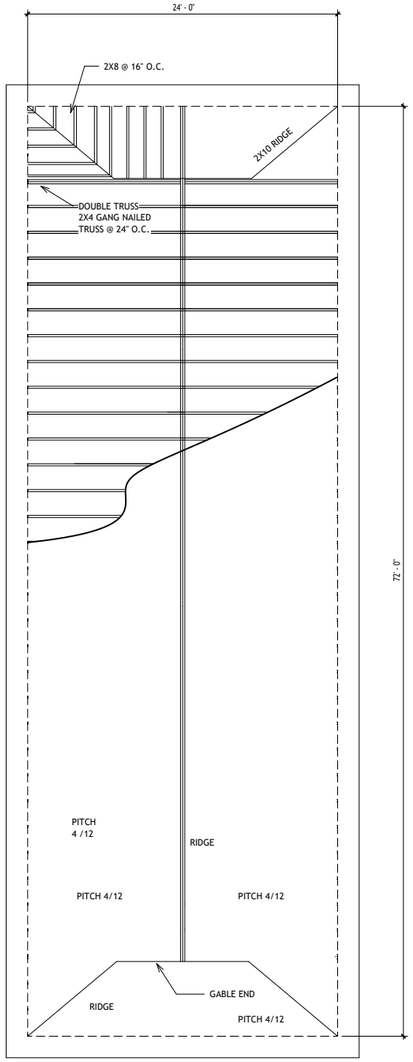

4 ROOF FRAMING PLAN
3/16" = 1'-0"

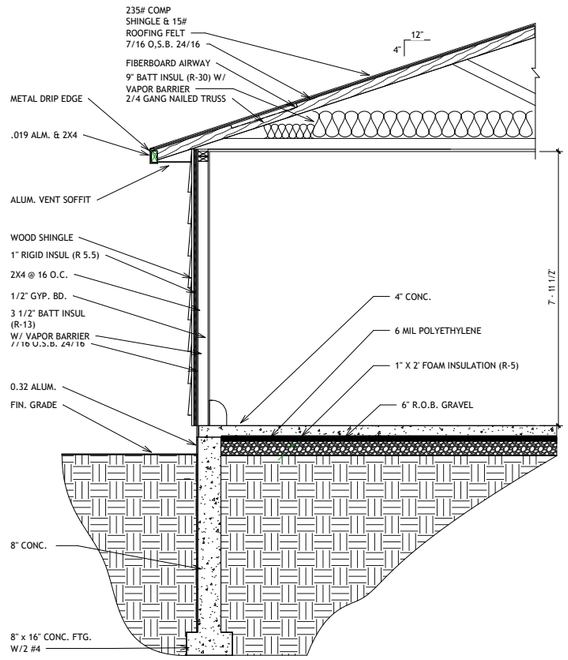

5 WALL SECTION (TYPICAL)
1/2" = 1'-0"

WEST SIDE DOOR SCHEDULE: (ALL UNITS PREHUNG / PREFIT W/HARDWARE)											
				DOOR		FRAME					
TAG	LOCATION	SIZE	THK.	MAT'L	TYPE	MAT'L		GLASS	DOOR	W/STRIP /T'HOLD	COMMENTS
1	ENTRY	36 X 80	1- 3/8	HM	A	WD	A	5/8 INSUL	ENTRY	INTEGRAL	
2	CLOSET	30 X 80	1- 3/8	HCW	E	WD	B				BIFOLD
3	BEDROOM/BATH	60 X 80	1- 3/8	HCW	C	WD	B	–	PRIVACY		
4	CLOSET	72 X 80	2	HCW	C	WD	B	–	PASSAGE		
5	H.W. HTR.	24 X 80	1- 3/8	HCW	C	WD	B	–	PASSAGE		
6	CLOSET	30 X 80	1- 3/8	HCW	D	WD	B	–	–		SLIDING
7	CLOSET	20 X 80	1- 3/8	HCW	D	WD	B	–	–		SLIDING
8	CLOSET	36 X 80	1- 3/8	HCW	E	WD	B	–	–		BIFOLD

8 DOOR SCHEDULE WEST
3/4" = 1'-0"

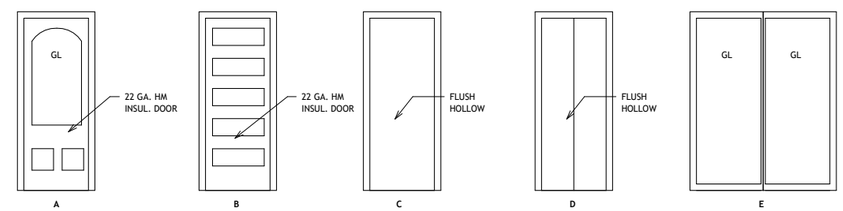

9 DOOR TYPES
3/8" = 1'-0"

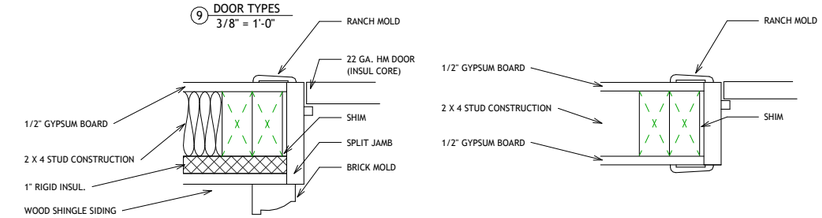

6 FRAME TYPES
3" = 1'-0"

WINDOW SCHEDULE				
TAG	SIZE	TYPE	GLASS	COMMENTS
A	8' X 4'	CASEMENT	1" INSUL	FIXED CTR.
B	6' X 3'	SLIDING	1" INSUL	
C	5' X 4'	SLIDING	1" INSUL	
D	6' X 6-8'	SLIDING DOOR	1" INSUL	

1 WINDOW SCHEDULE
3/4" = 1'-0"

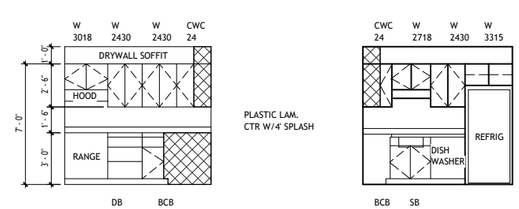

2 KITCHEN ELEVATIONS
1/4" = 1'-0"

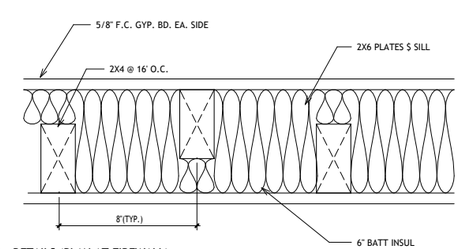

3 DETAILS (PLAN AT FIREWALL)
3" = 1'-0"

AUTODESK

www.autodesk.com/revit

Consultant
Address
Address
Phone
Fax
e-mail

Consultant
Address
Address
Phone
Fax
e-mail

Consultant
Address
Address
Phone
Fax
e-mail

Consultant
Address
Address
Phone
Fax
e-mail

Consultant
Address
Address
Phone
Fax
e-mail

NOTE: ACTUAL SHEET SET SIZE IS D - 22" X 34"

No.	Description	Date

TCC - ET
2-UNIT RESIDENCE

DETAILS & SCHEDULES
FINAL

Project number	FINAL
Date	Issue Date
Drawn by	ADEL KNODE
Checked by	BRADFORD

A501

Scale	As indicated

5/6/2026 2:28:09 PM