




Consultant
Address
Address
Address
Phone

[illegible]

Harbor View Offices
Level 1 Floor Plan


A101

Scale	1/8" = 1'-0"
-------	--------------

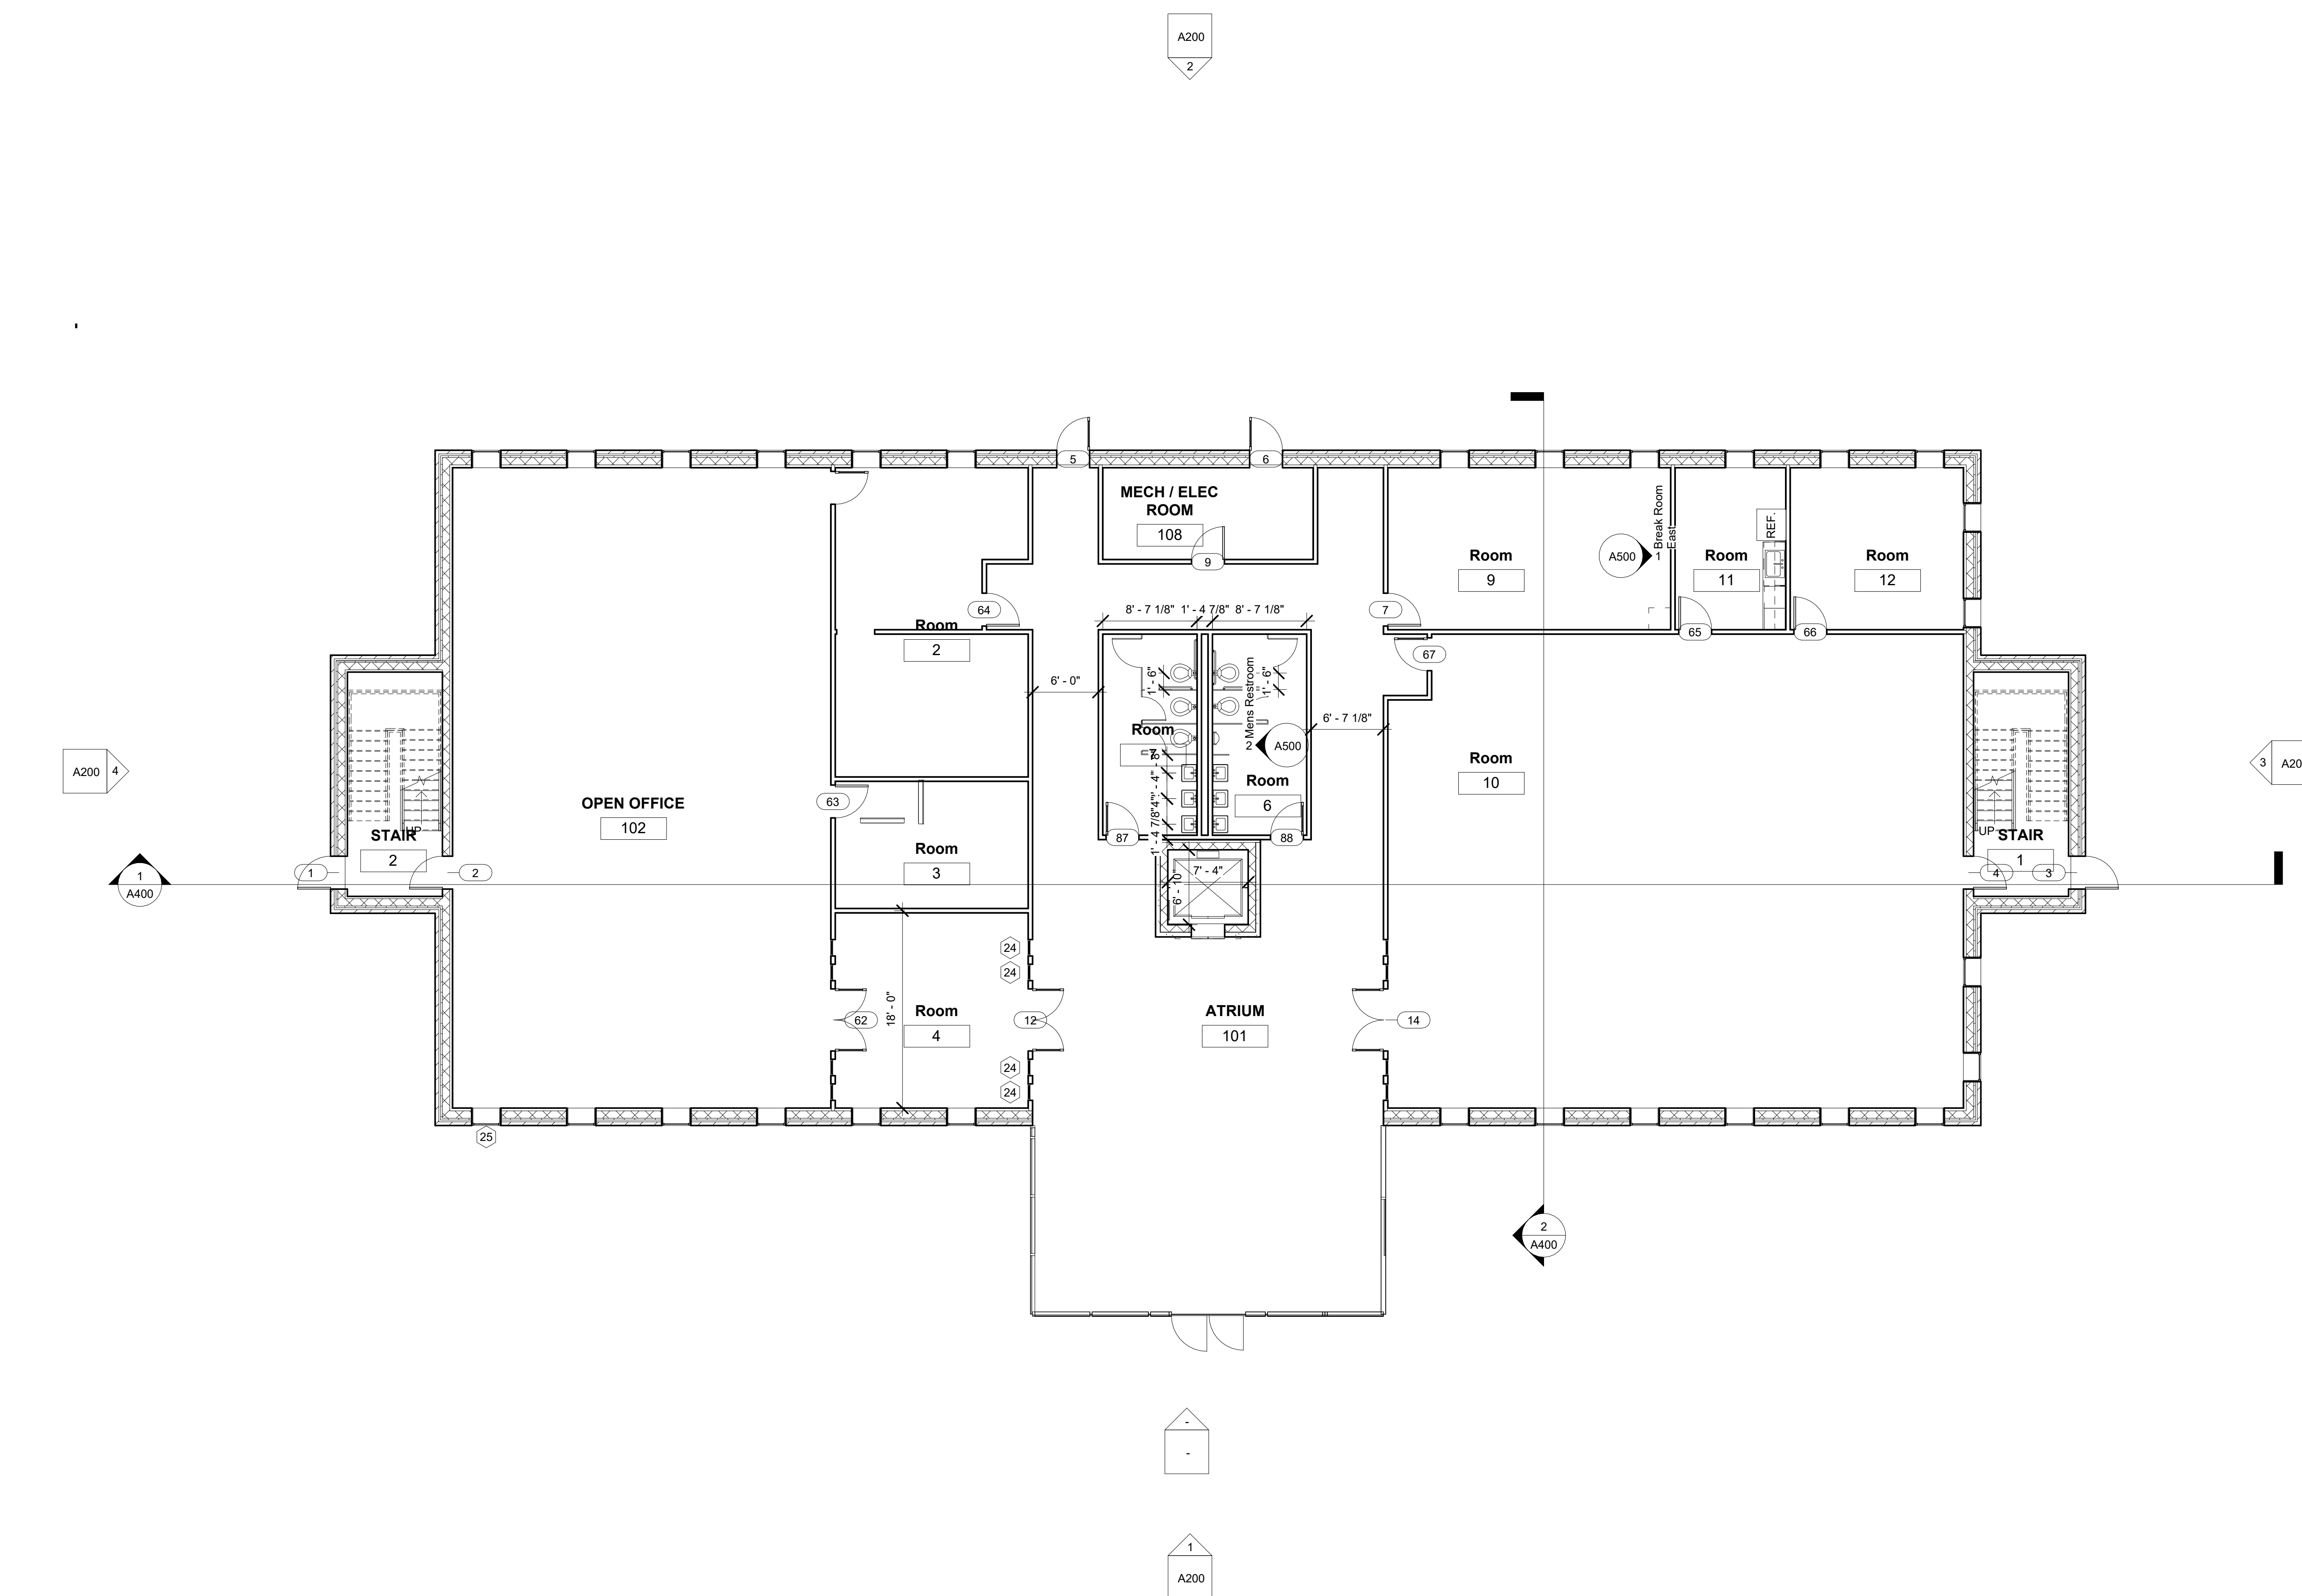

① Level 1
1/8" = 1'-0"

6/6/2026 1:55:49 PM

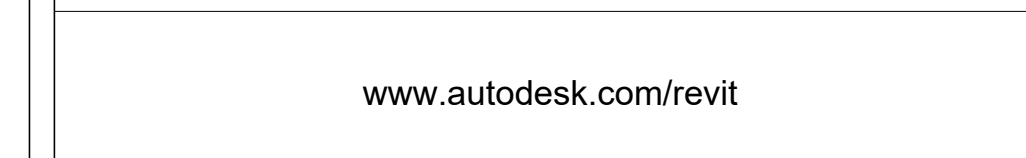

Consultant
Address
Address
Address
Phone

[illegible]


Harbor View Offices
Level 2 Floor Plan


Project Number	2026-001
Date	June 3, 2026
Drawn By	Author
Checked By	Checker

A102

Scale	1/8" = 1'-0"
-------	--------------

6/6/2026 1:55:49 PM

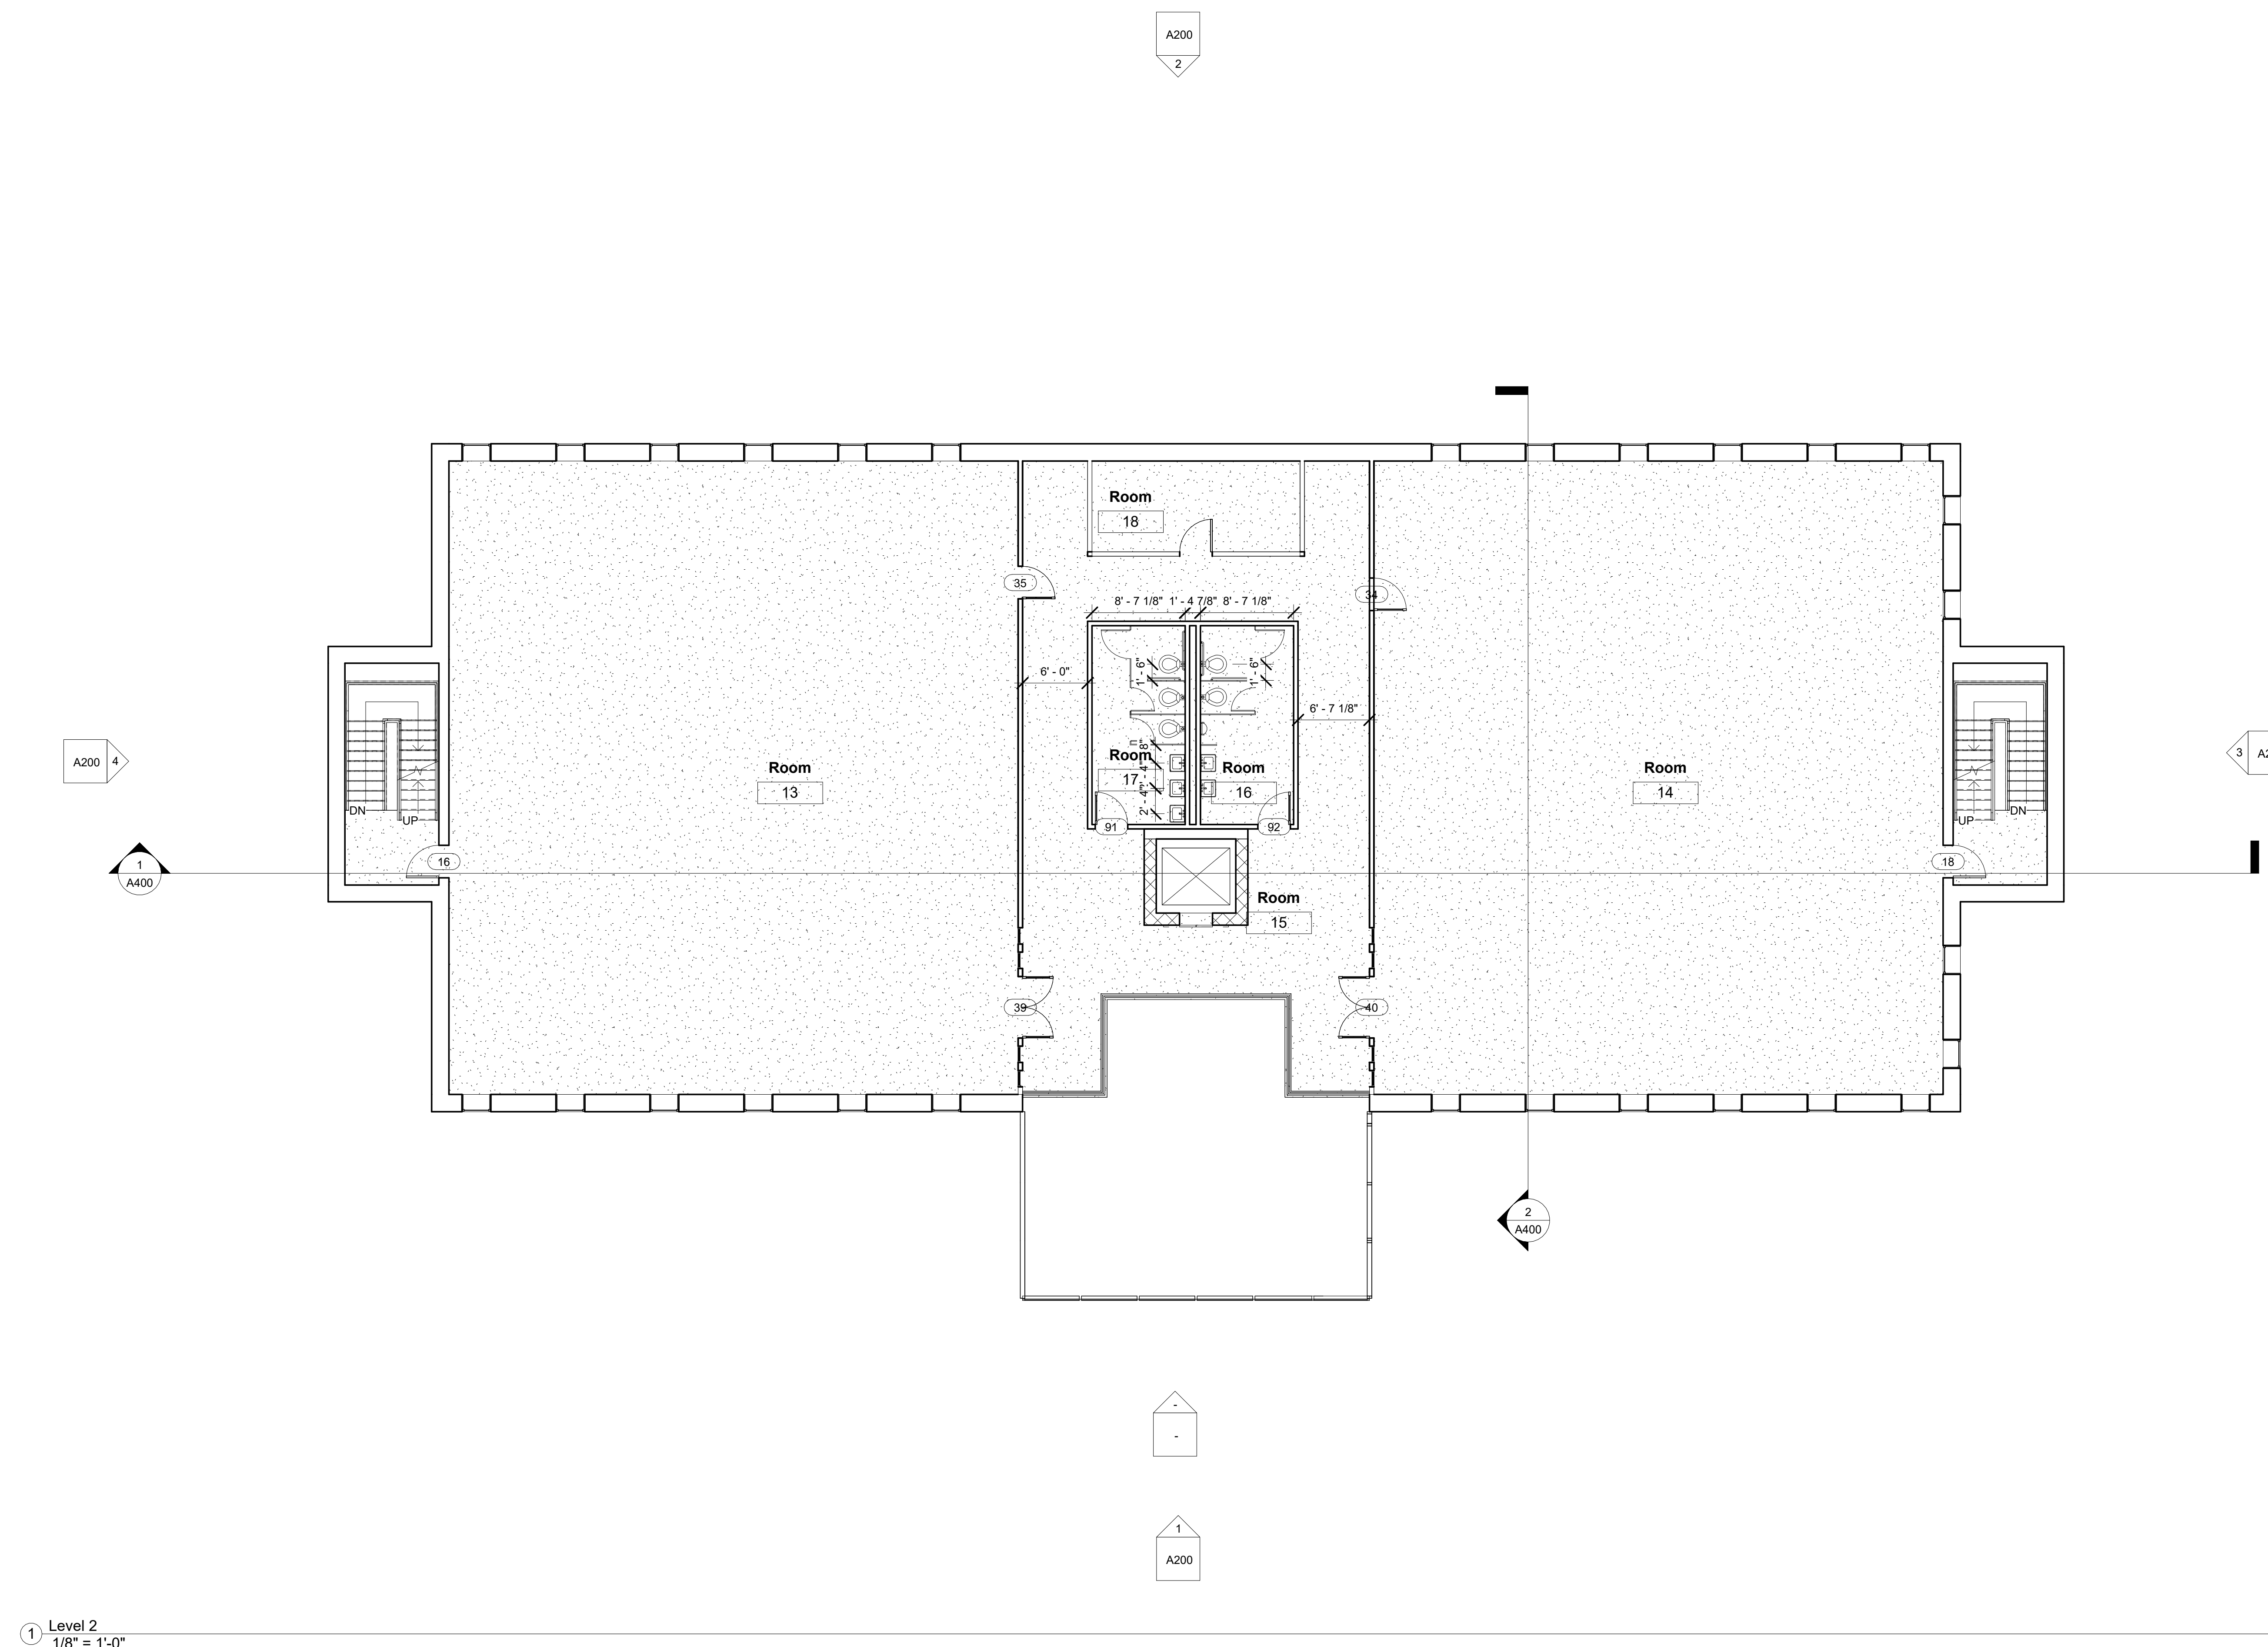

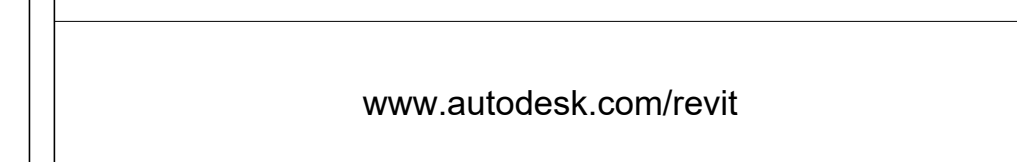

	Consultant
Address	
Address	
Address	
Phone	

[illegible]


Harbor View Offices
Level 3 Floor Plan

Project Number	2026-00
Date	June 3, 2026
Drawn By	Author
Checked By	Checker

A103

Scale	1/8" = 1'-0"
-------	--------------

6/6/2026 1:55:49 PM

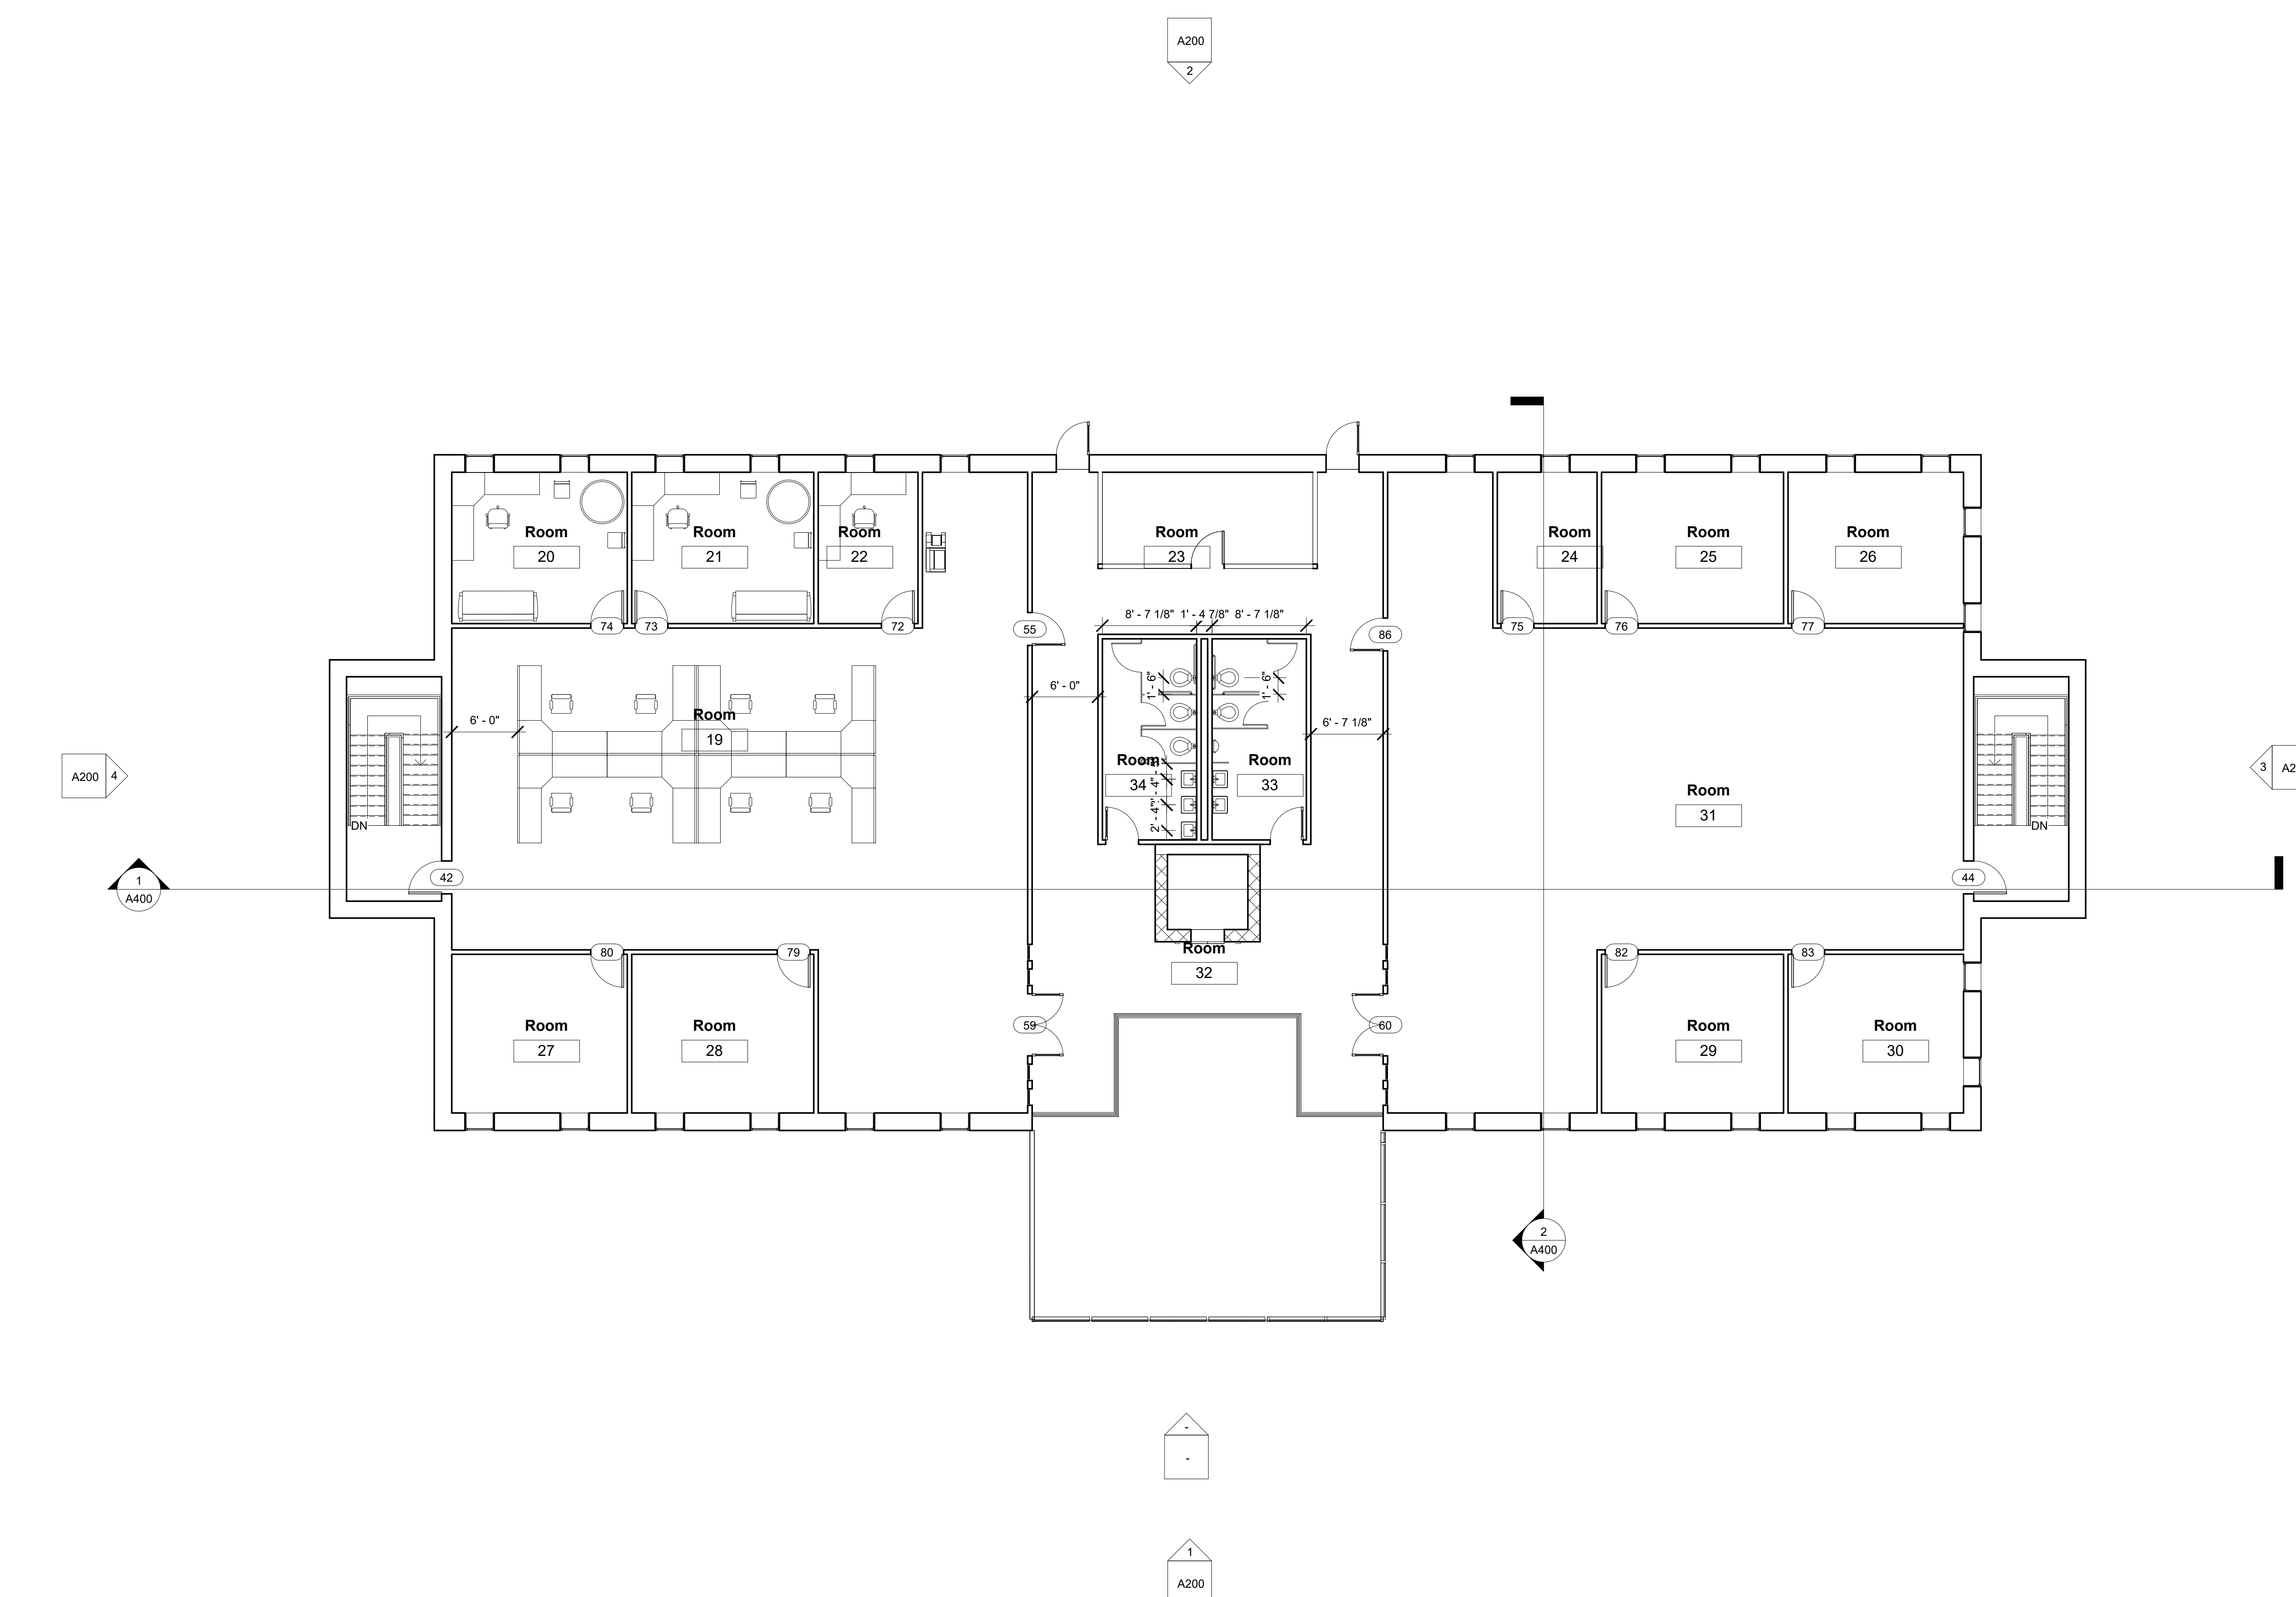

① Level 3
1/8" = 1'-0"



www.autodesk.com/revit


Consultant
Address
Address
Address
Phone

Consultant
Address
Address
Address
Phone

Consultant
Address
Address
Address
Phone

Consultant
Address
Address
Address
Phone

Consultant
Address
Address
Address
Phone

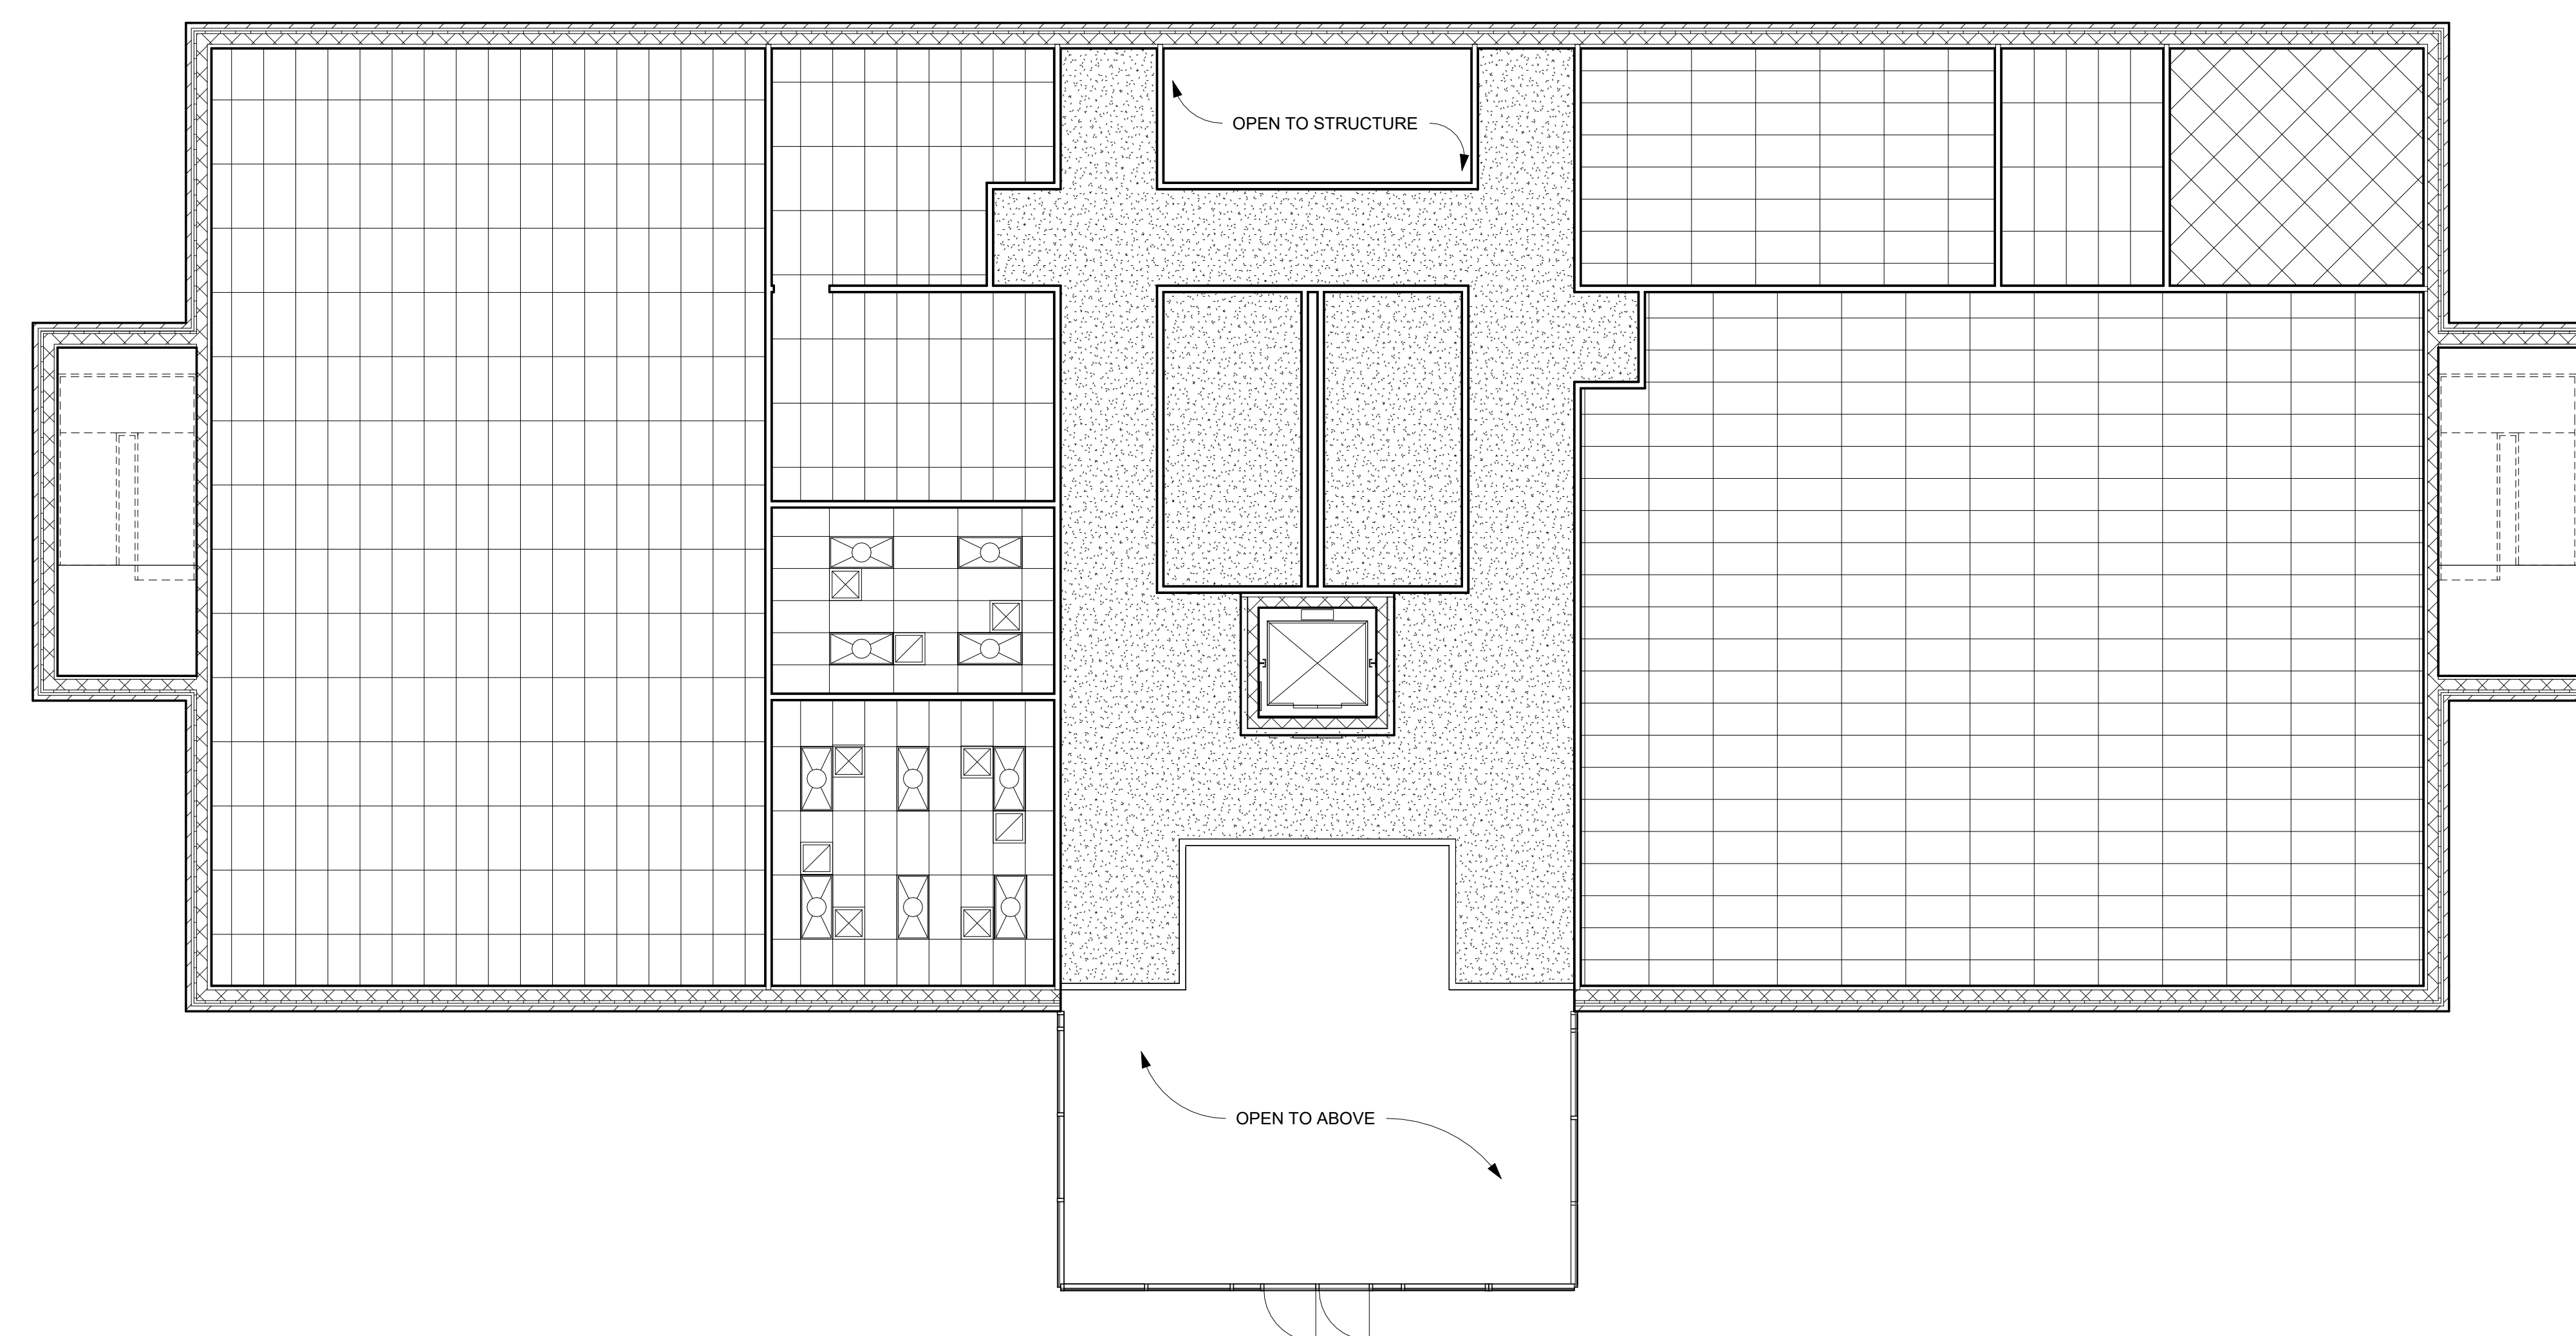

① Level 1
1/8" = 1'-0"

[illegible]

T.H.E Developers

Harbor View Offices

Level 1 Reflected Ceiling

Project Number	2026-001
----------------	----------

Date	June 3, 2026
------	--------------

Drawn By	Author
----------	--------

Checked By	Checker
------------	---------

A111

Scale	1/8" = 1'-0"
-------	--------------



www.autodesk.com/revit

Consultant
Address
Address
Address
Phone

Consultant
Address
Address
Address
Phone

Consultant
Address
Address
Address
Phone

Consultant
Address
Address
Address
Phone

Consultant
Address
Address
Address
Phone

[illegible]

T.H.E Developers

Harbor View Offices

Level 2 Reflected Ceiling

Project Number	2026-001
----------------	----------

Date	June 3, 2026
------	--------------


Drawn By	Author
----------	--------

Checked By	Checker
------------	---------

A112

Scale	1/8" = 1'-0"
-------	--------------

6/6/2026 1:55:50 PM

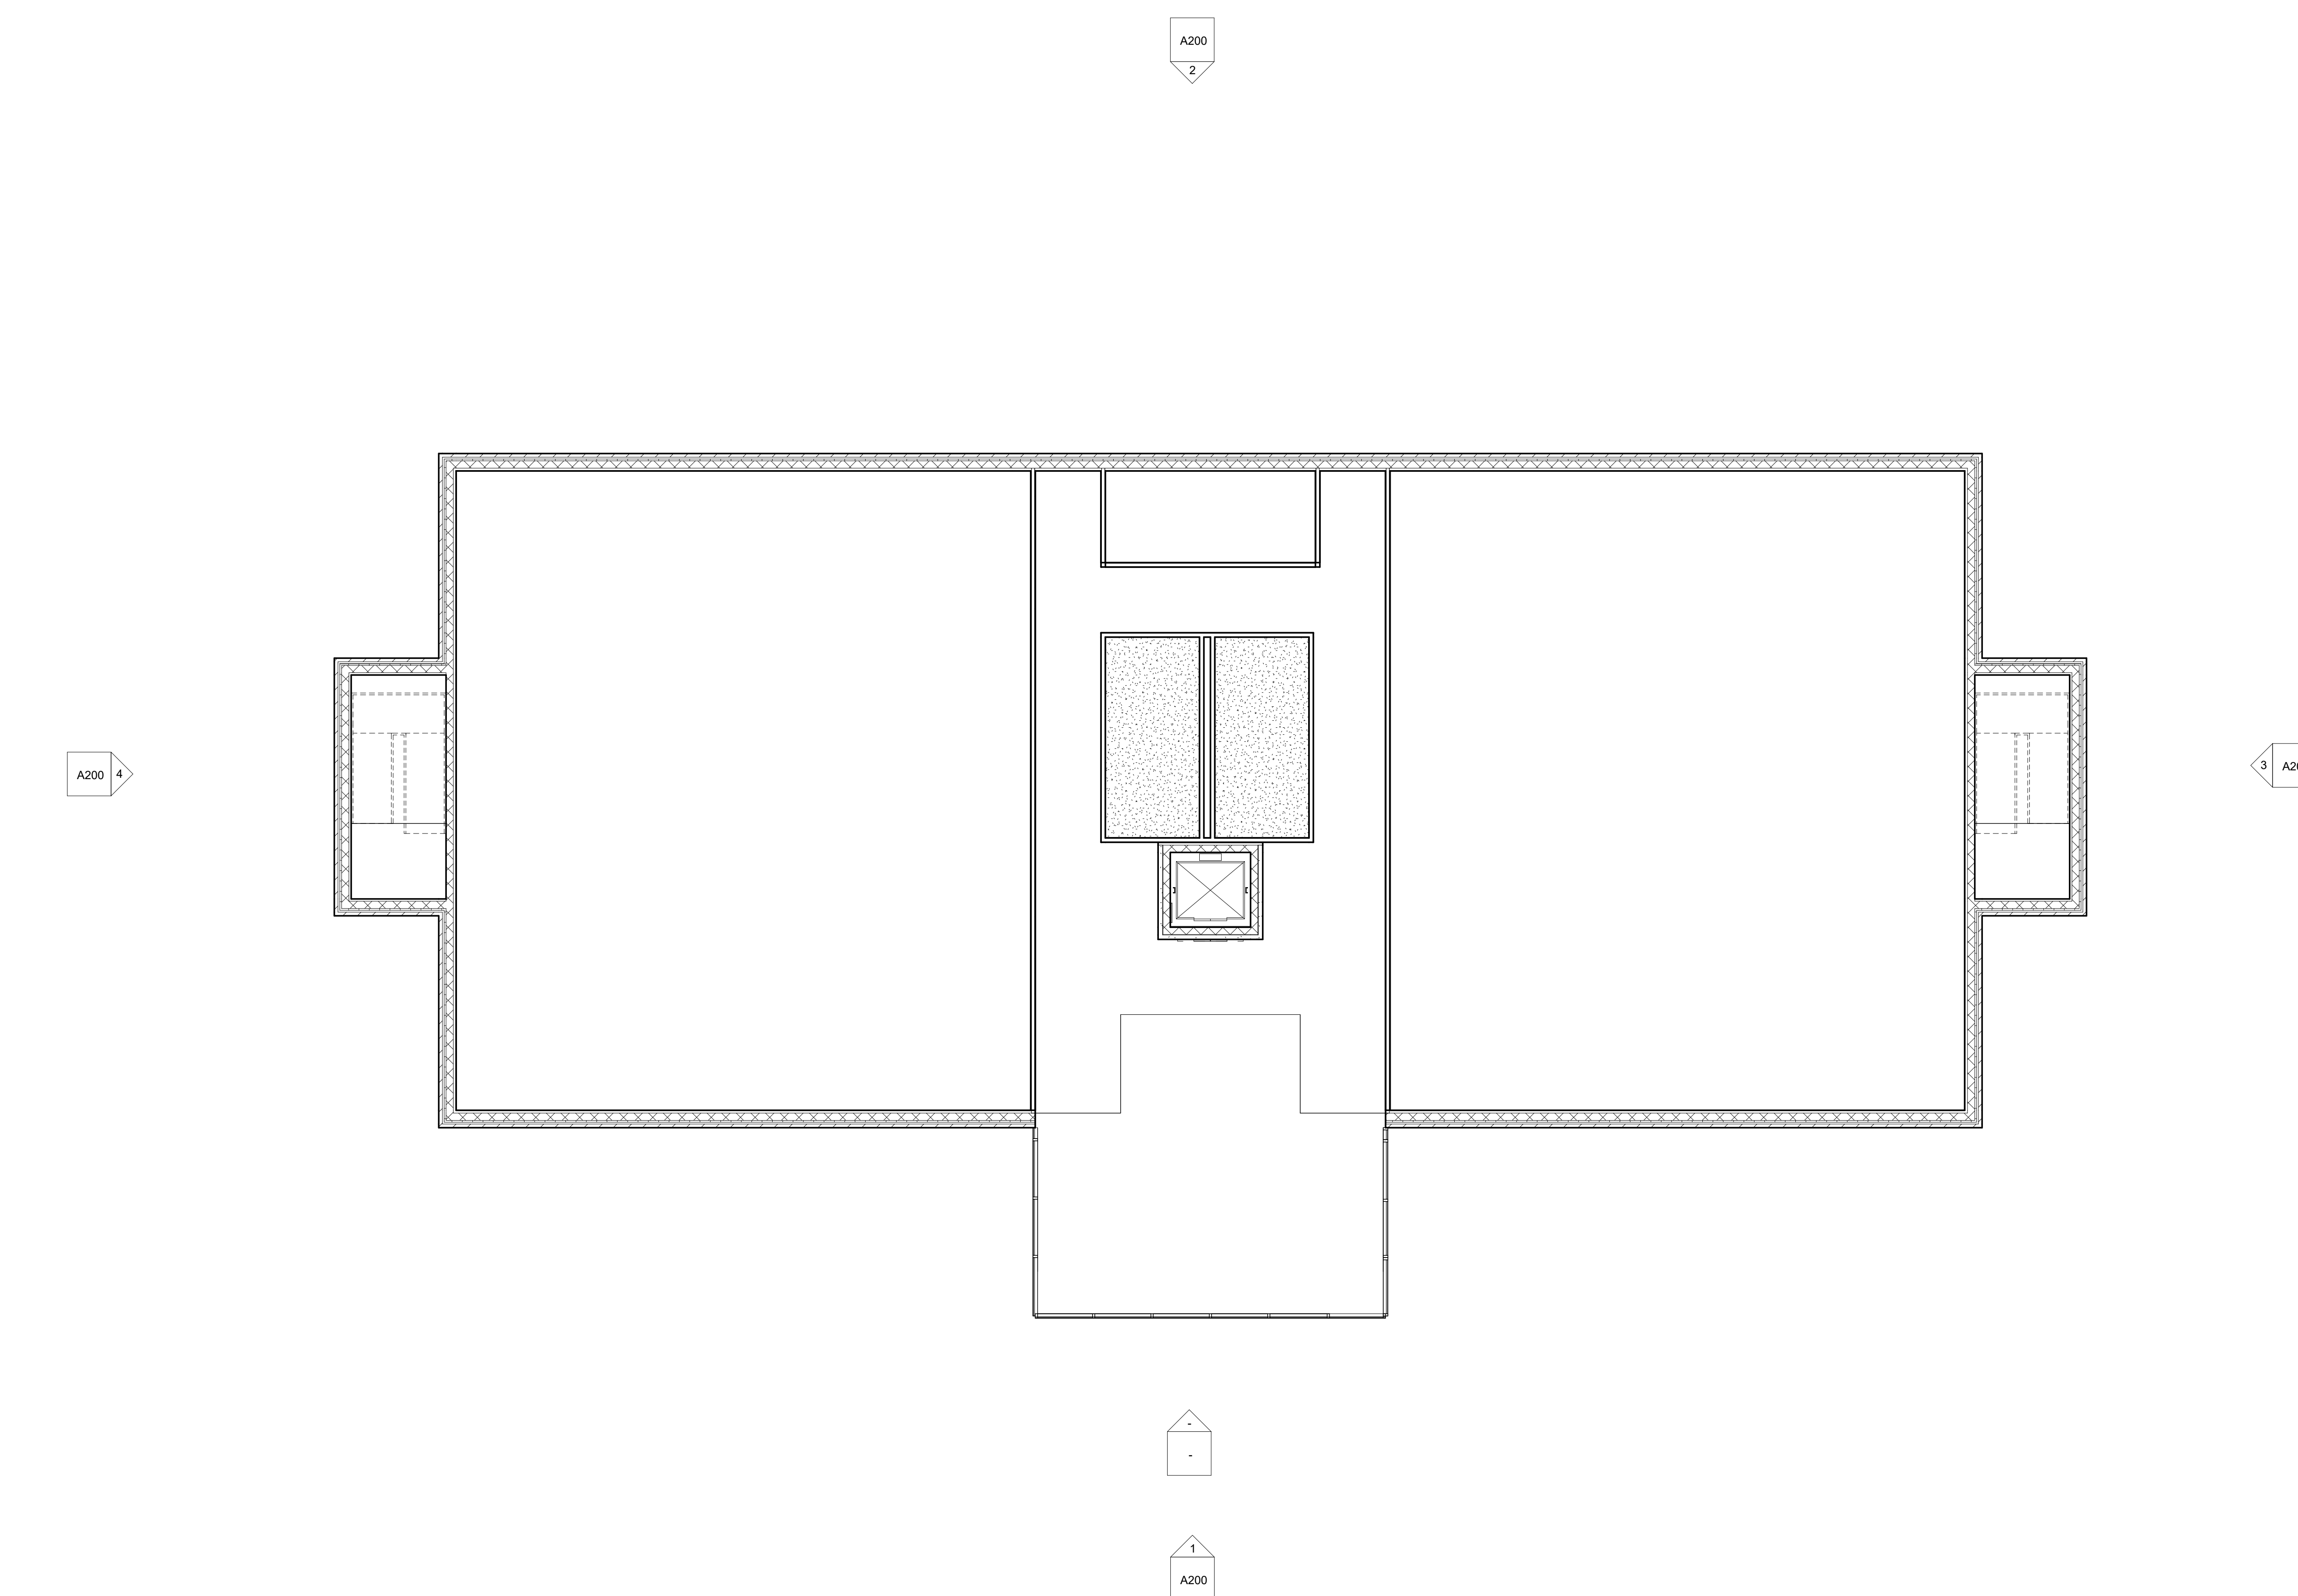

① Level 2
1/8" = 1'-0"



www.autodesk.com/revit

Consultant
Address
Address
Address
Phone

Consultant
Address
Address
Address
Phone

Consultant
Address
Address
Address
Phone

Consultant
Address
Address
Address
Phone

Consultant
Address
Address
Address
Phone

[illegible]

T.H.E Developers

Harbor View Offices

Level 3 Reflected Ceiling

Project Number	2026-001
----------------	----------


Date	June 3, 2026
------	--------------

Drawn By	Author
----------	--------

Checked By	Checker
------------	---------

A113

Scale	1/8" = 1'-0"
-------	--------------

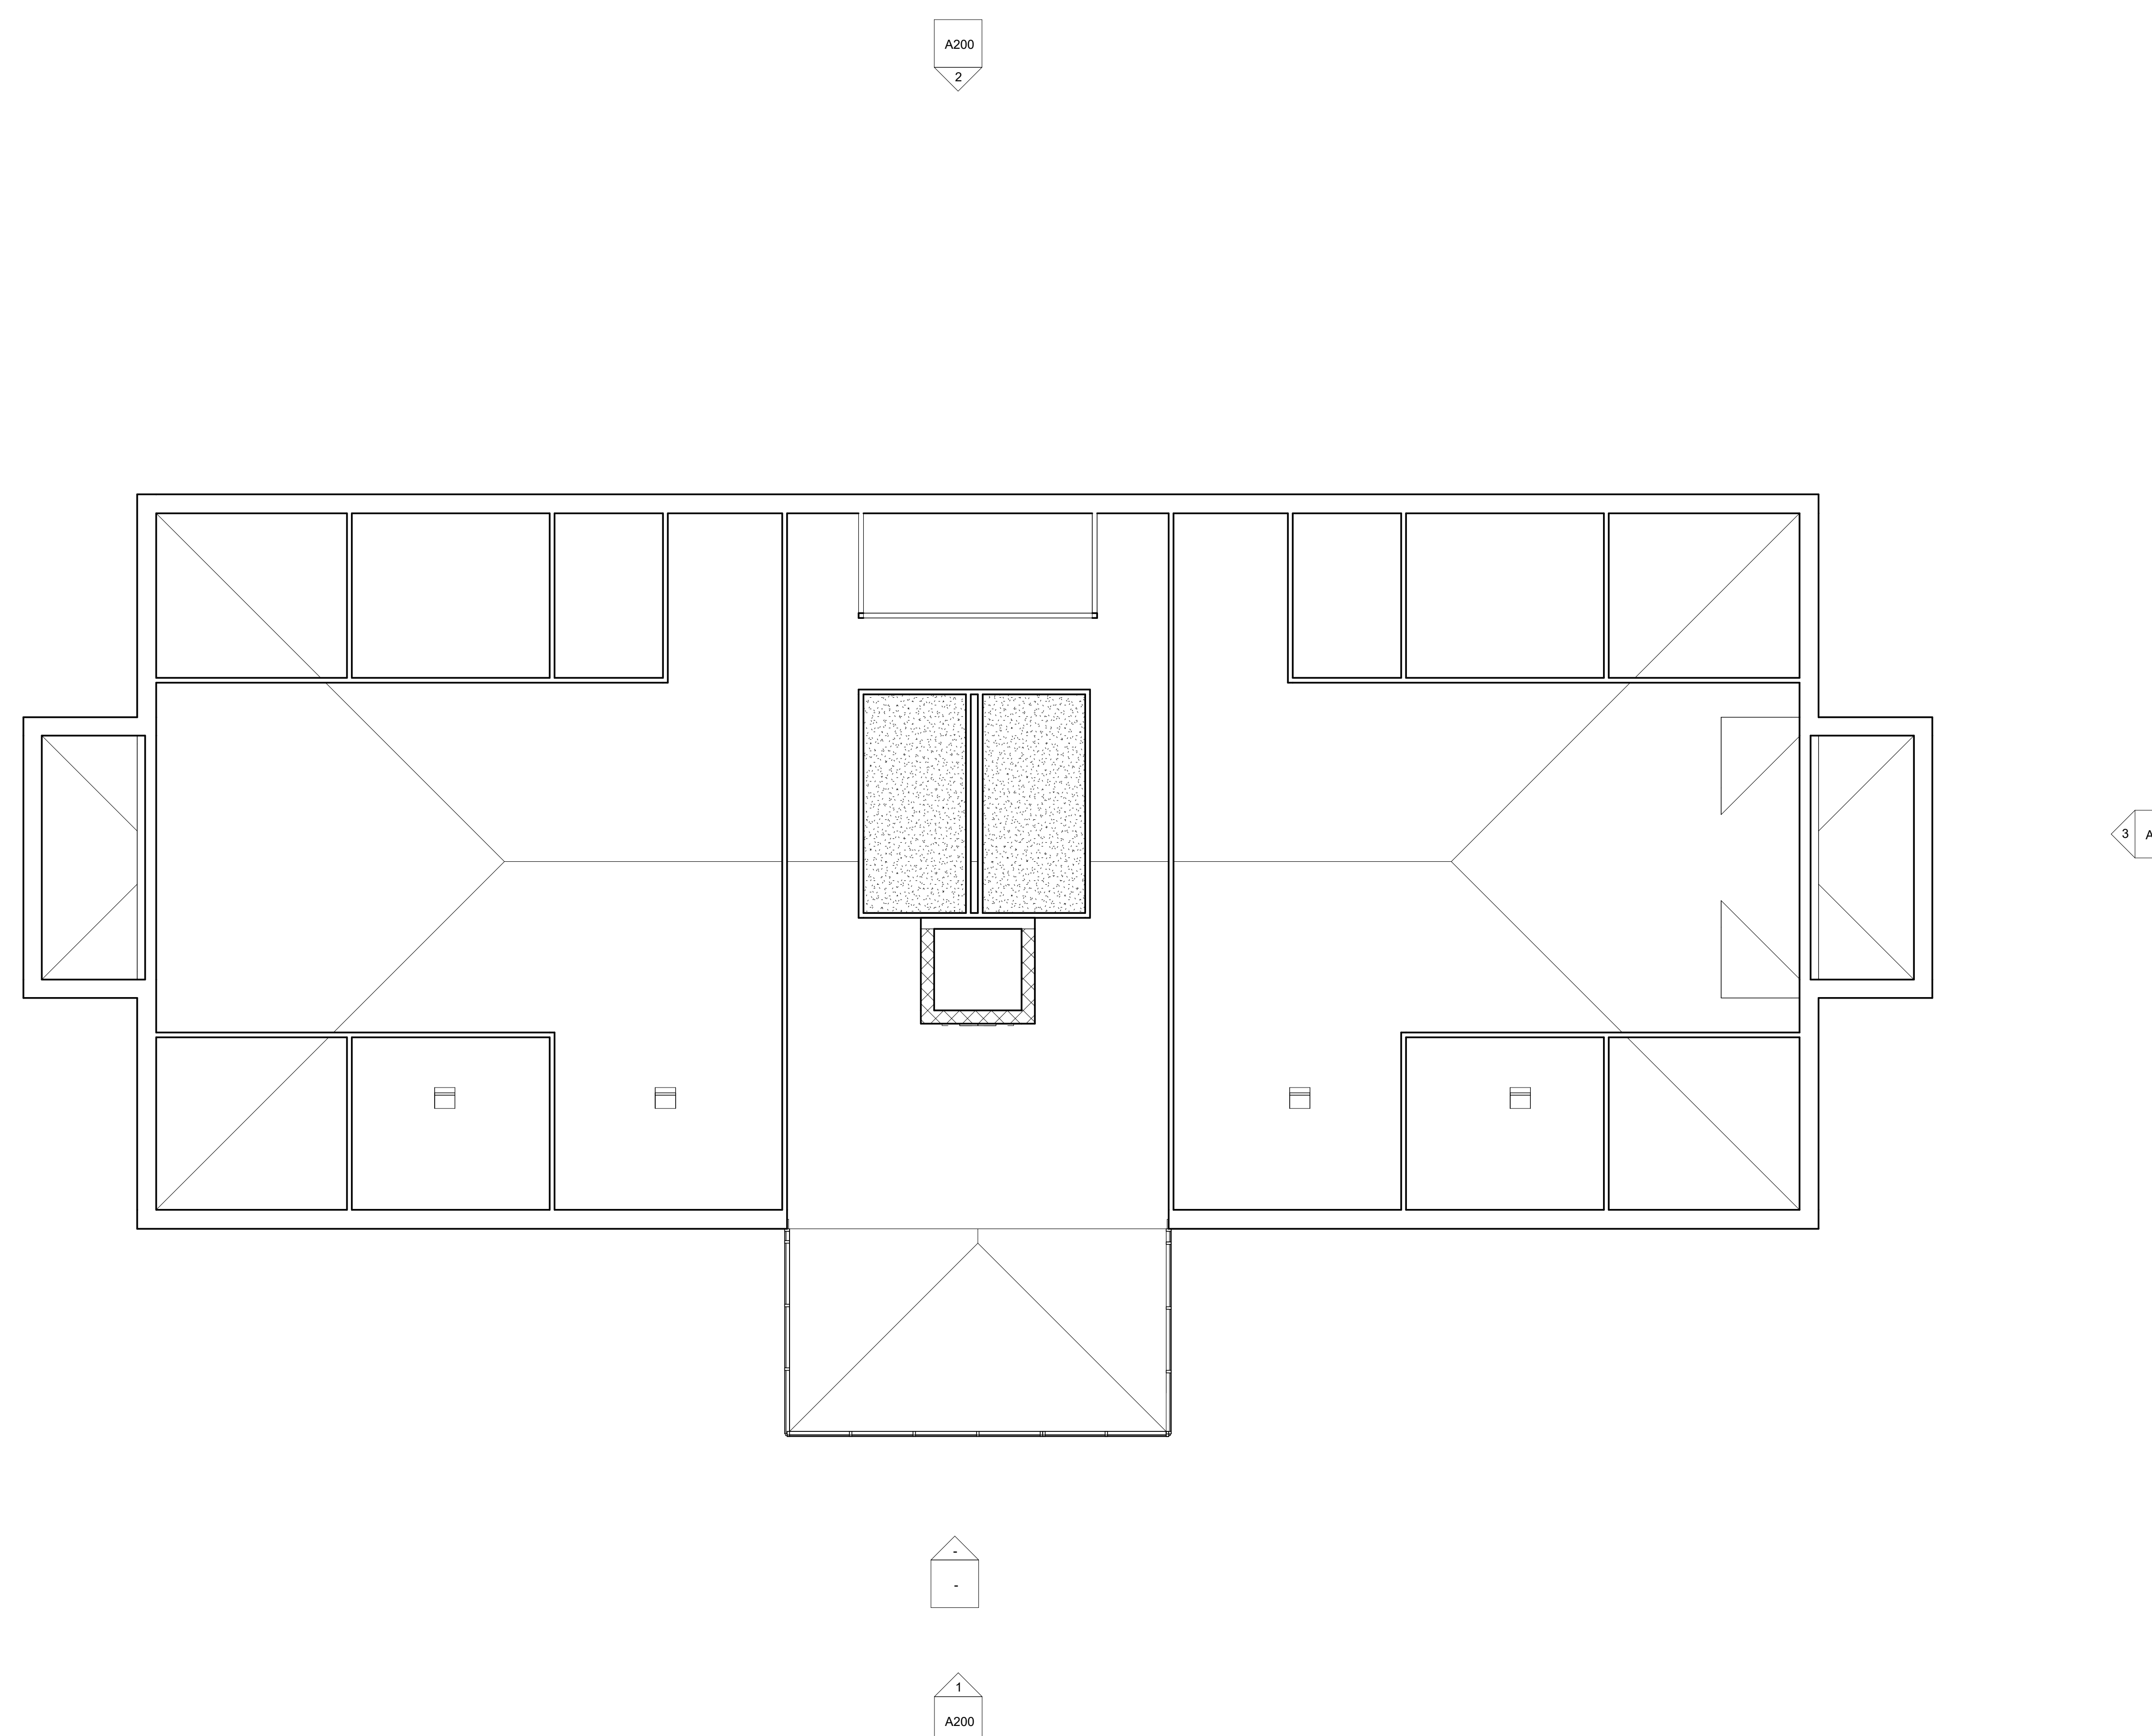

① Level 3
1/8" = 1'-0"



www.autodesk.com/revit

Consultant
Address
Address
Address
Phone

Consultant	Address	Address	Address	Phone
------------	---------	---------	---------	-------

Consultant	Address	Address	Address	Phone
------------	---------	---------	---------	-------

Consultant	Address	Address	Address	Phone
------------	---------	---------	---------	-------

Consultant
Address
Address
Address
Phone

[illegible]

T.H.E Developers





Harbor View Offices
Exterior Elevations

Project Number	2026-001
Date	June 3, 2026
Drawn By	Author
Checked By	Checker

A200

Scale	1/8" = 1'-0"
-------	--------------

.....

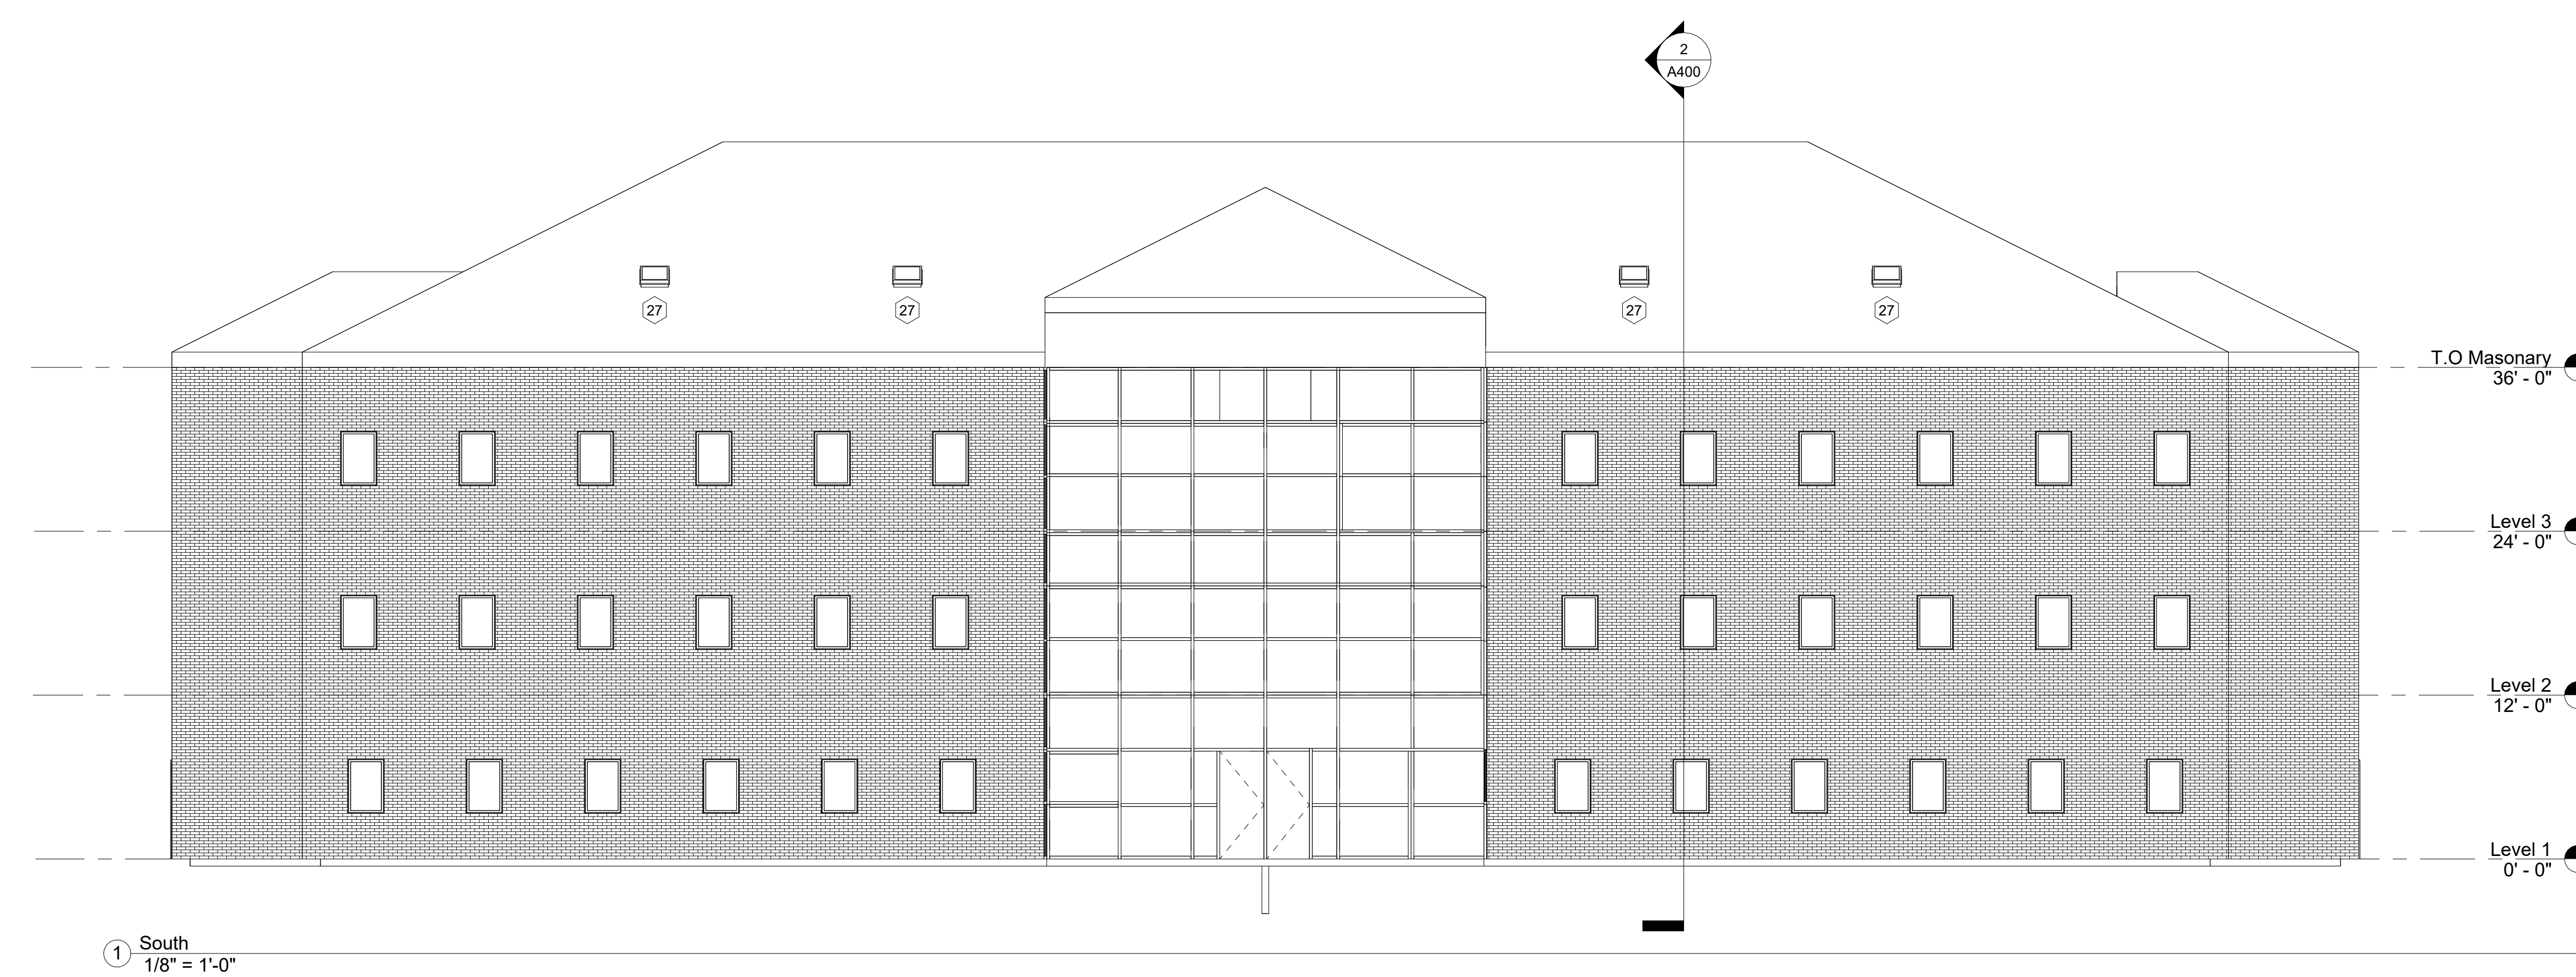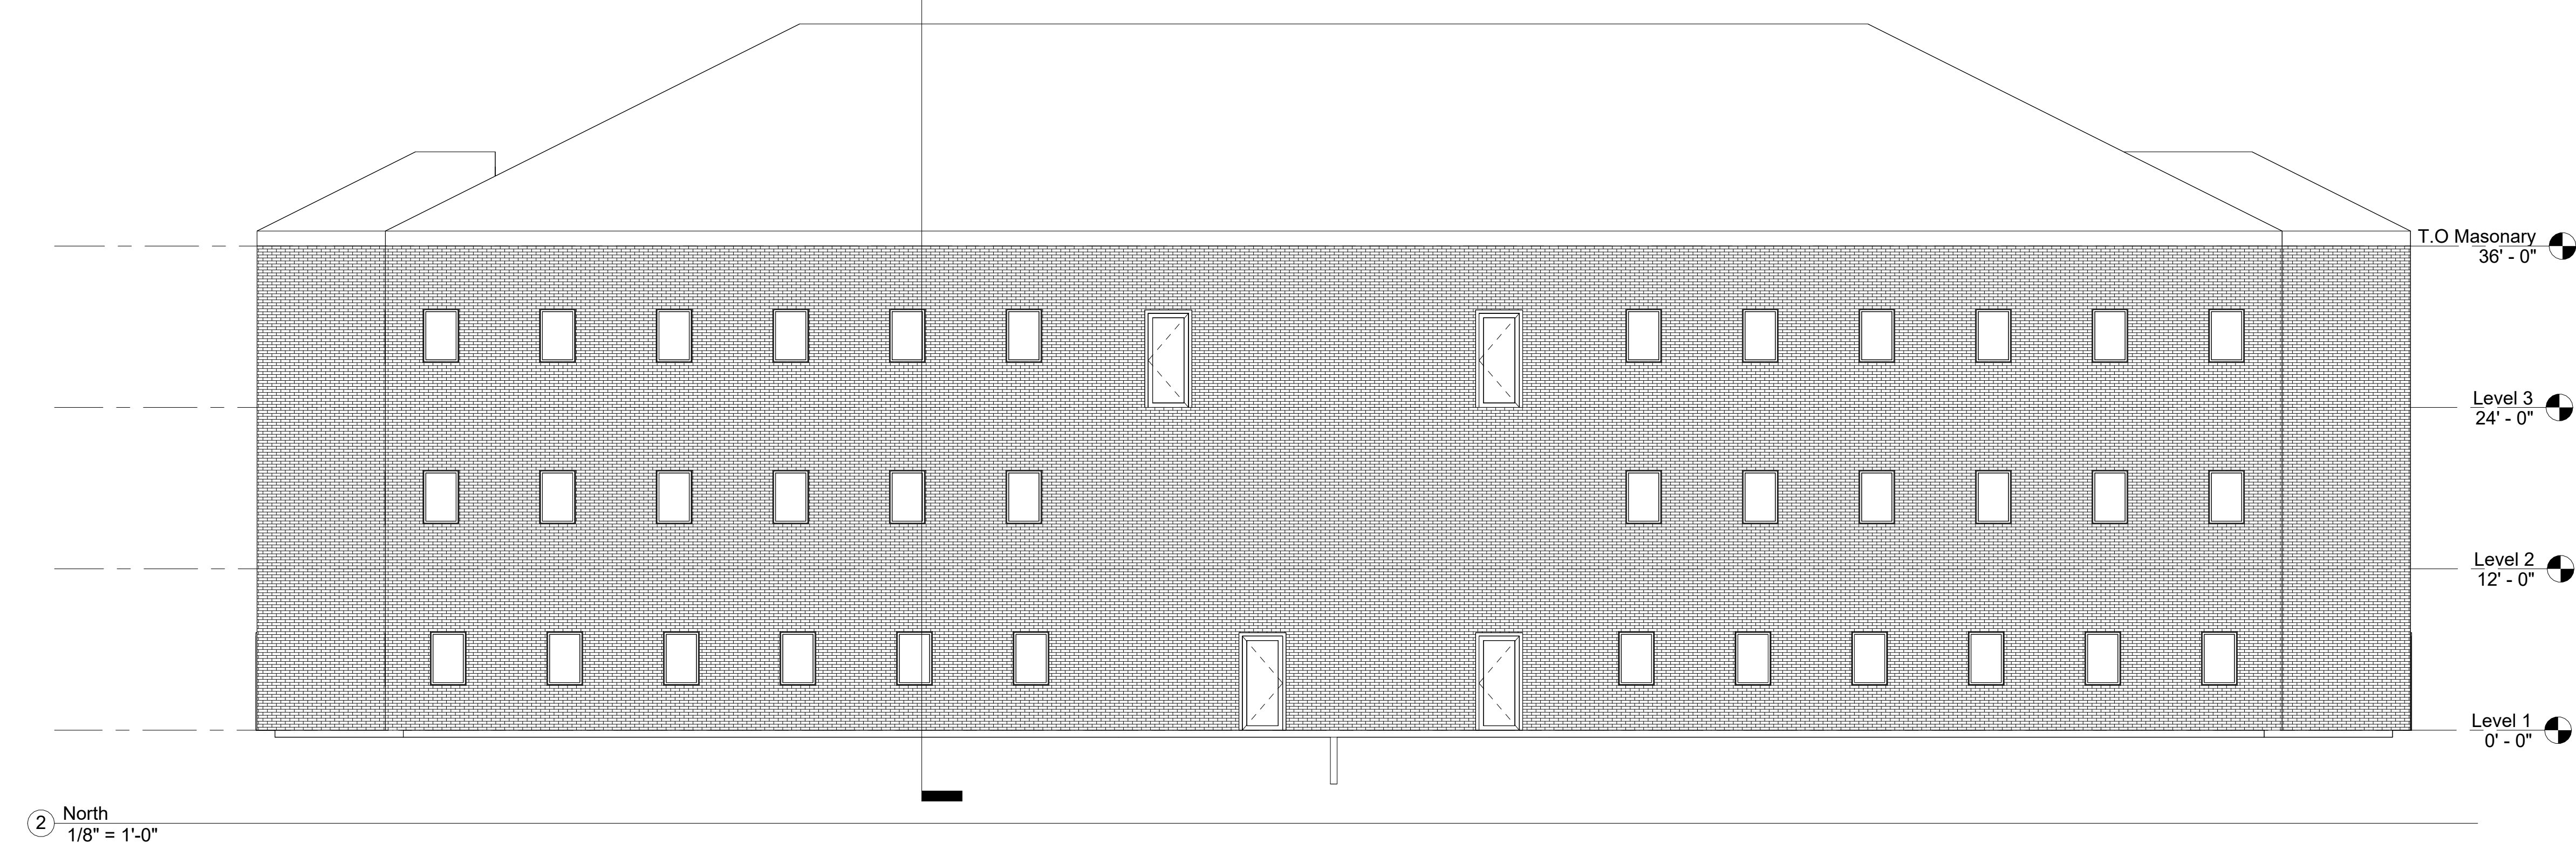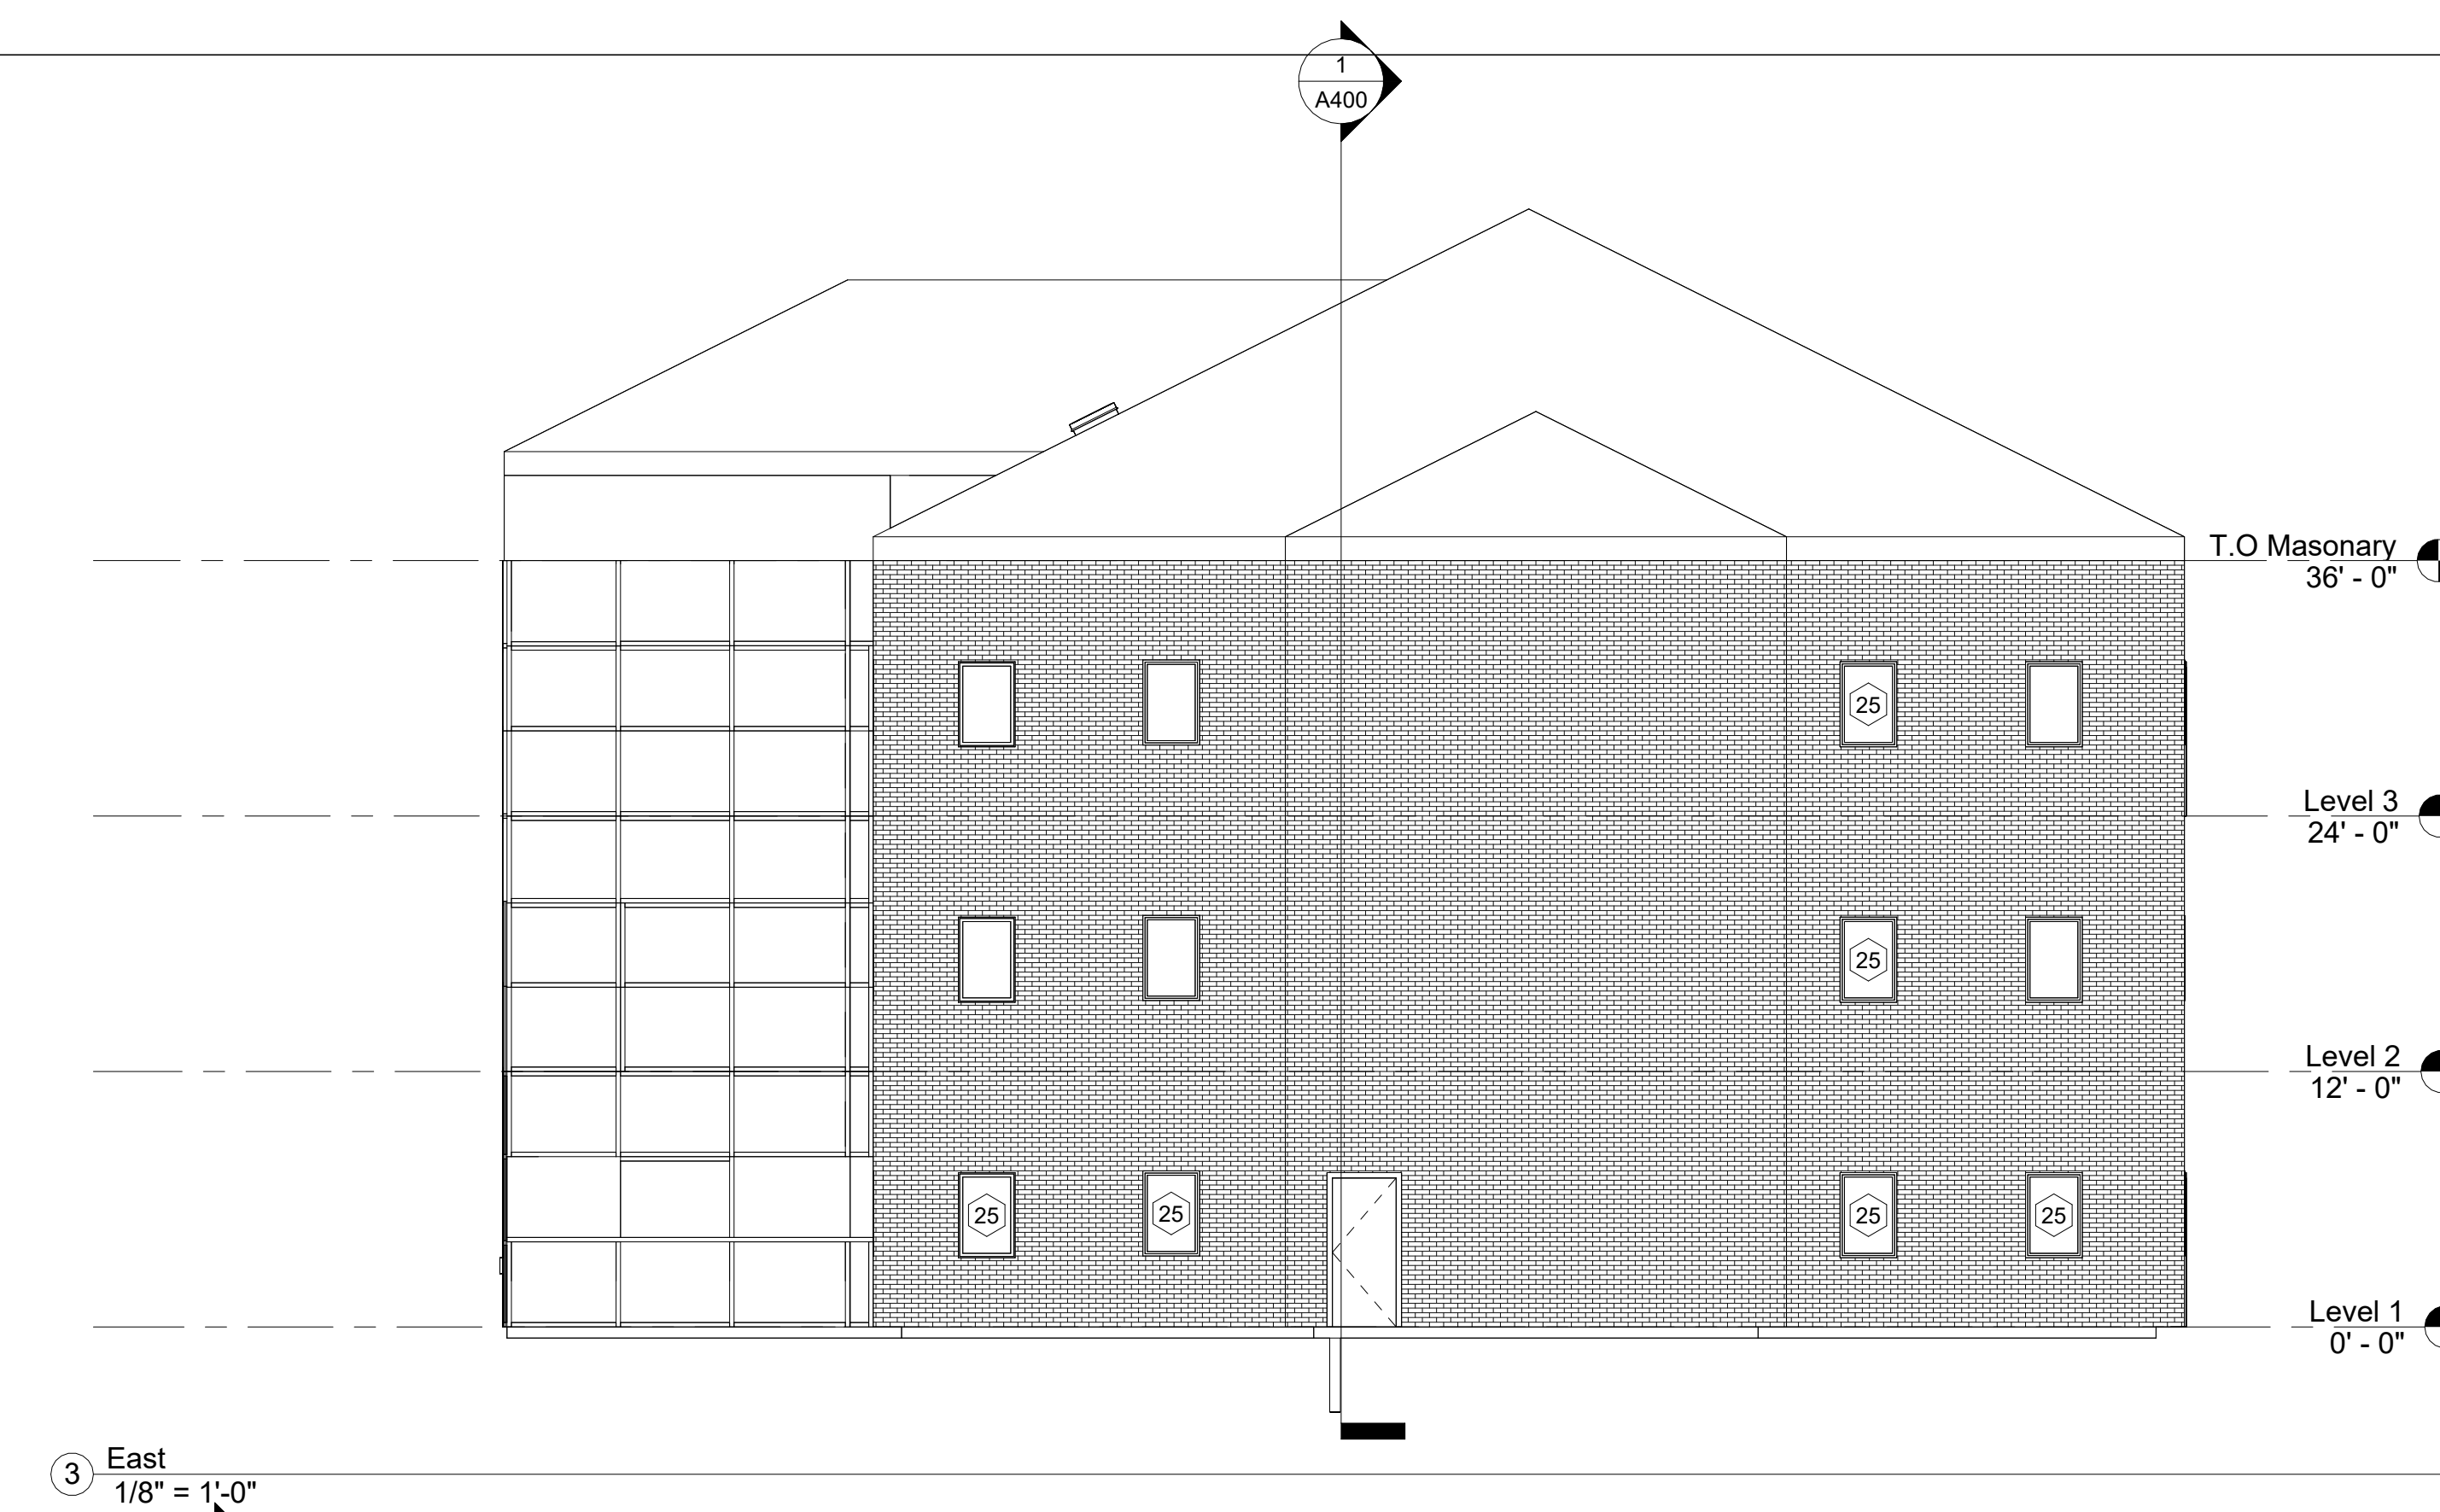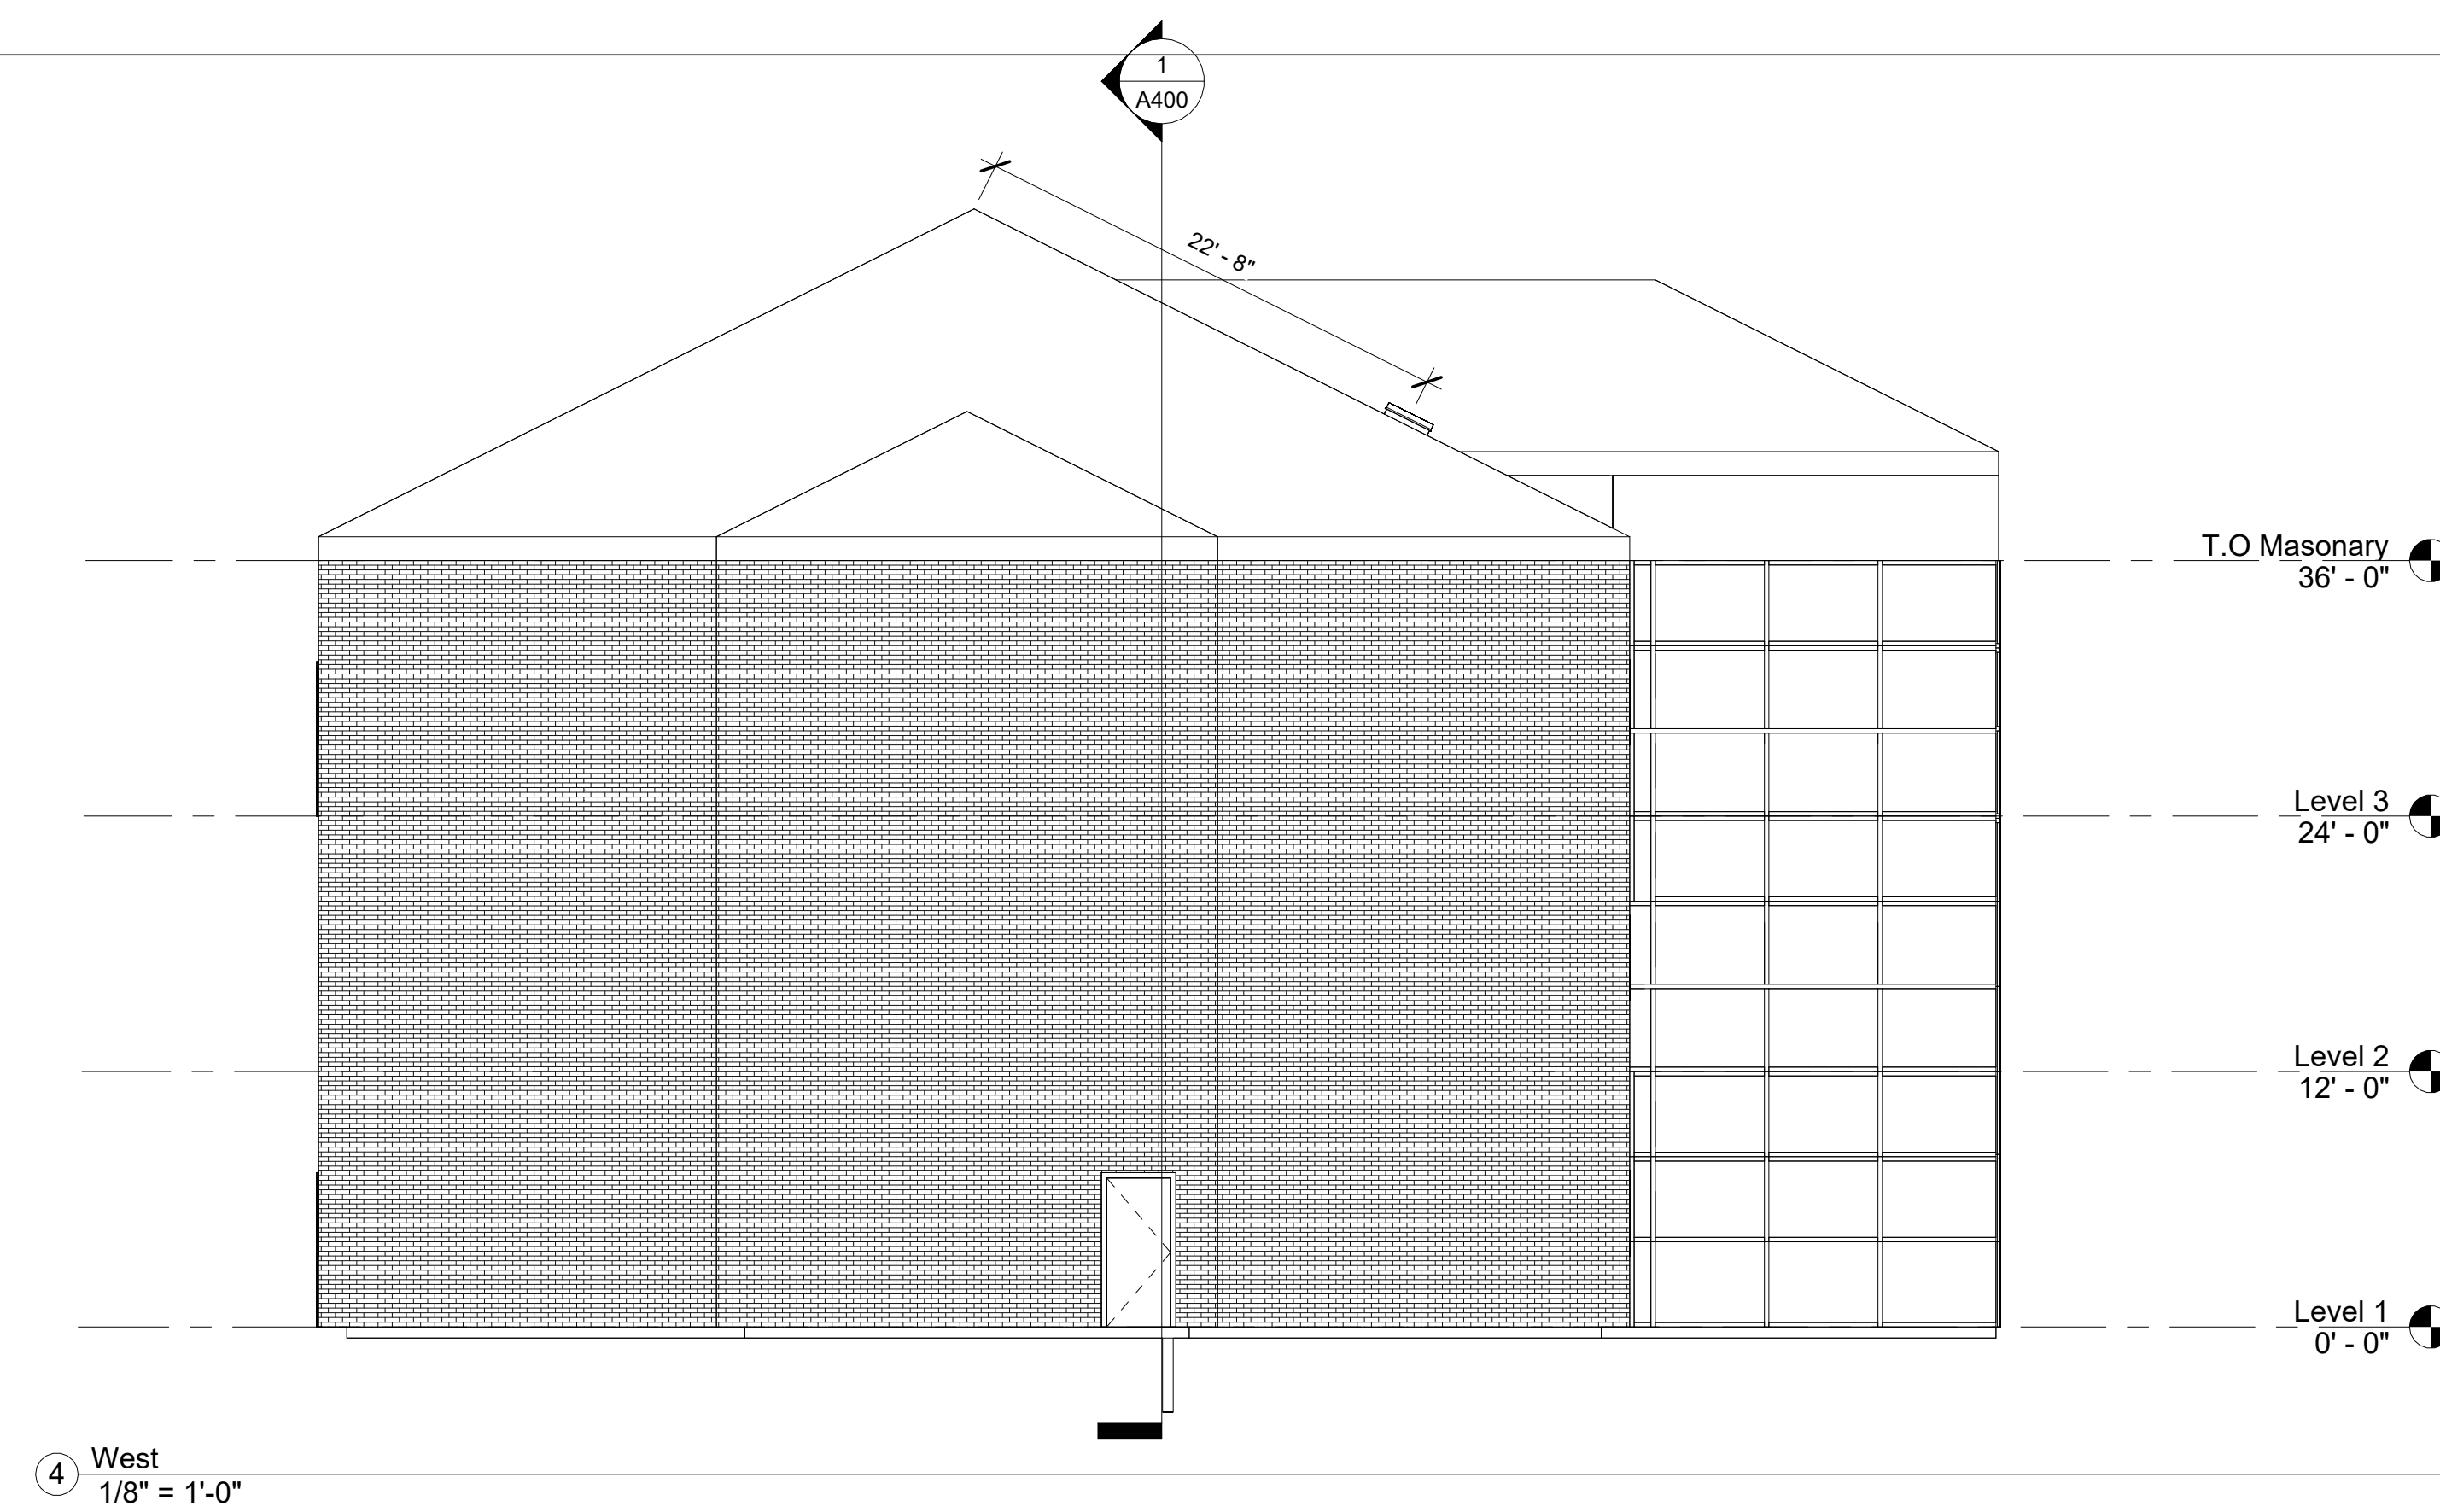



www.autodesk.com/revit

Consultant
Address
Address
Address
Phone

Consultant	Address	Address	Address	Phone
------------	---------	---------	---------	-------

Consultant	Address	Address	Address	Phone
------------	---------	---------	---------	-------

Consultant	Address	Address	Address	Phone
------------	---------	---------	---------	-------

Consultant	Address	Address	Address	Phone
------------	---------	---------	---------	-------

[illegible]

T.H.E Developers


Harbor View Offices
Wall Sections

Project Number	2026-001
Date	June 3, 2026
Drawn By	Author
Checked By	Checker

A400

Scale	As indicated
-------	--------------


.....

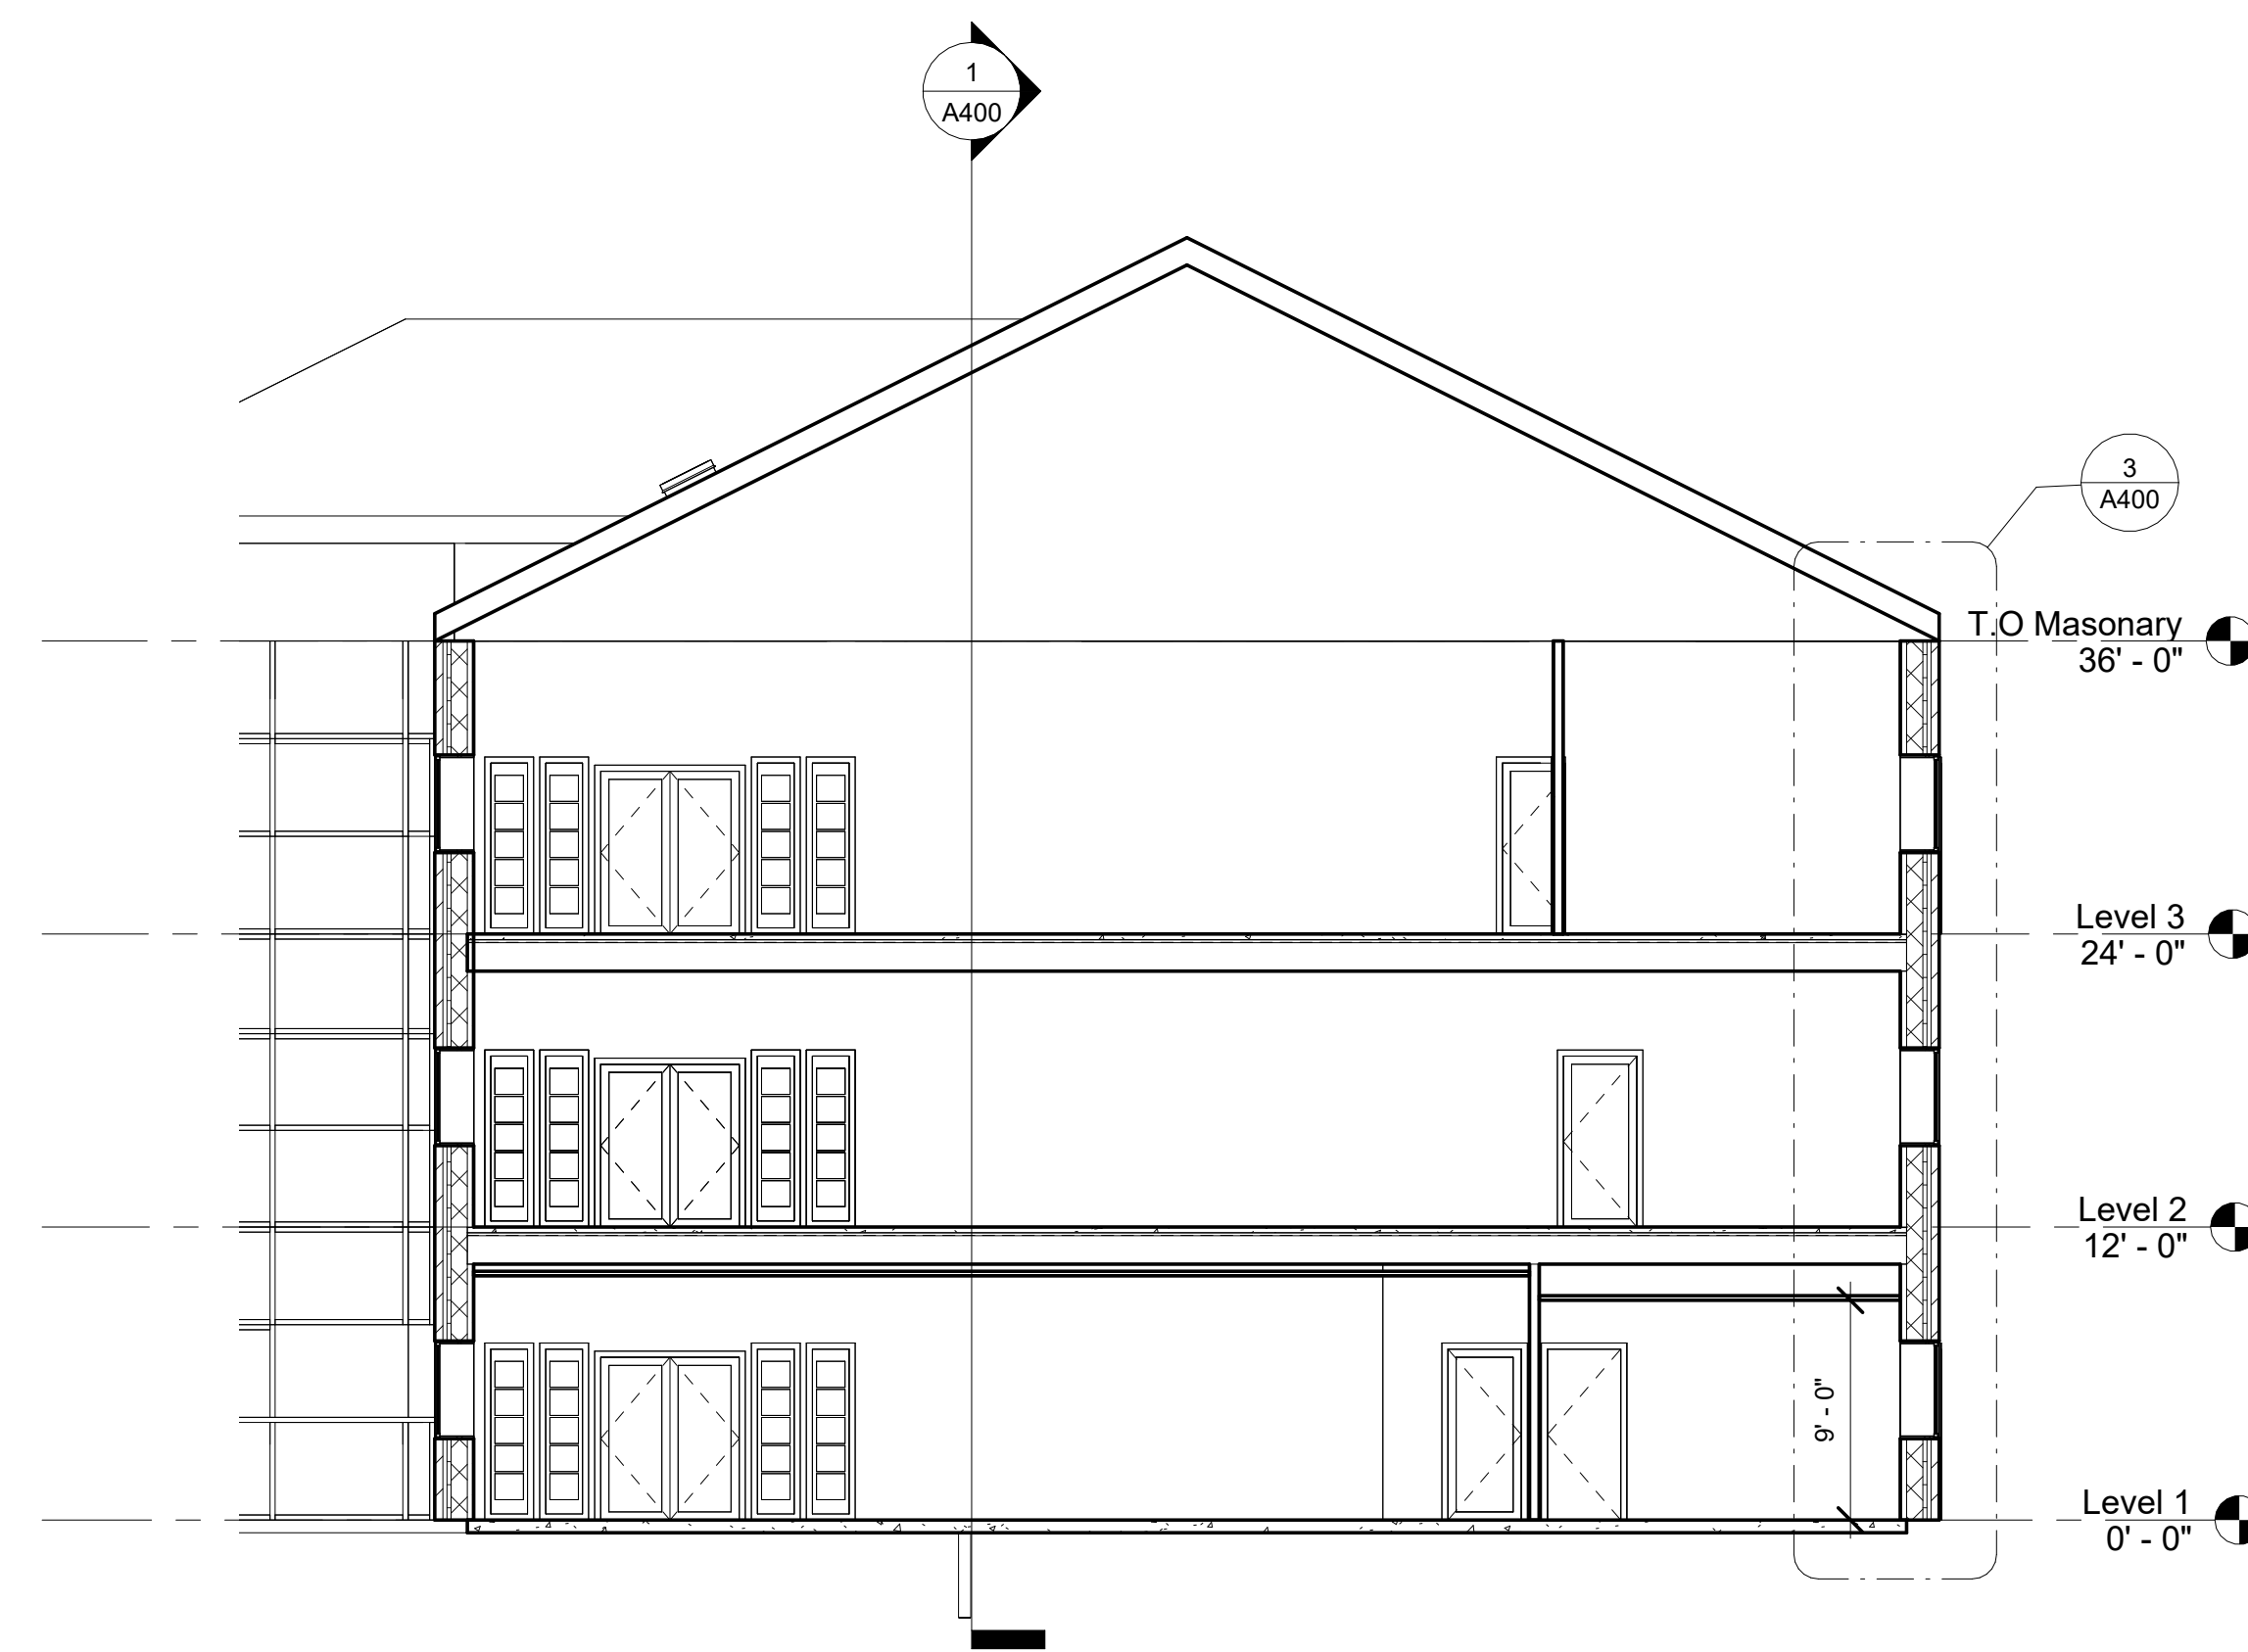

② Cross Section 1
1/8" = 1'-0"



① Longitudinal Section
1/8" = 1'-0"

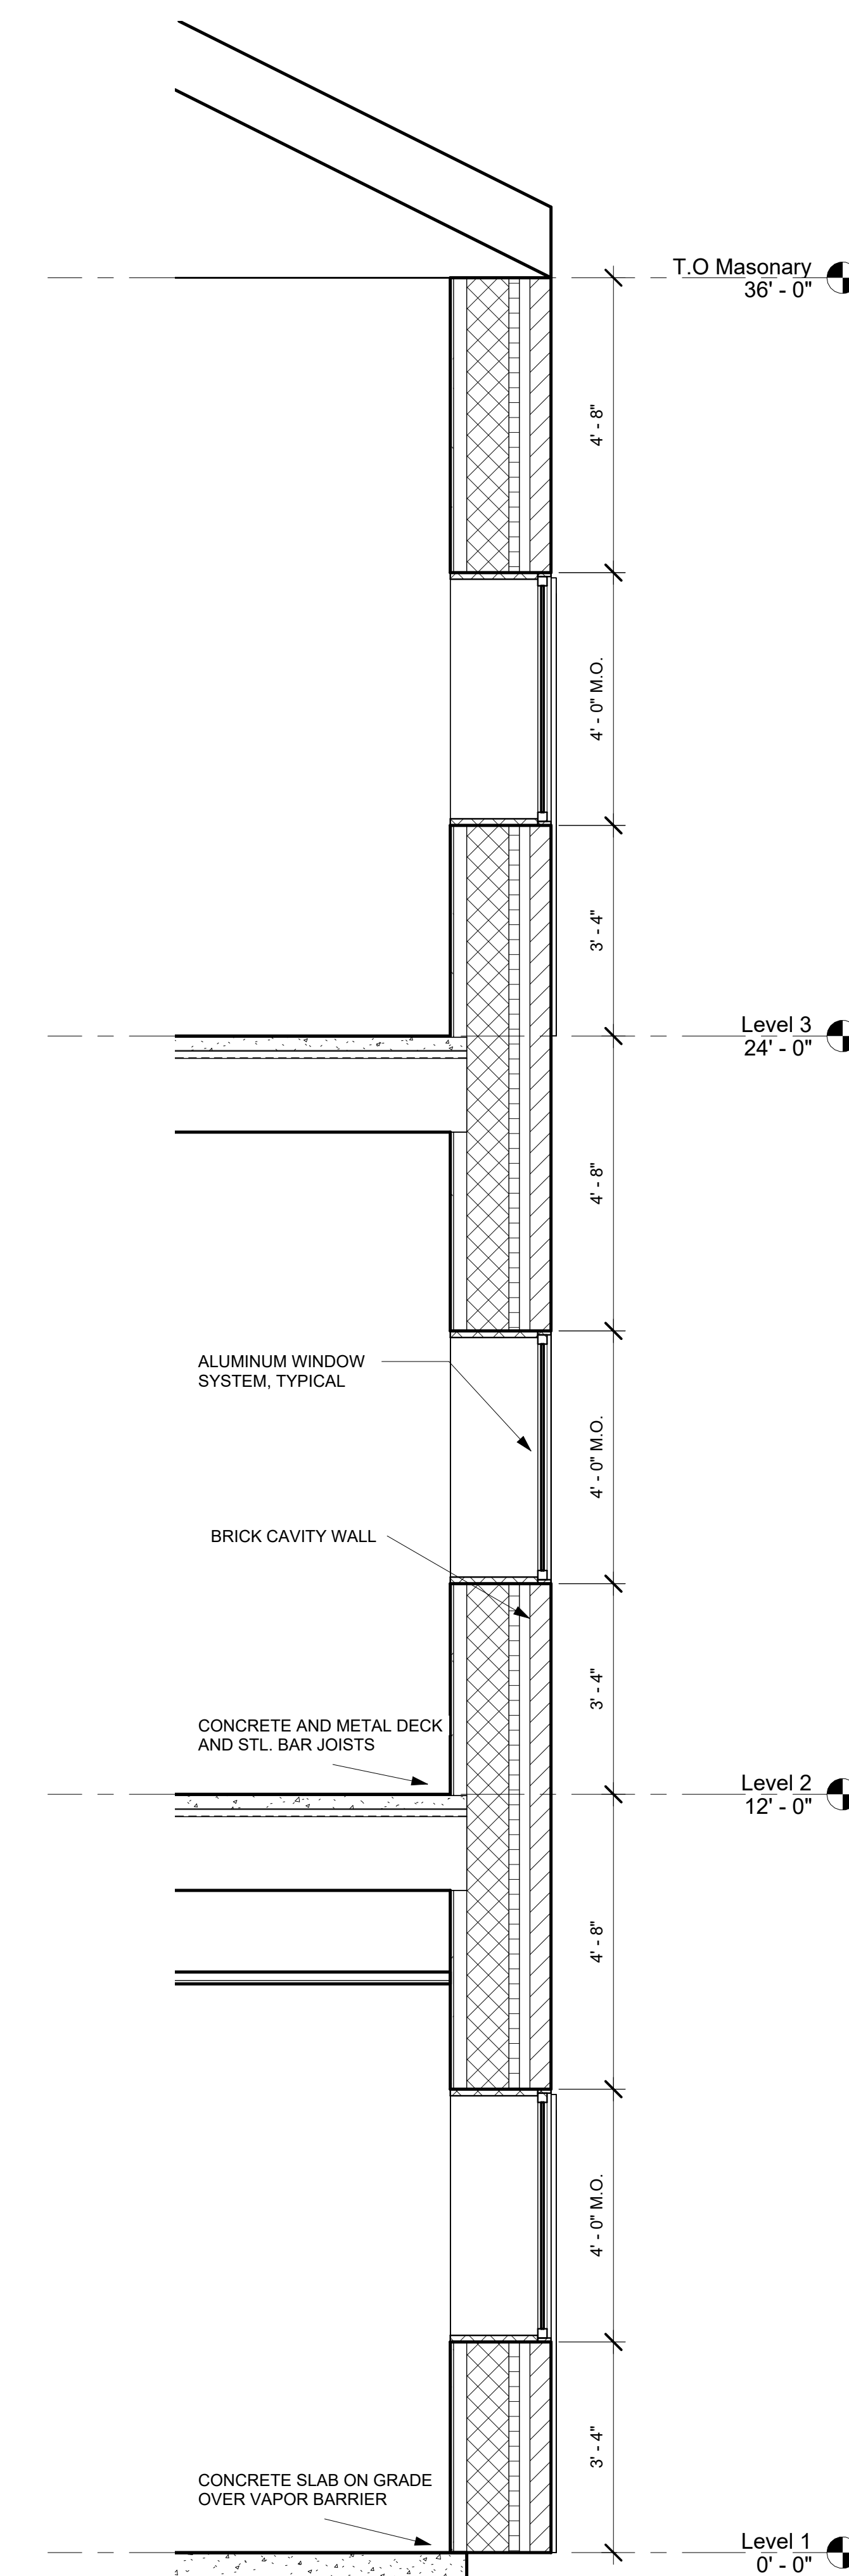

③ Cross Section 1 - Callout 1
1/2" = 1'-0"



www.autodesk.com/revit


Consultant
Address
Address
Address
Phone

Consultant	Address	Address	Address	Phone
------------	---------	---------	---------	-------


Consultant	Address	Address	Address	Phone
------------	---------	---------	---------	-------

Consultant
Address
Address
Address
Phone

Consultant
Address
Address
Address
Phone

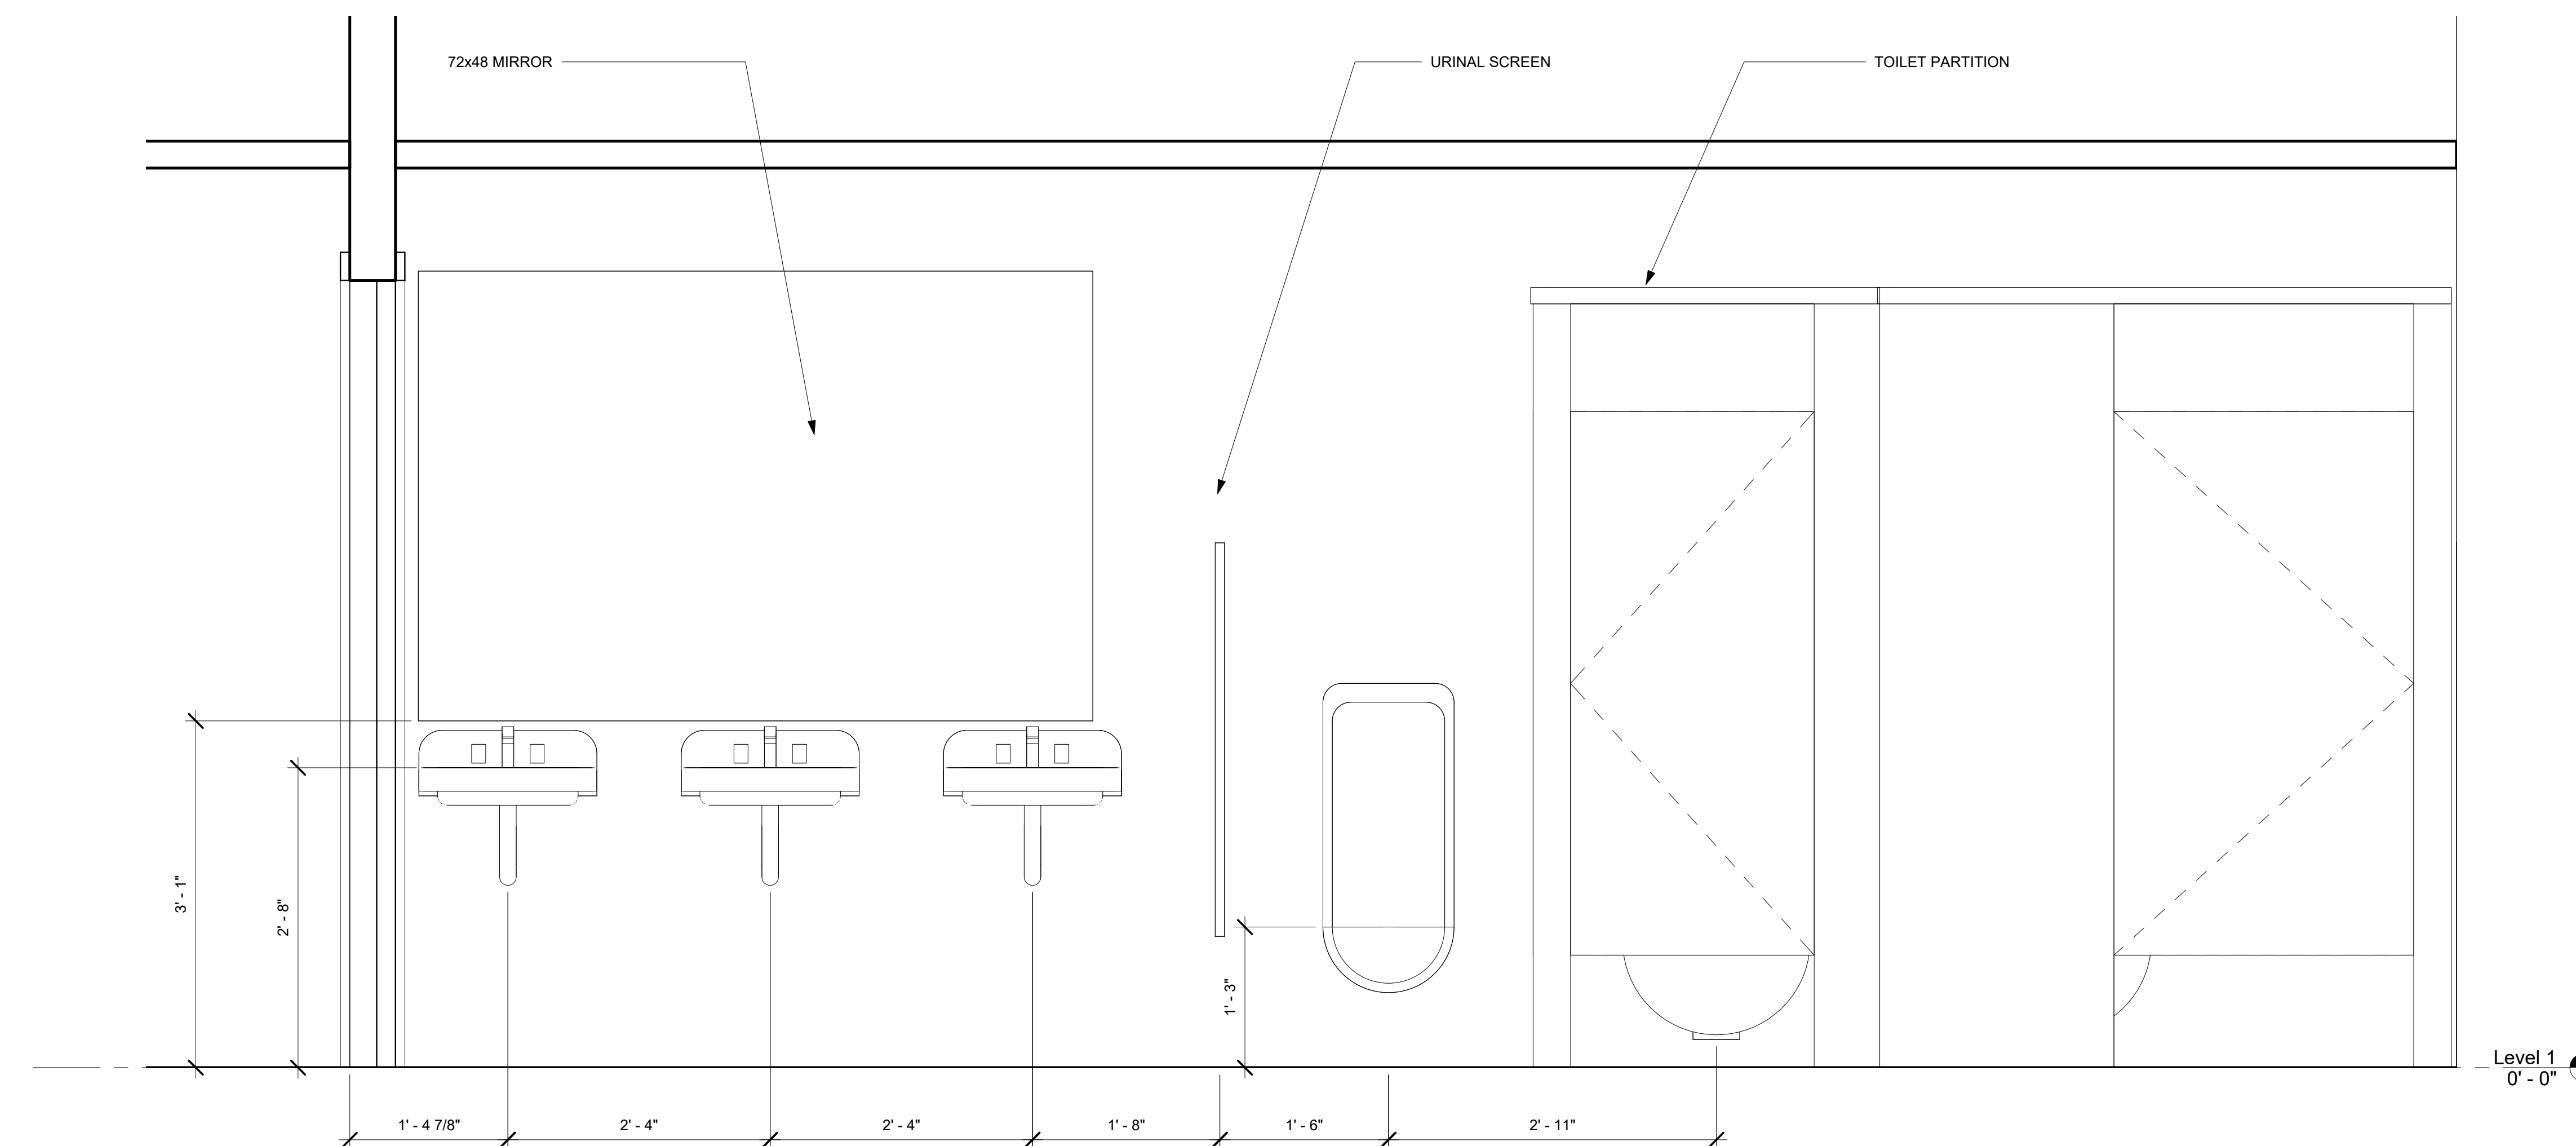

2 Mens Restroom
1" = 1'-0"

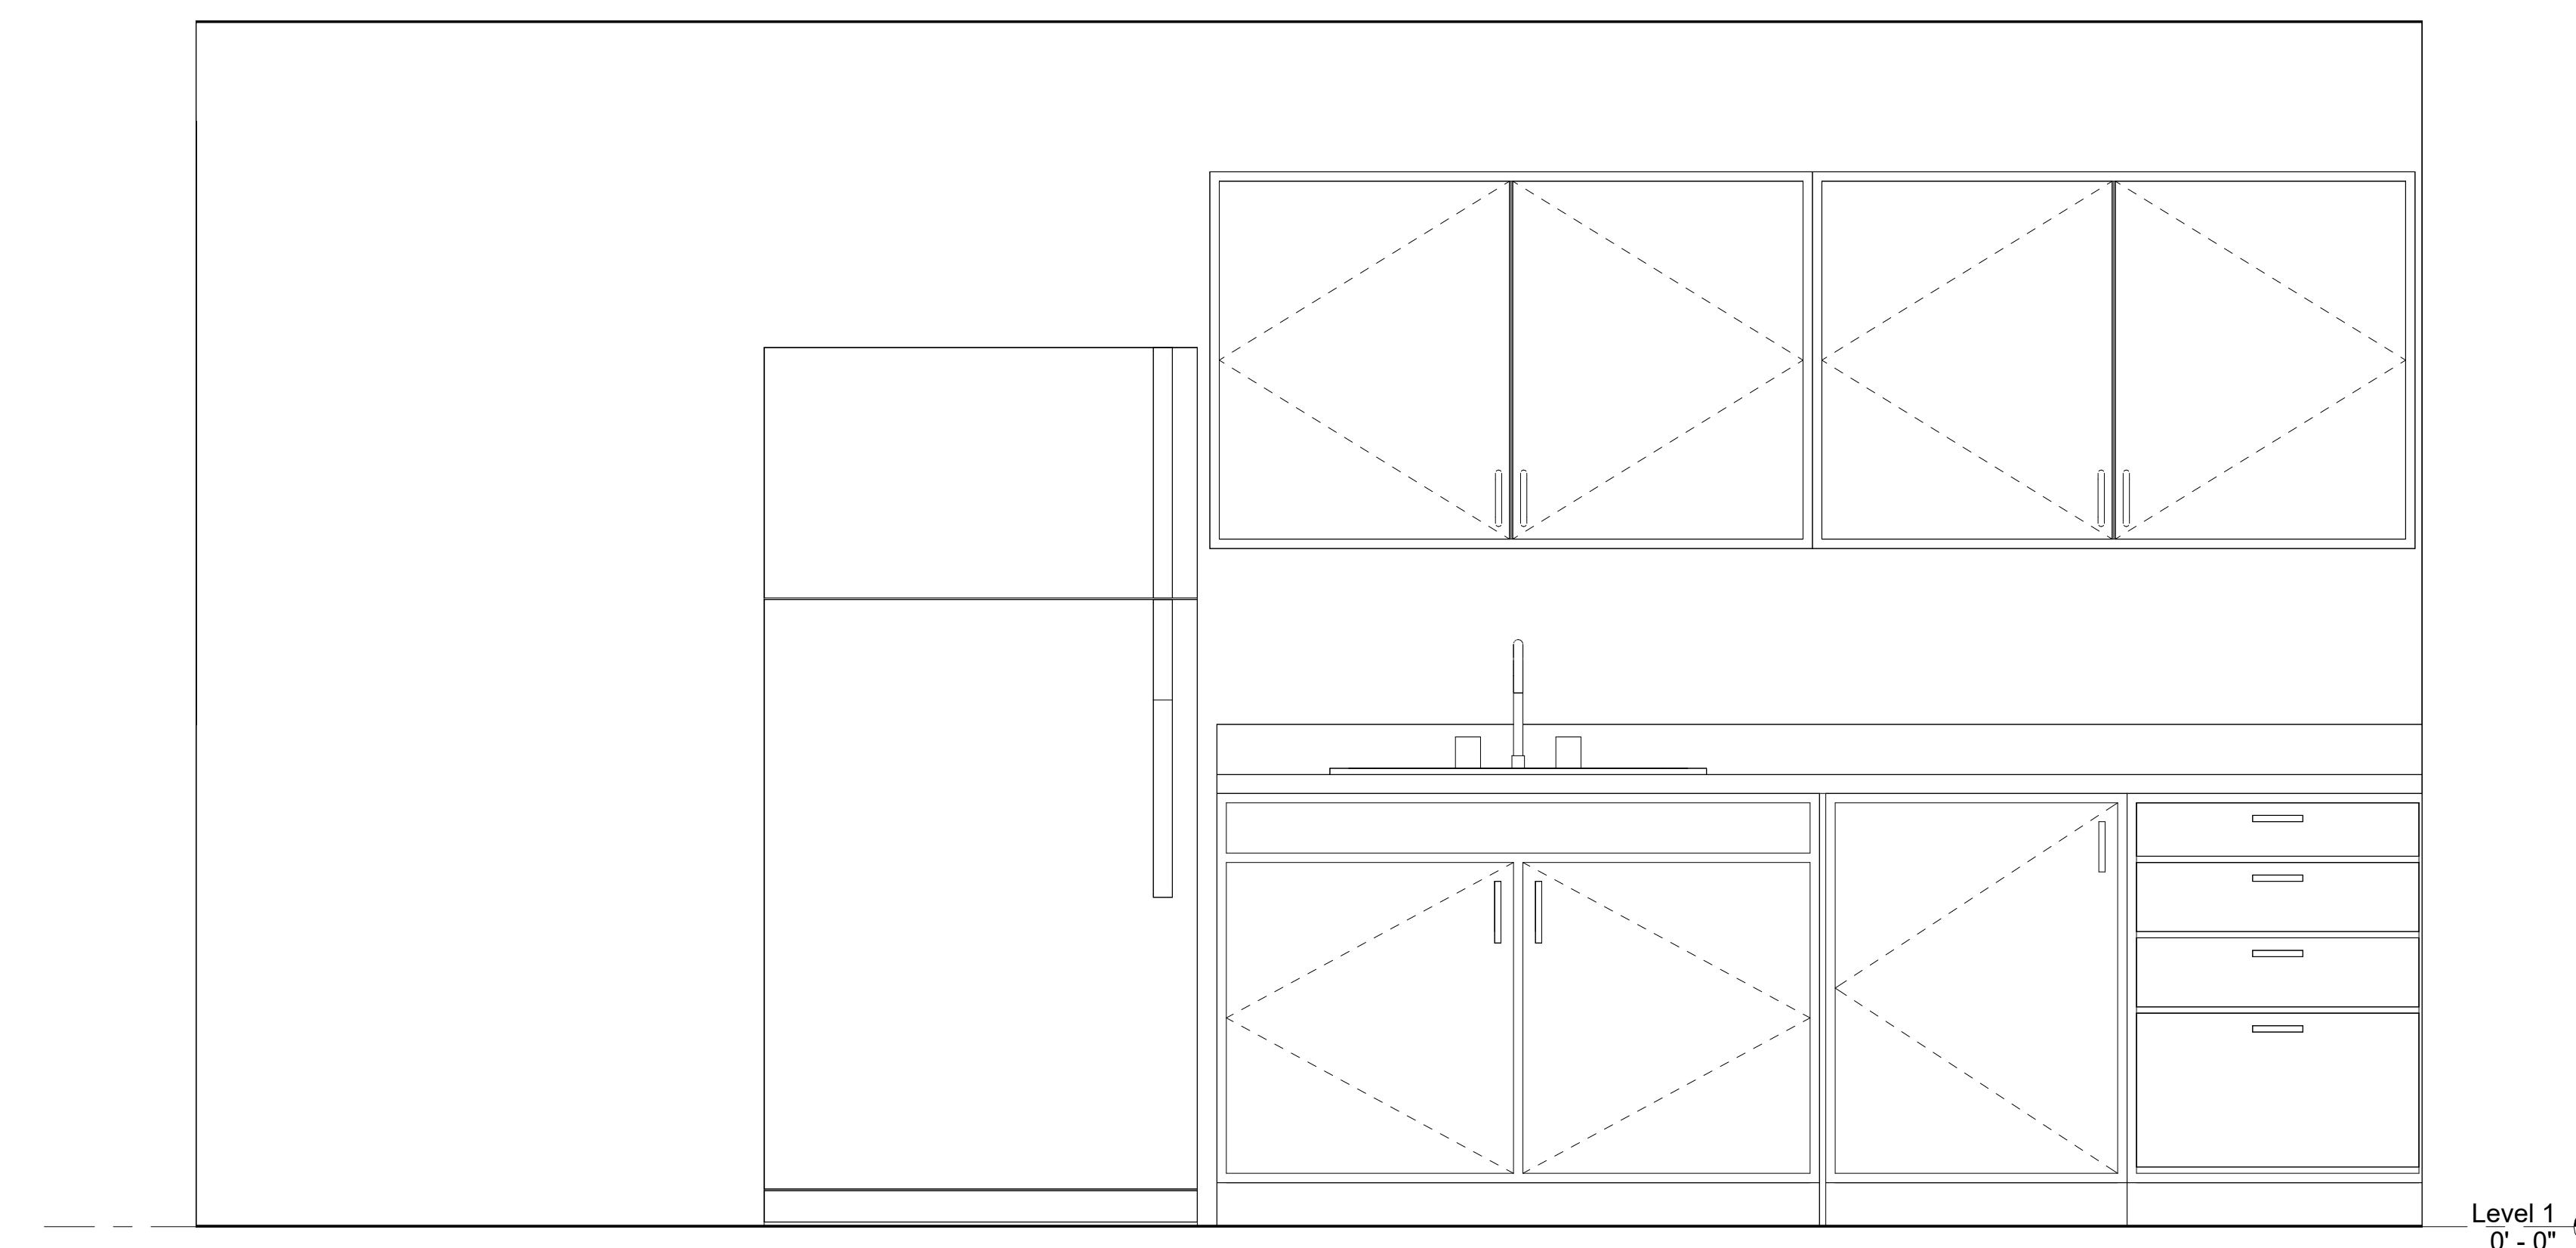

① Break Room East
1" = 1'-0"

[illegible]

T.H.E Developers

Harbor View Offices
Interior Elevations

Project Number	2026-001
----------------	----------

Date	June 3, 2026
------	--------------

Drawn By	Author
----------	--------

Checked By	Checker
------------	---------

1500


A500

A500	
Scale	1" = 1'-0"


Scale 1" = 1'-0"

6/6/2026 1:55:54 PM


Keynote Legend	
Key Value	Keynote Text
09 29 00.C1	1/2" Gypsum Wallboard

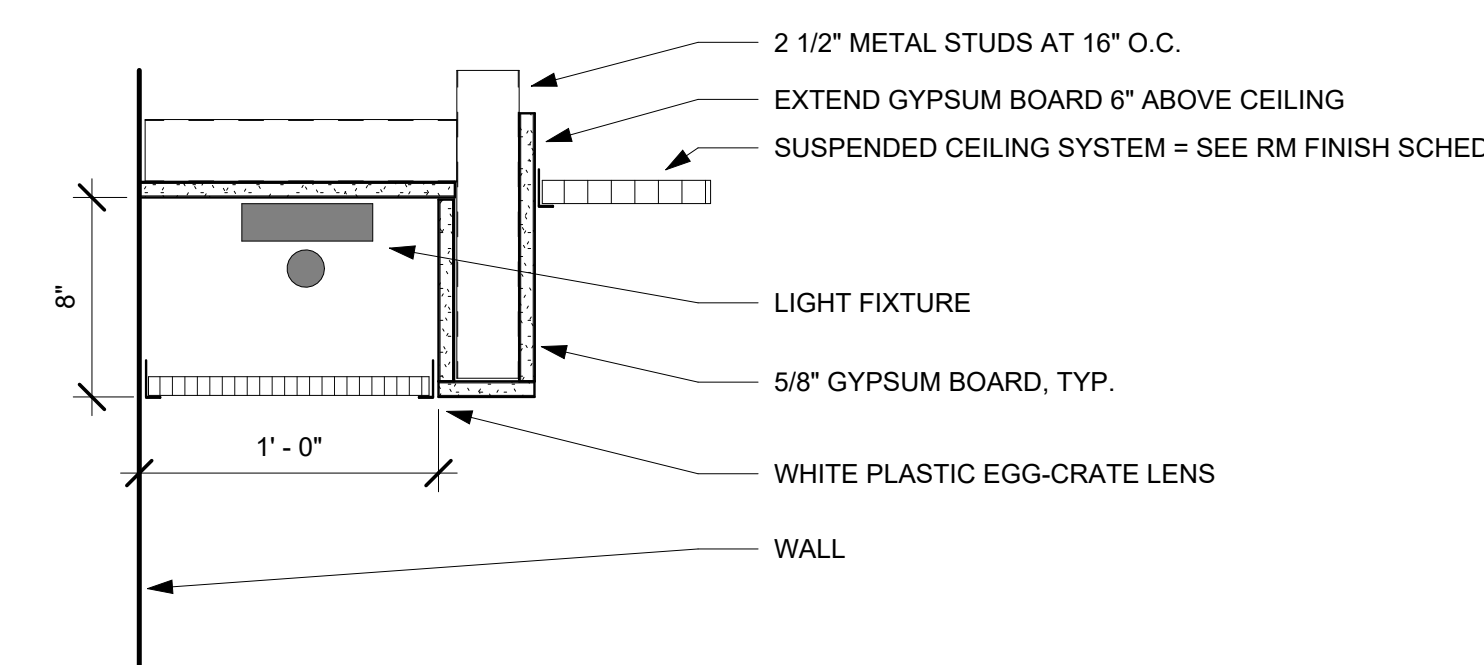


5 Toilet Room Ceiling Detail
1 1/2" = 1'-0"

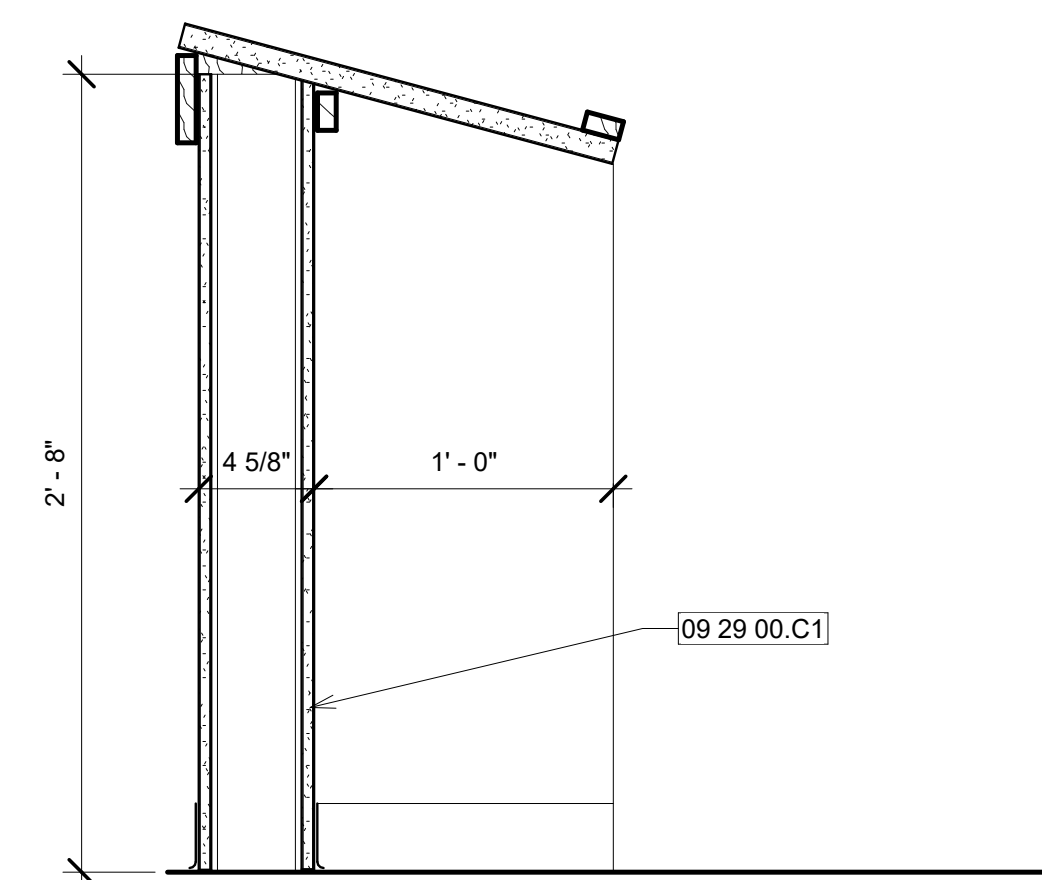


7 Fixed Student Desk - KEYNOTES
1 1/2" = 1'-0"

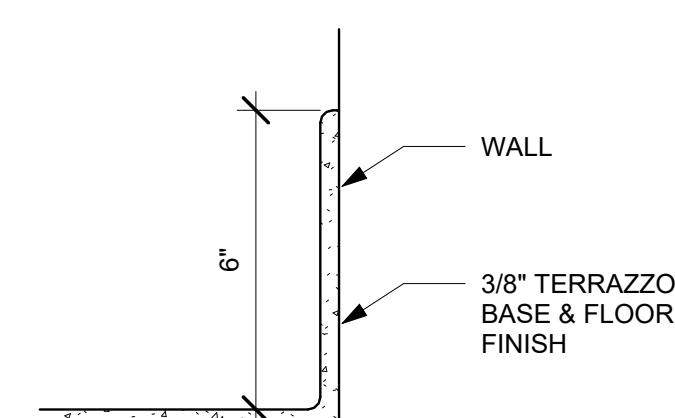


6 Terrazzo Base Detail
3" = 1'-0"

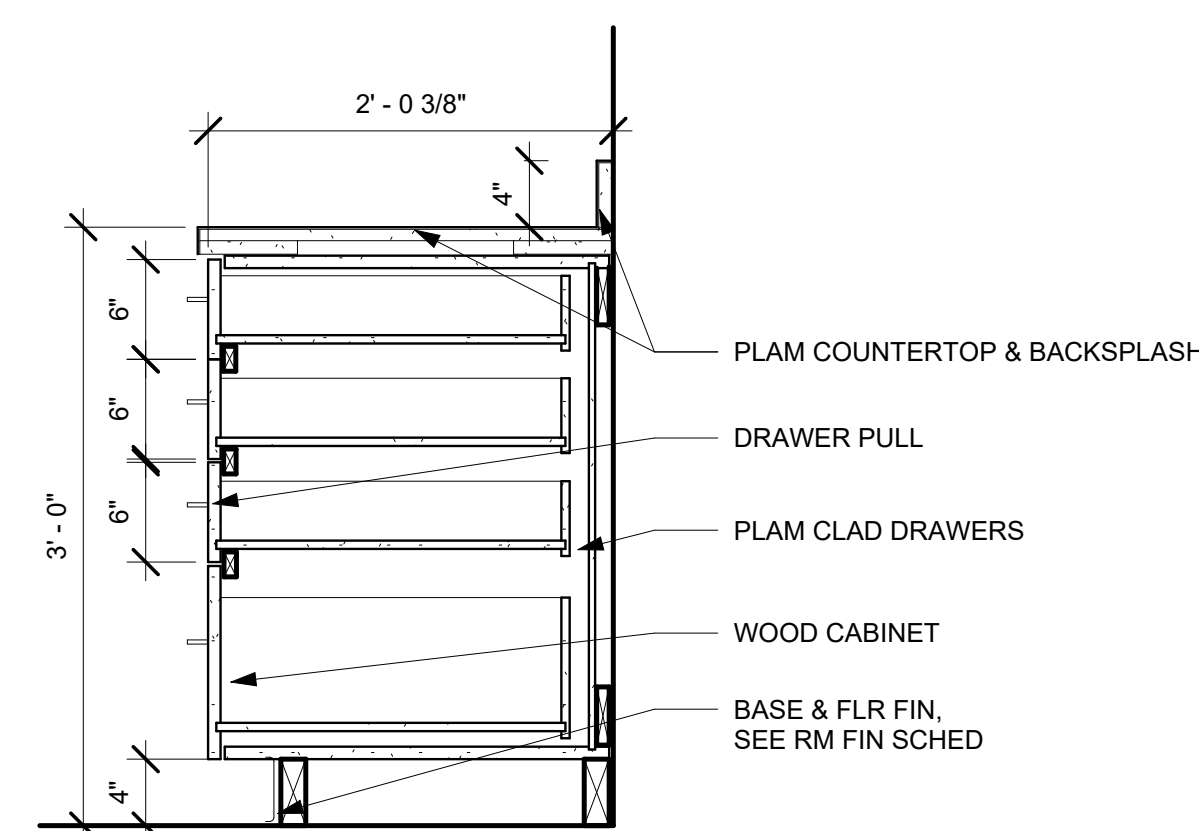


② Base Cabinet Detail - Drawers
1" = 1'-0"

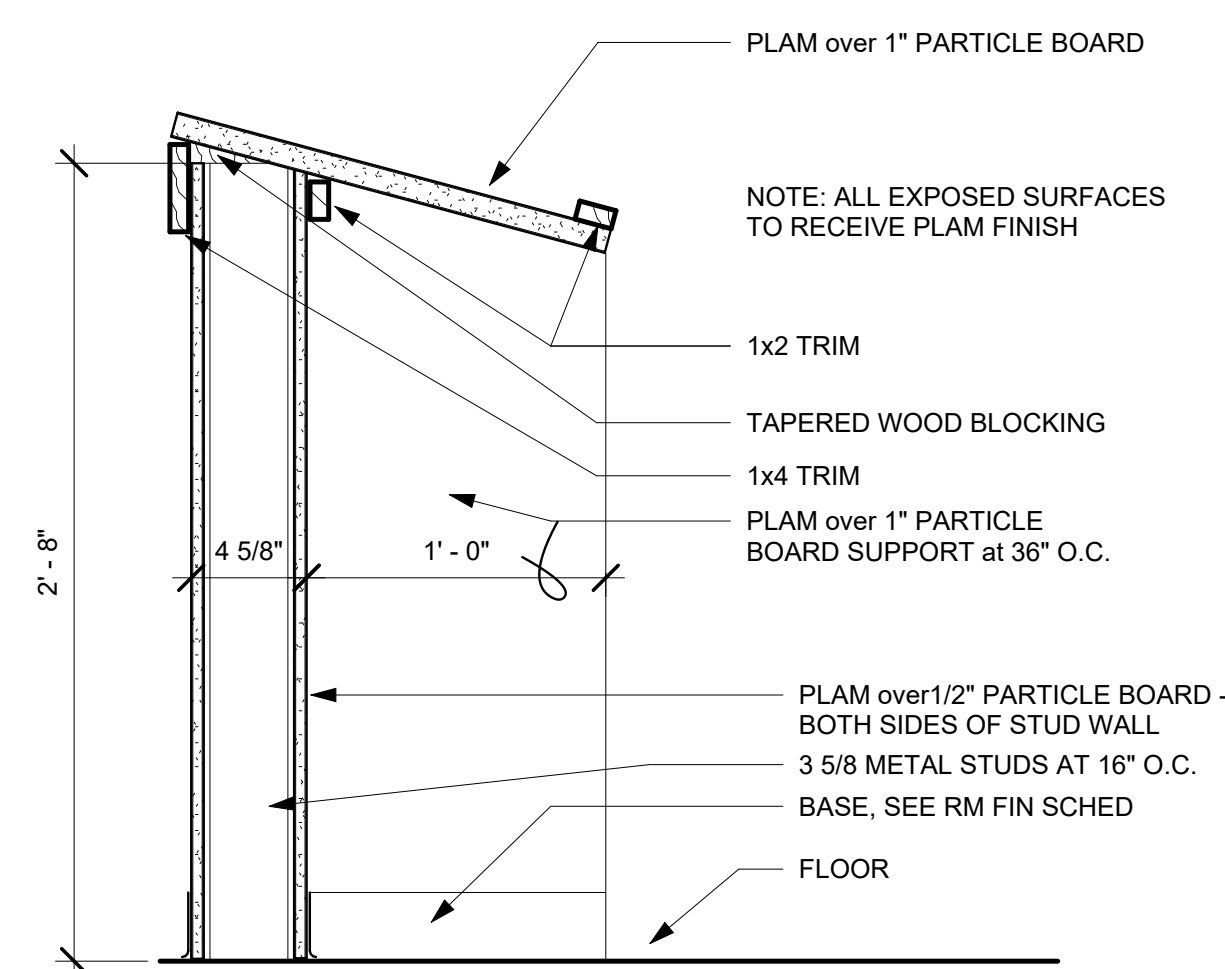

③ Fixed Student Desk
1 1/2" = 1'-0"

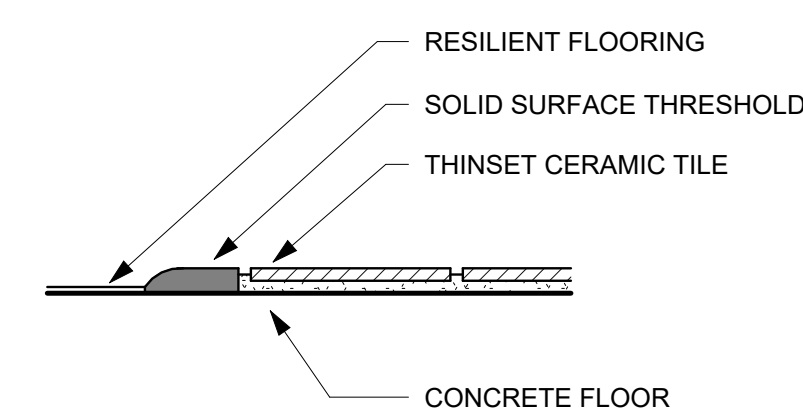

8 Floor Transition Detail
3" = 1'-0"

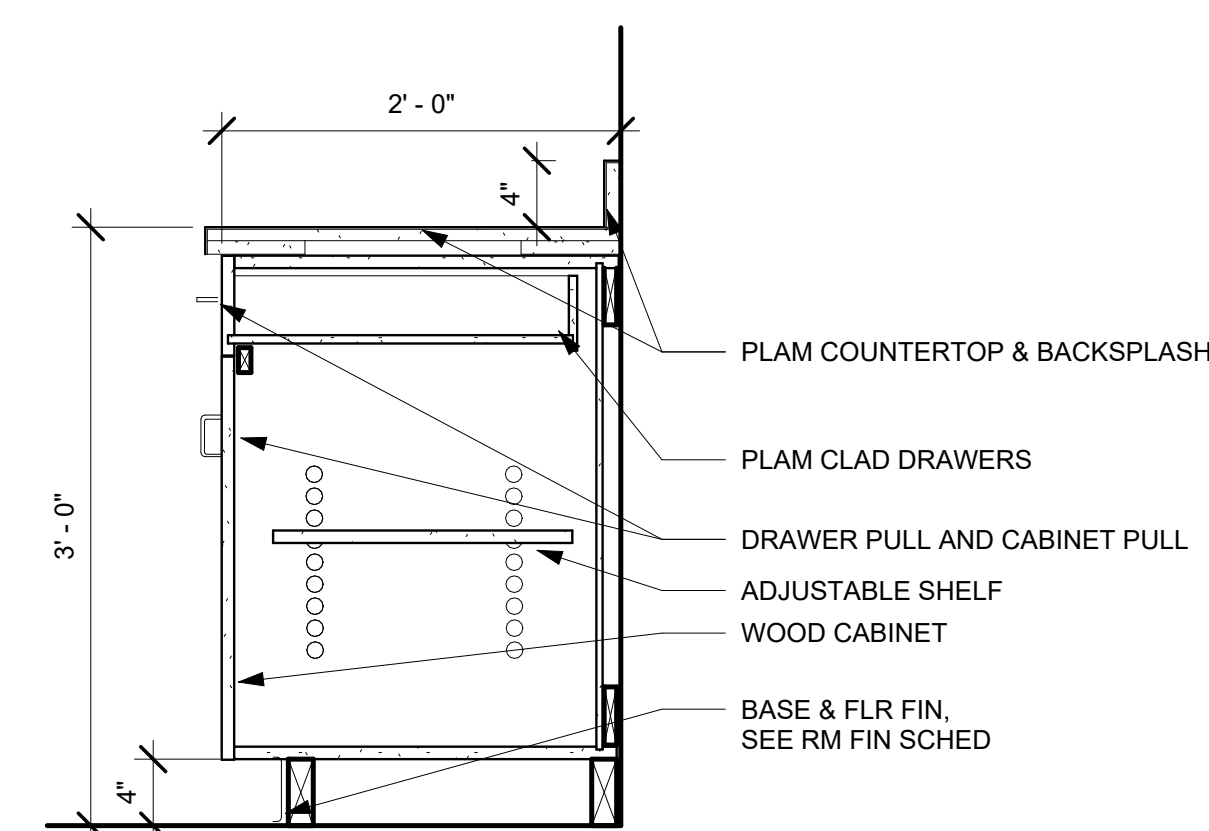

1 Base Cabinet Detail
1" = 1'-0"



www.autodesk.com/revit

Consultant
Address
Address
Address
Phone

Consultant
Address
Address
Address
Phone

Consultant
Address
Address
Address
Phone

Consultant
Address
Address
Address
Phone

Consultant
Address
Address
Address
Phone

[illegible]

T.H.E Developers

Harbor View Offices

Details

Project Number	2026-001
----------------	----------

Date	June 3, 2026
------	--------------

Drawn By	Author
----------	--------

Checked By	Checker
------------	---------

A600

Scale	As indicated
-------	--------------



www.autodesk.com/revit

Consultant
Address
Address
Address
Phone


Consultant	Address	Address	Address	Phone
------------	---------	---------	---------	-------

Consultant	Address	Address	Address	Phone
------------	---------	---------	---------	-------

Consultant	Address	Address	Address	Phone
------------	---------	---------	---------	-------

Consultant
Address
Address
Address
Phone

1 Atrium Roof Option 2

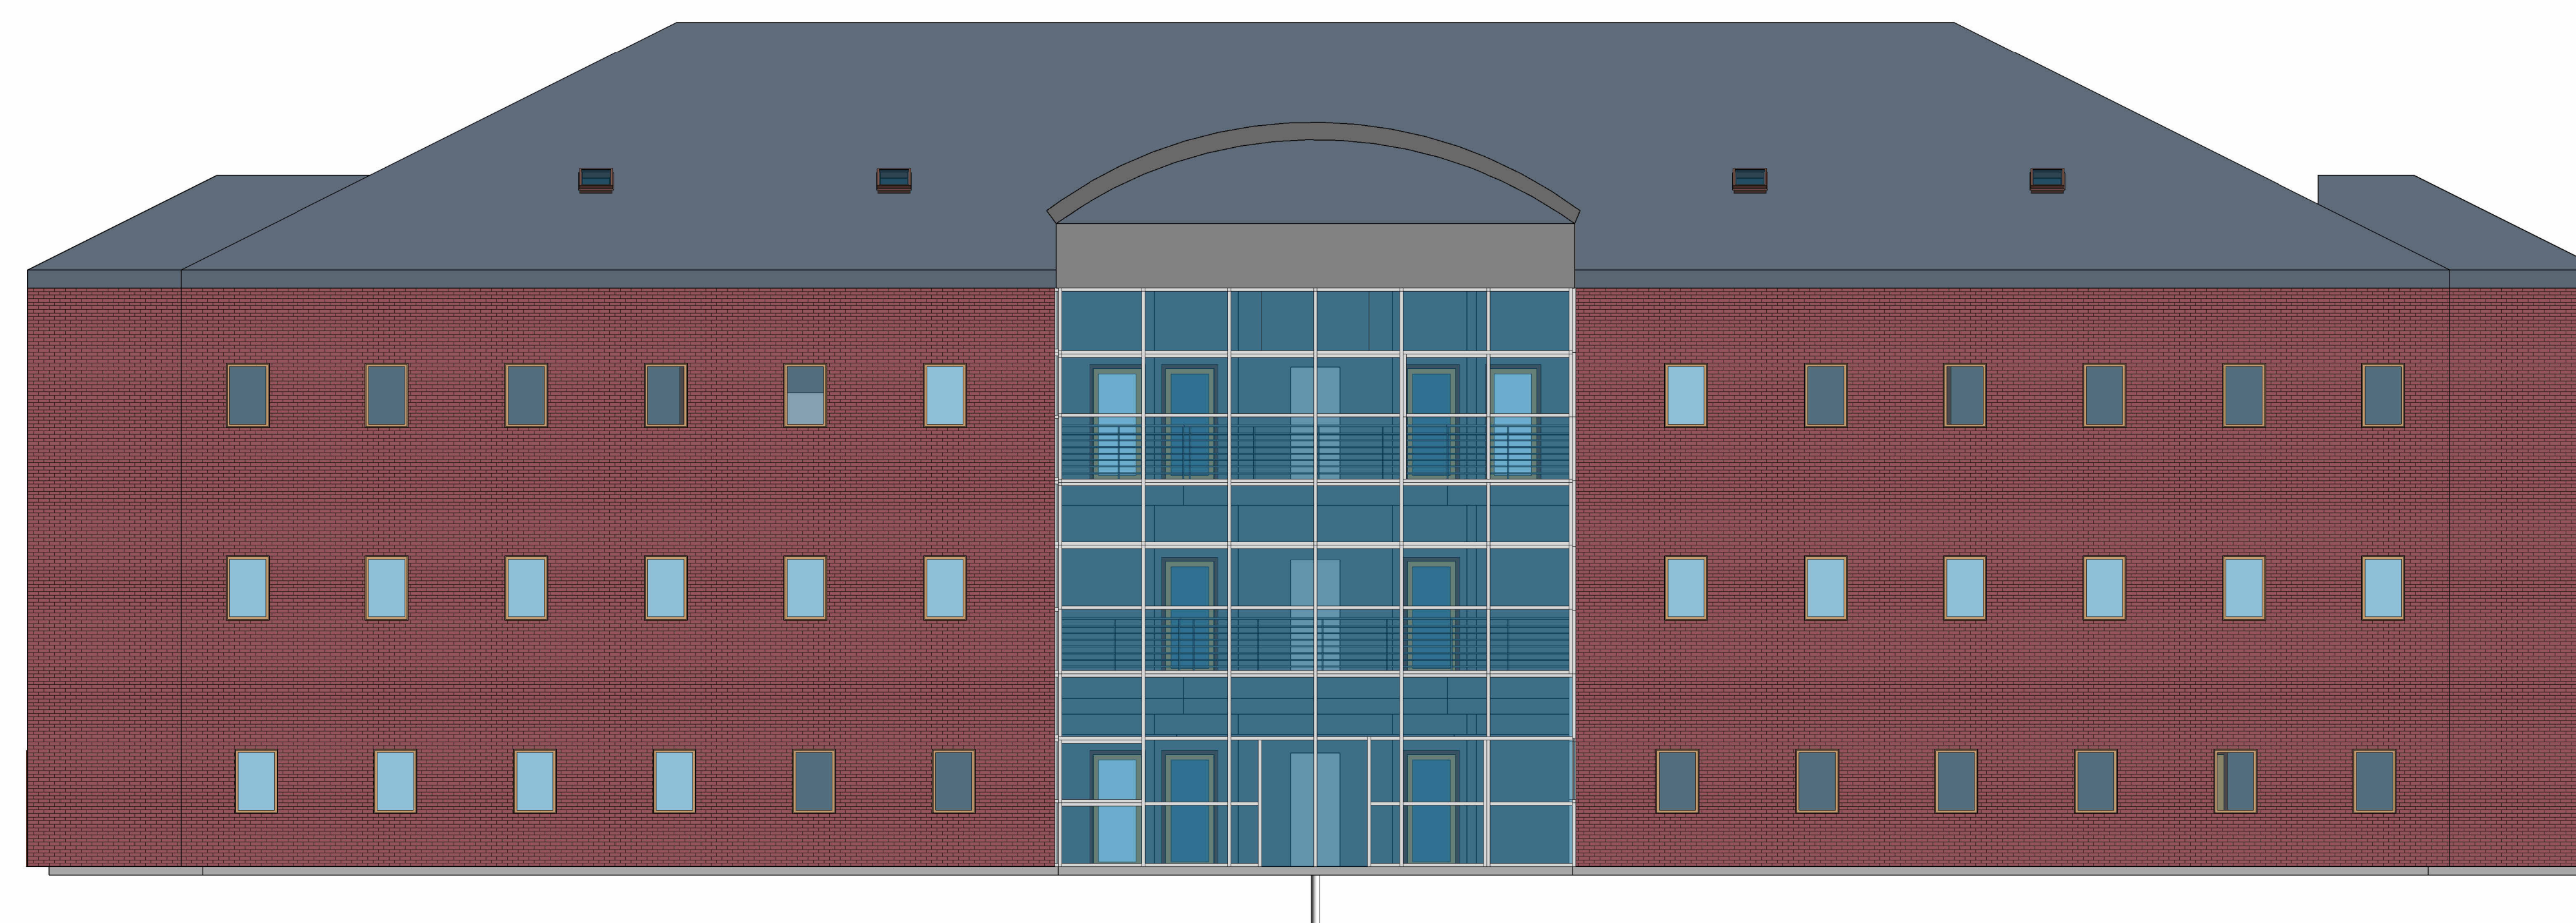

2 Curtainwall Option 2

[illegible]

T.H.E Developers

Harbor View Offices

Design Options

Project Number	2026-001
----------------	----------

Date	June 3, 2026
------	--------------

Drawn By	Author
----------	--------

Checked By	Checker
------------	---------

A900

Scale

01/07/2020 1:30:02 PM