




Consultant
Address
Address
Address
Phone

[illegible]

Level 1 Floor Plan

Project Number	2026-001
Date	June 3, 2026
Drawn By	A Knodel
Checked By	A Knodel

Scale	1/8" = 1'-0"
-------	--------------

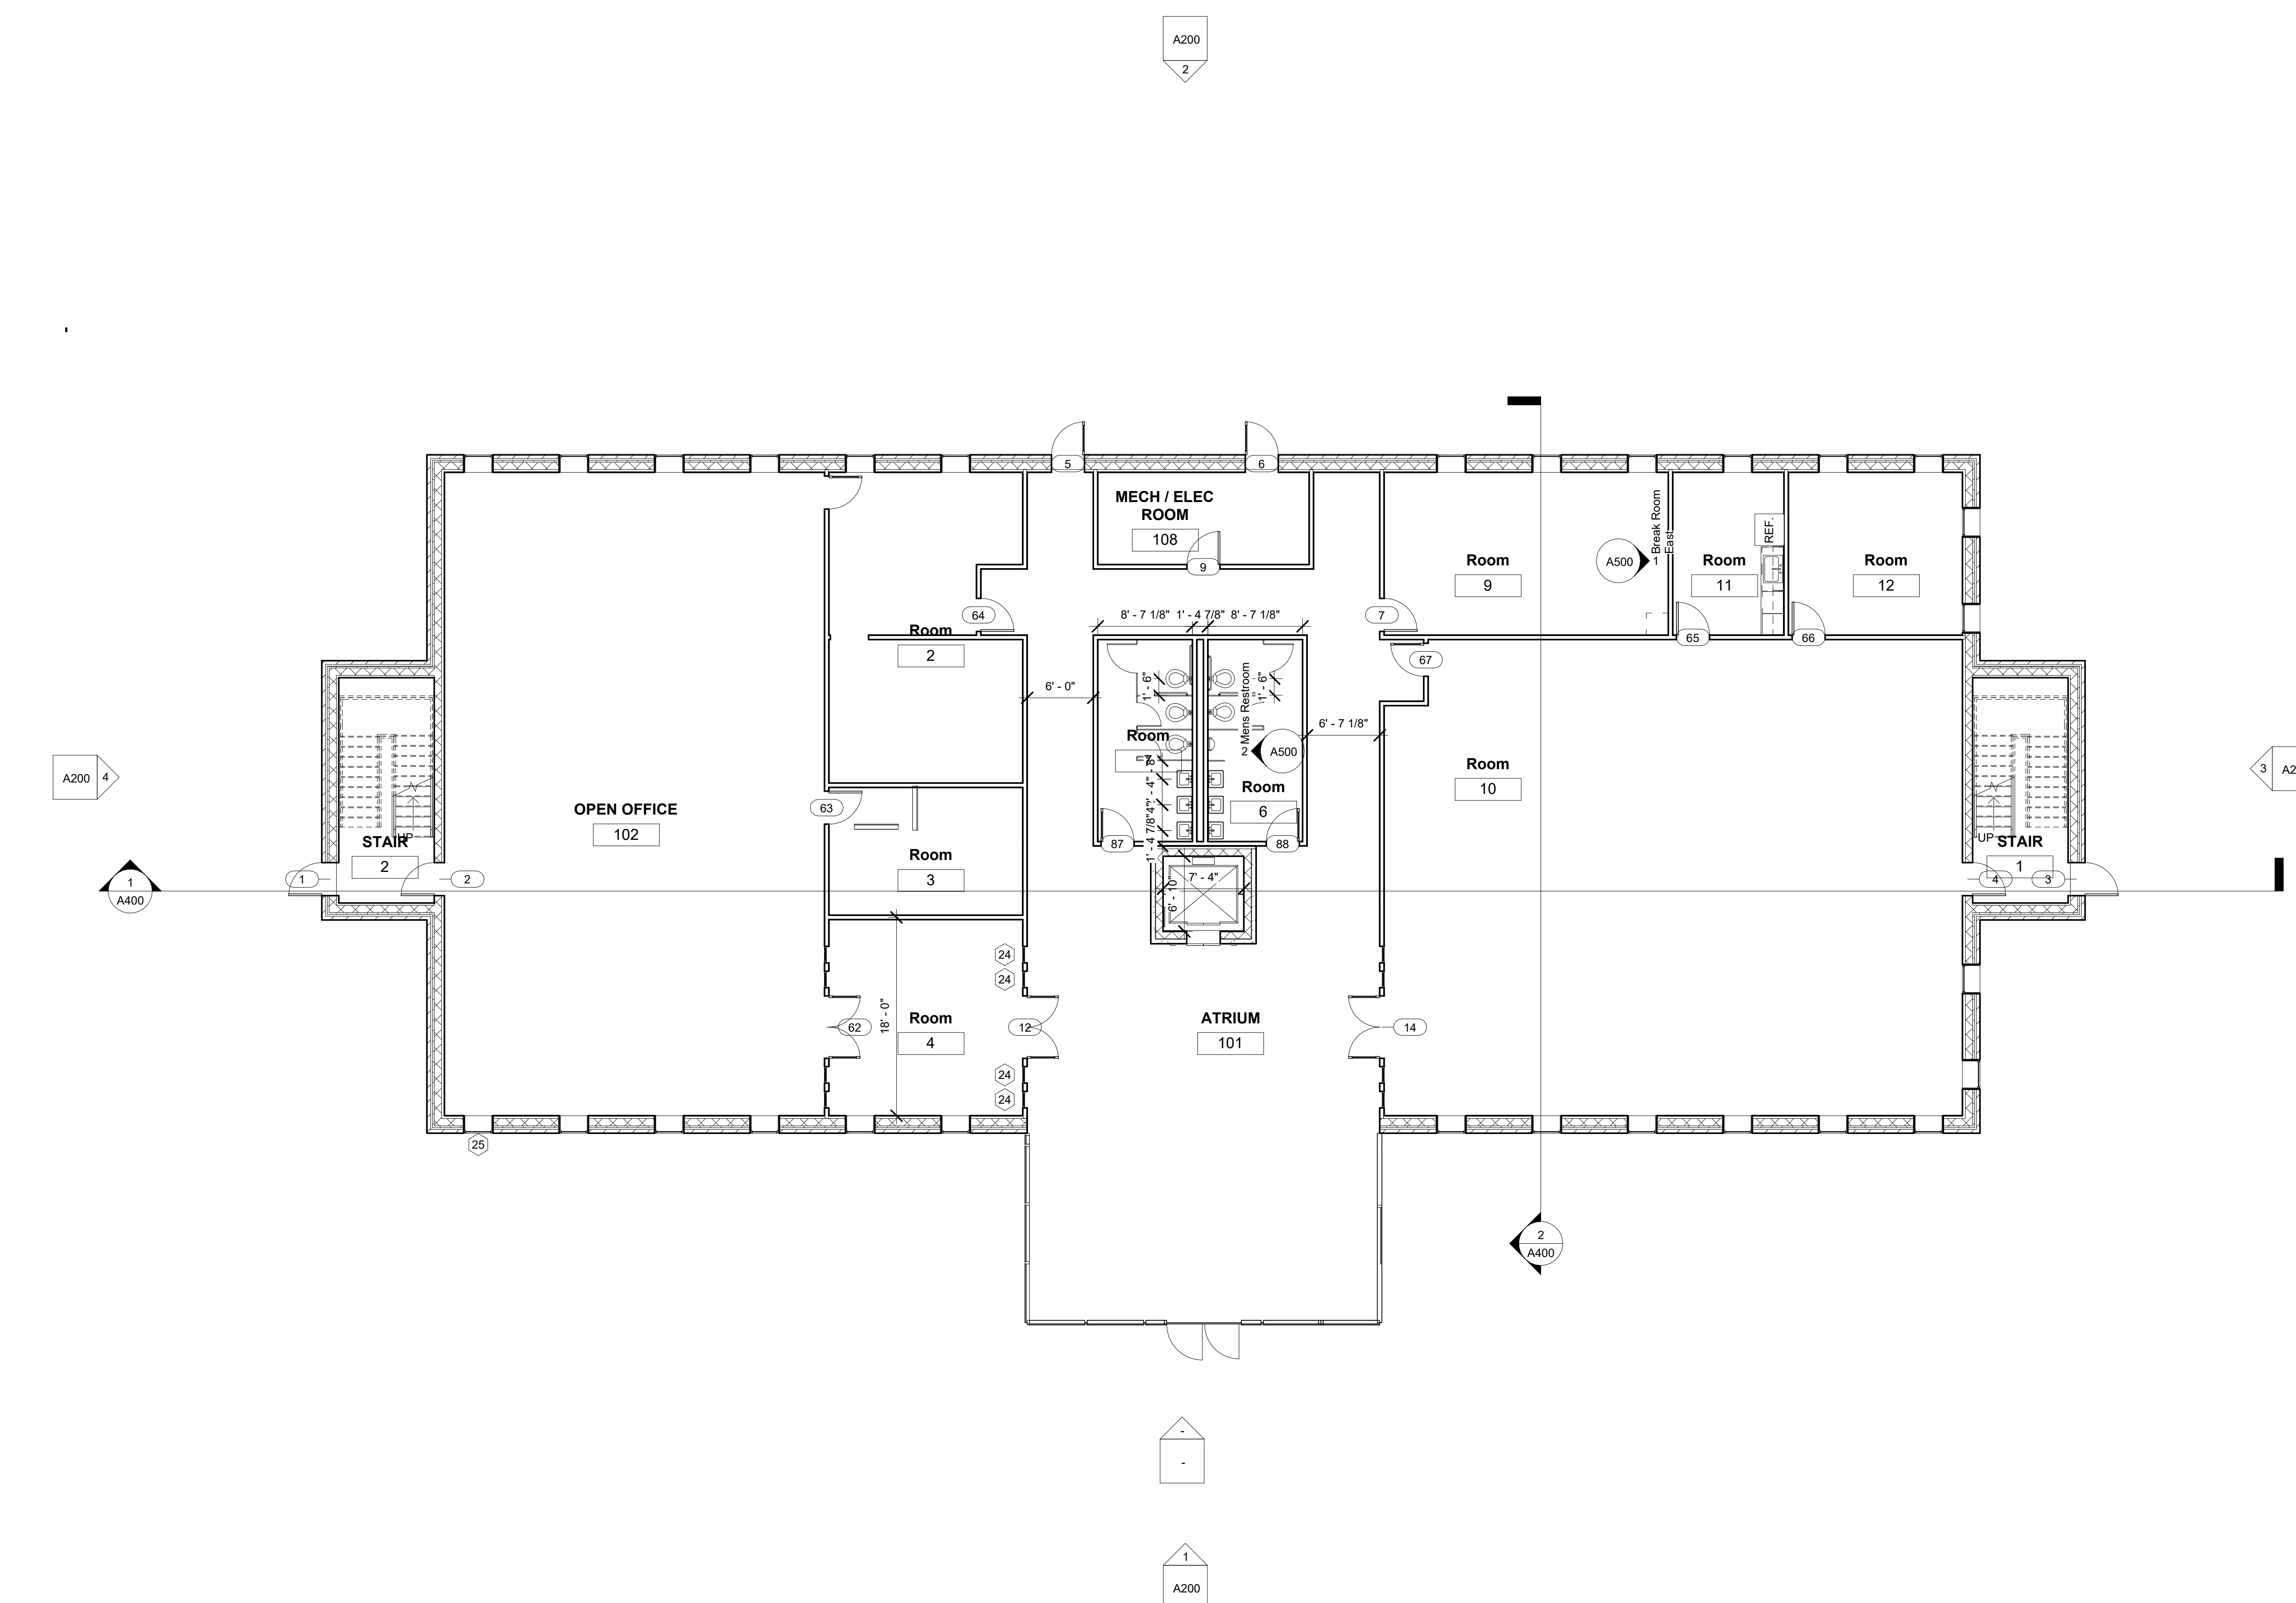

① Level 1
1/8" = 1'-0"



www.autodesk.com/revit

Consultant
Address
Address
Address
Phone

Consultant
Address
Address
Address
Phone

Consultant
Address
Address
Address
Phone

Consultant
Address
Address
Address
Phone

Consultant
Address
Address
Address
Phone

[illegible]

T.H.E Developers

Harbor View Offices

Level 2 Floor Plan


Project Number	2026-001
----------------	----------

Date	June 3, 2026
------	--------------

Drawn By	Author
----------	--------

A102

Scale	1/8" = 1'-0"
-------	--------------

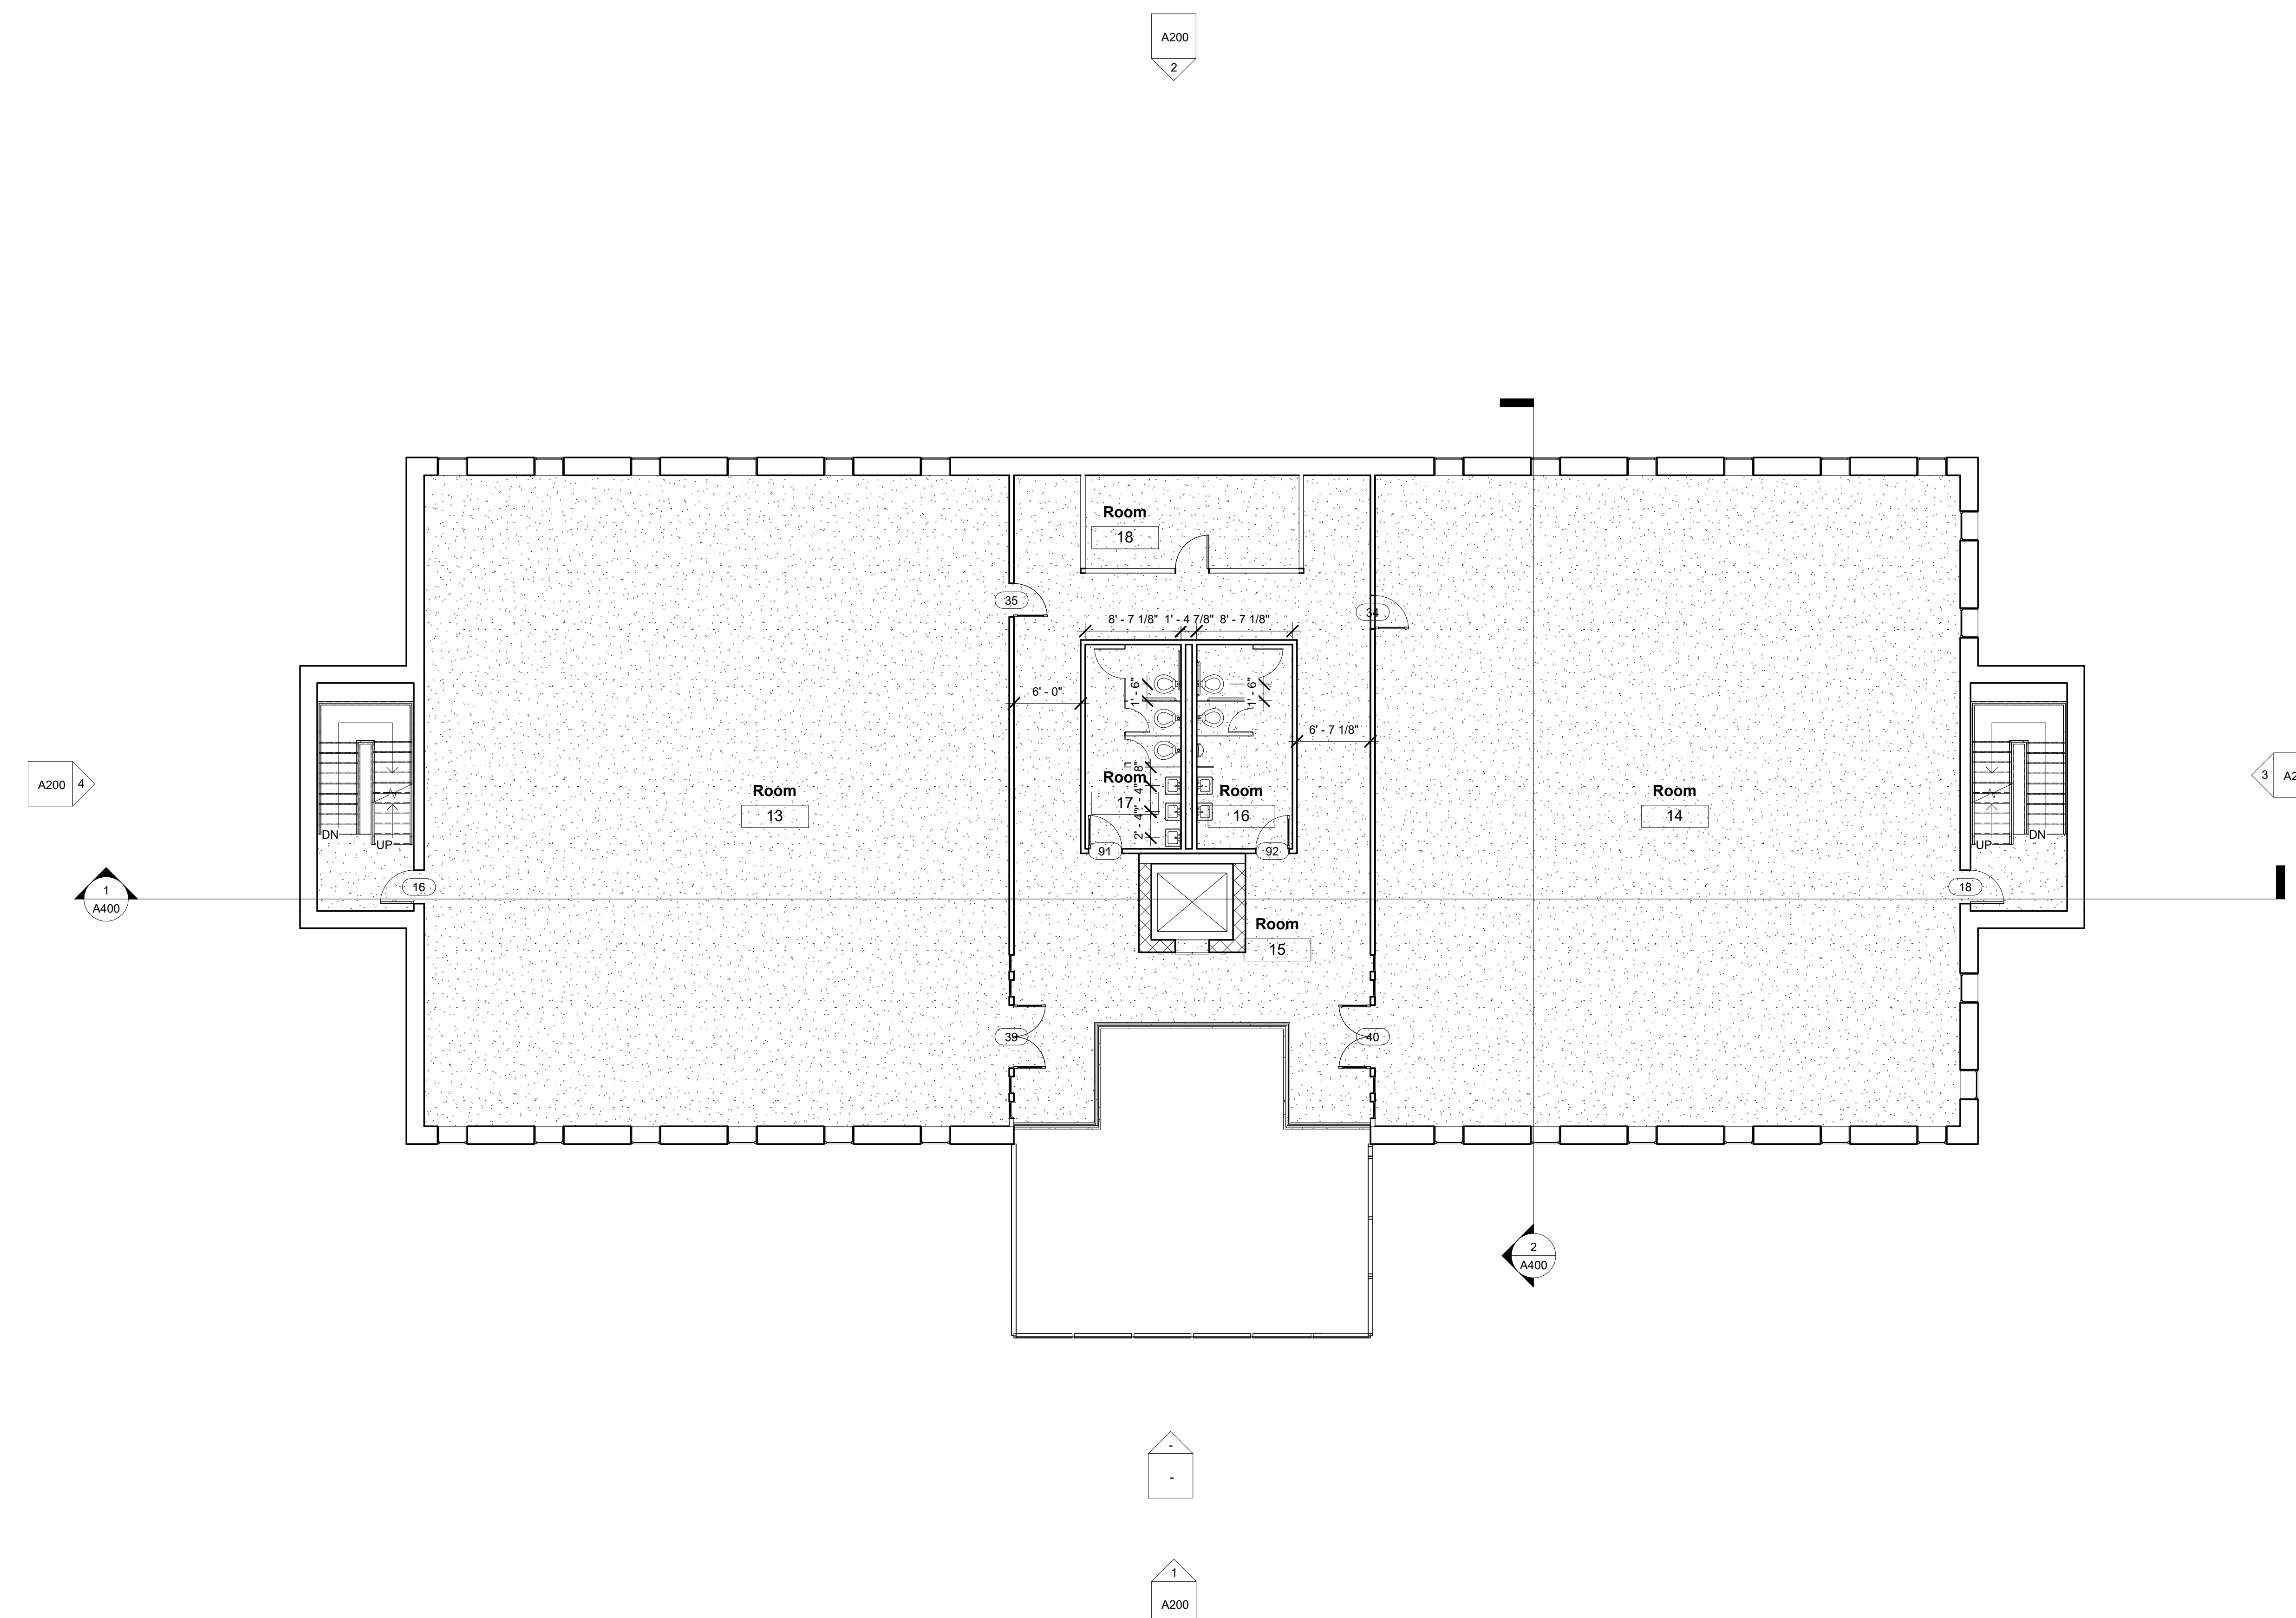

① Level 2
1/8" = 1'-0"

8/2026 5:25:48 PM




Consultant
Address
Address
Address
Phone

[illegible]

Project Number	2026-001
Date	June 3, 2026
Drawn By	Author
Checked By	Checker

Scale	1/8" = 1'-0"
-------	--------------

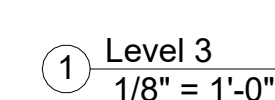



www.autodesk.com/revit


Consultant
Address
Address
Address
Phone

Consultant
Address
Address
Address
Phone

Consultant
Address
Address
Address
Phone

Consultant
Address
Address
Address
Phone

Consultant
Address
Address
Address
Phone

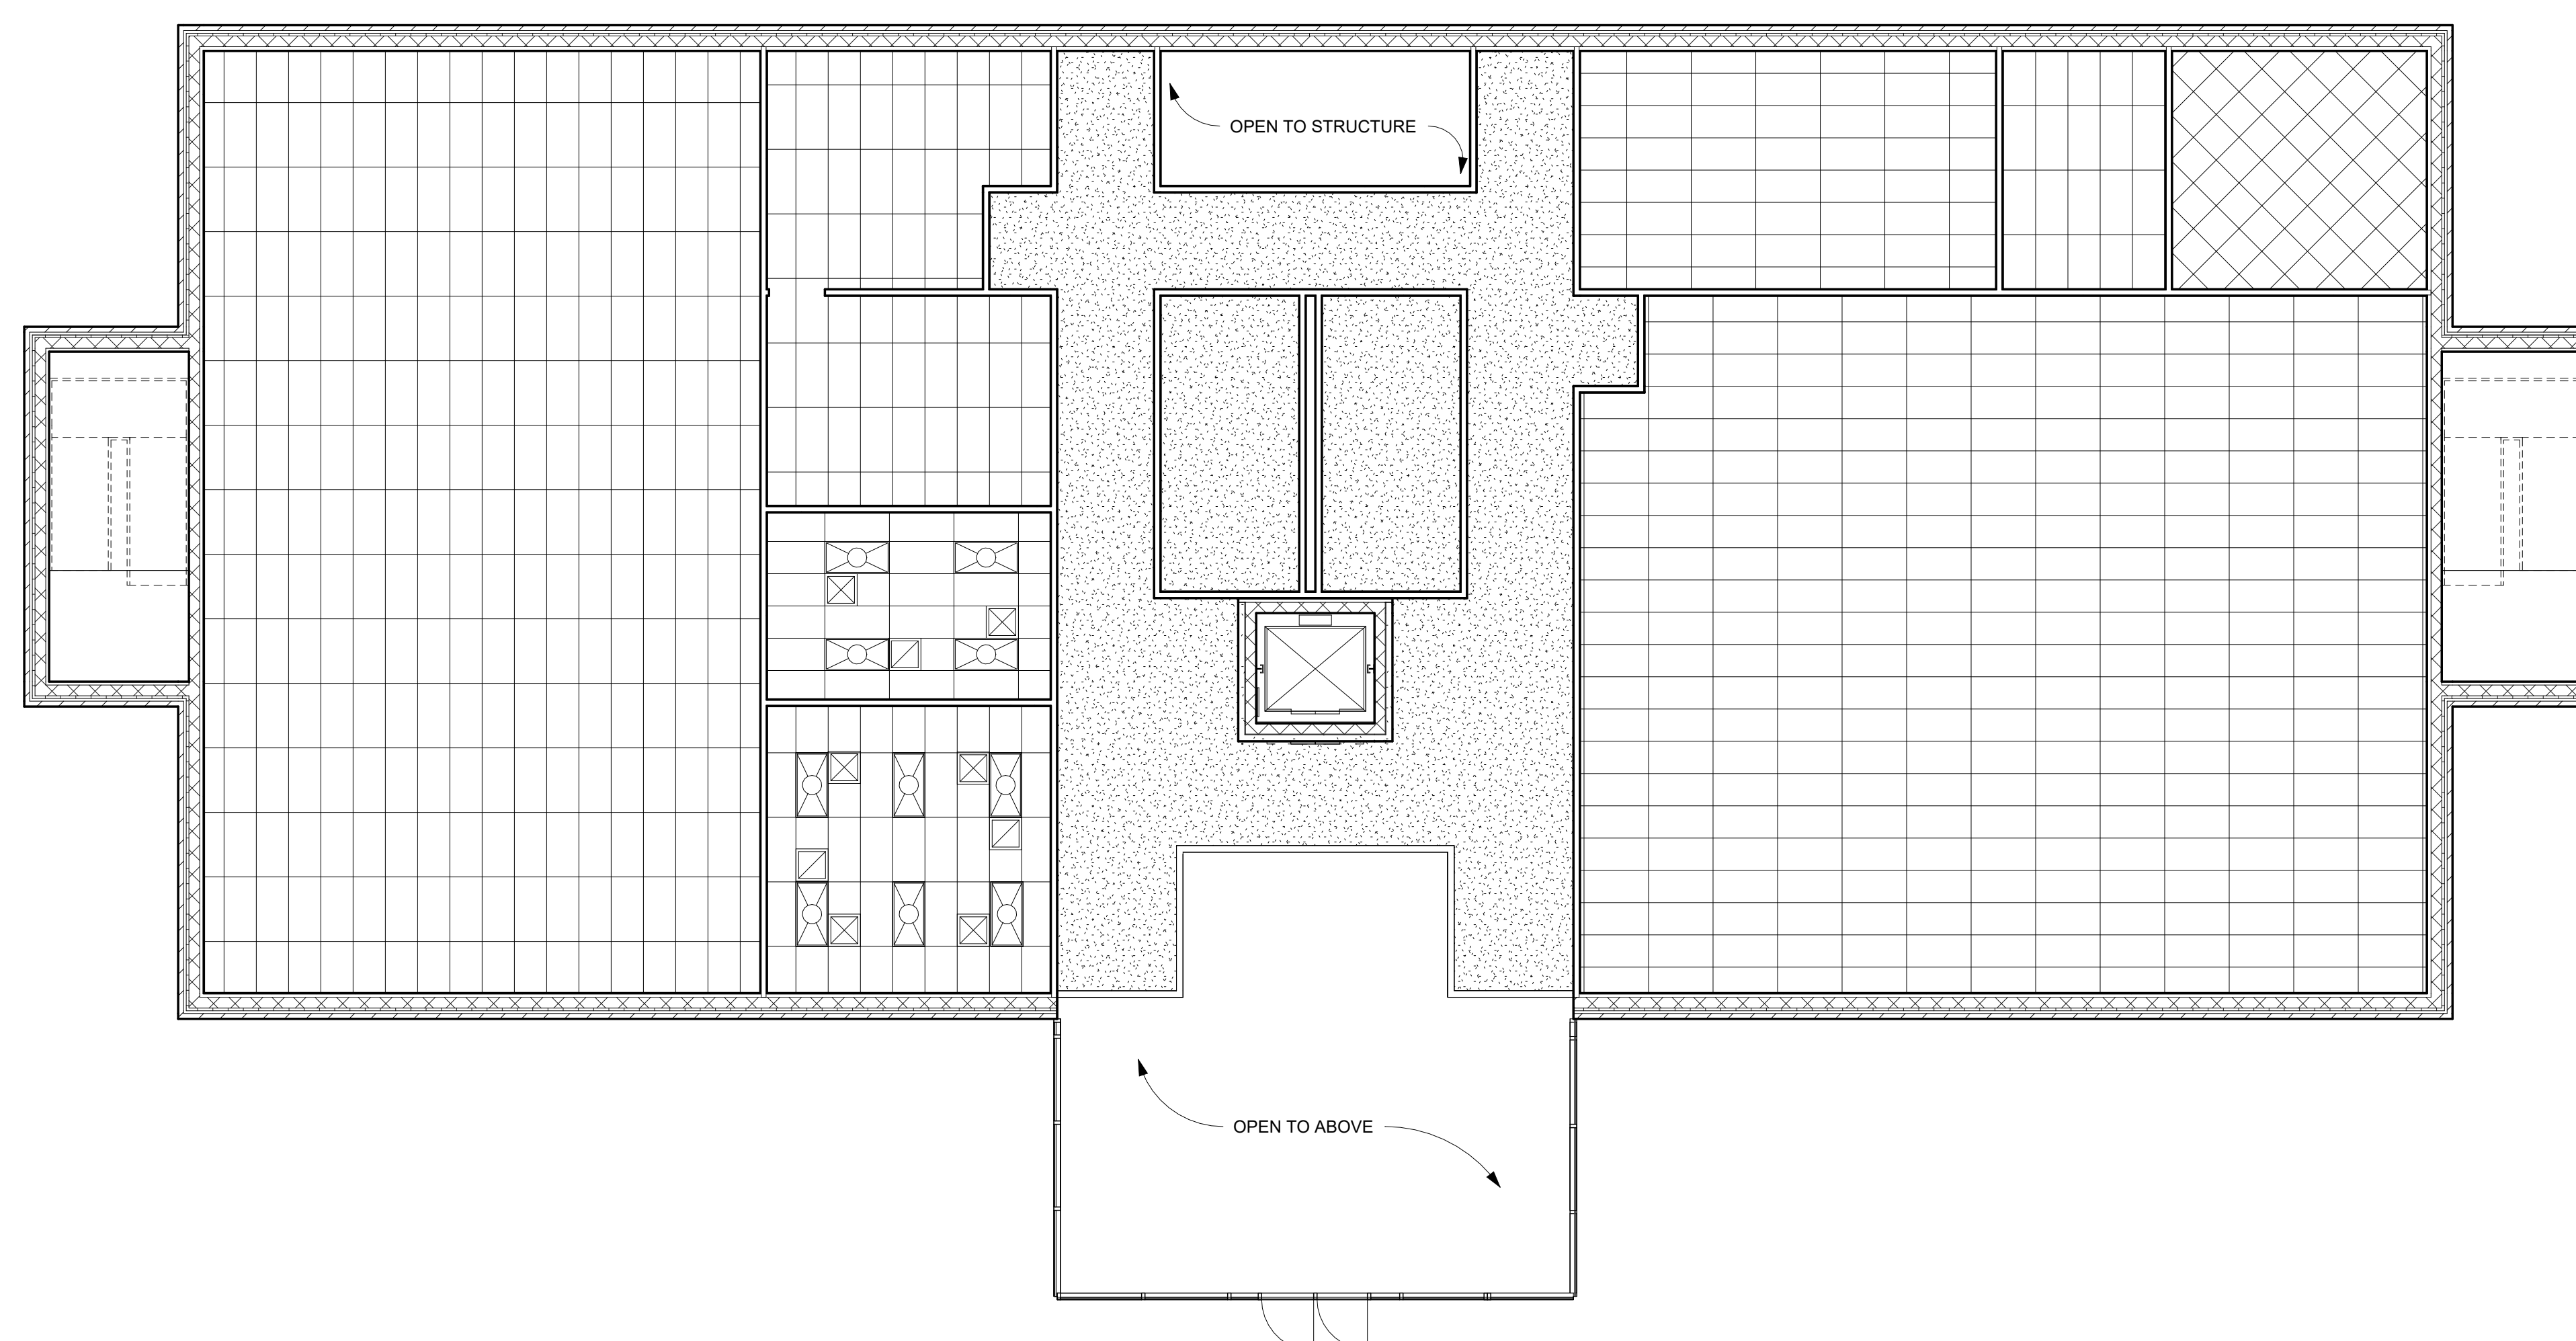

① Level 1
1/8" = 1'-0"

[illegible]

T.H.E Developers

Harbor View Offices

Level 1 Reflected Ceiling

Project Number	2026-001
----------------	----------

Date	June 3, 2026
------	--------------

Drawn By	Author
----------	--------

Checked By	Checker
------------	---------

A111

Scale	1/8" = 1'-0"
-------	--------------



www.autodesk.com/revit

Consultant
Address
Address
Address
Phone

Consultant
Address
Address
Address
Phone

Consultant
Address
Address
Address
Phone

Consultant
Address
Address
Address
Phone

Consultant
Address
Address
Address
Phone

[illegible]

T.H.E Developers

Harbor View Offices

Level 2 Reflected Ceiling

Project Number	2026-001
----------------	----------

Date	June 3, 2026
------	--------------


Drawn By	Author
----------	--------

Checked By	Checker
------------	---------

A112

Scale	1/8" = 1'-0"
-------	--------------

① Level 2
1/8" = 1'-0"

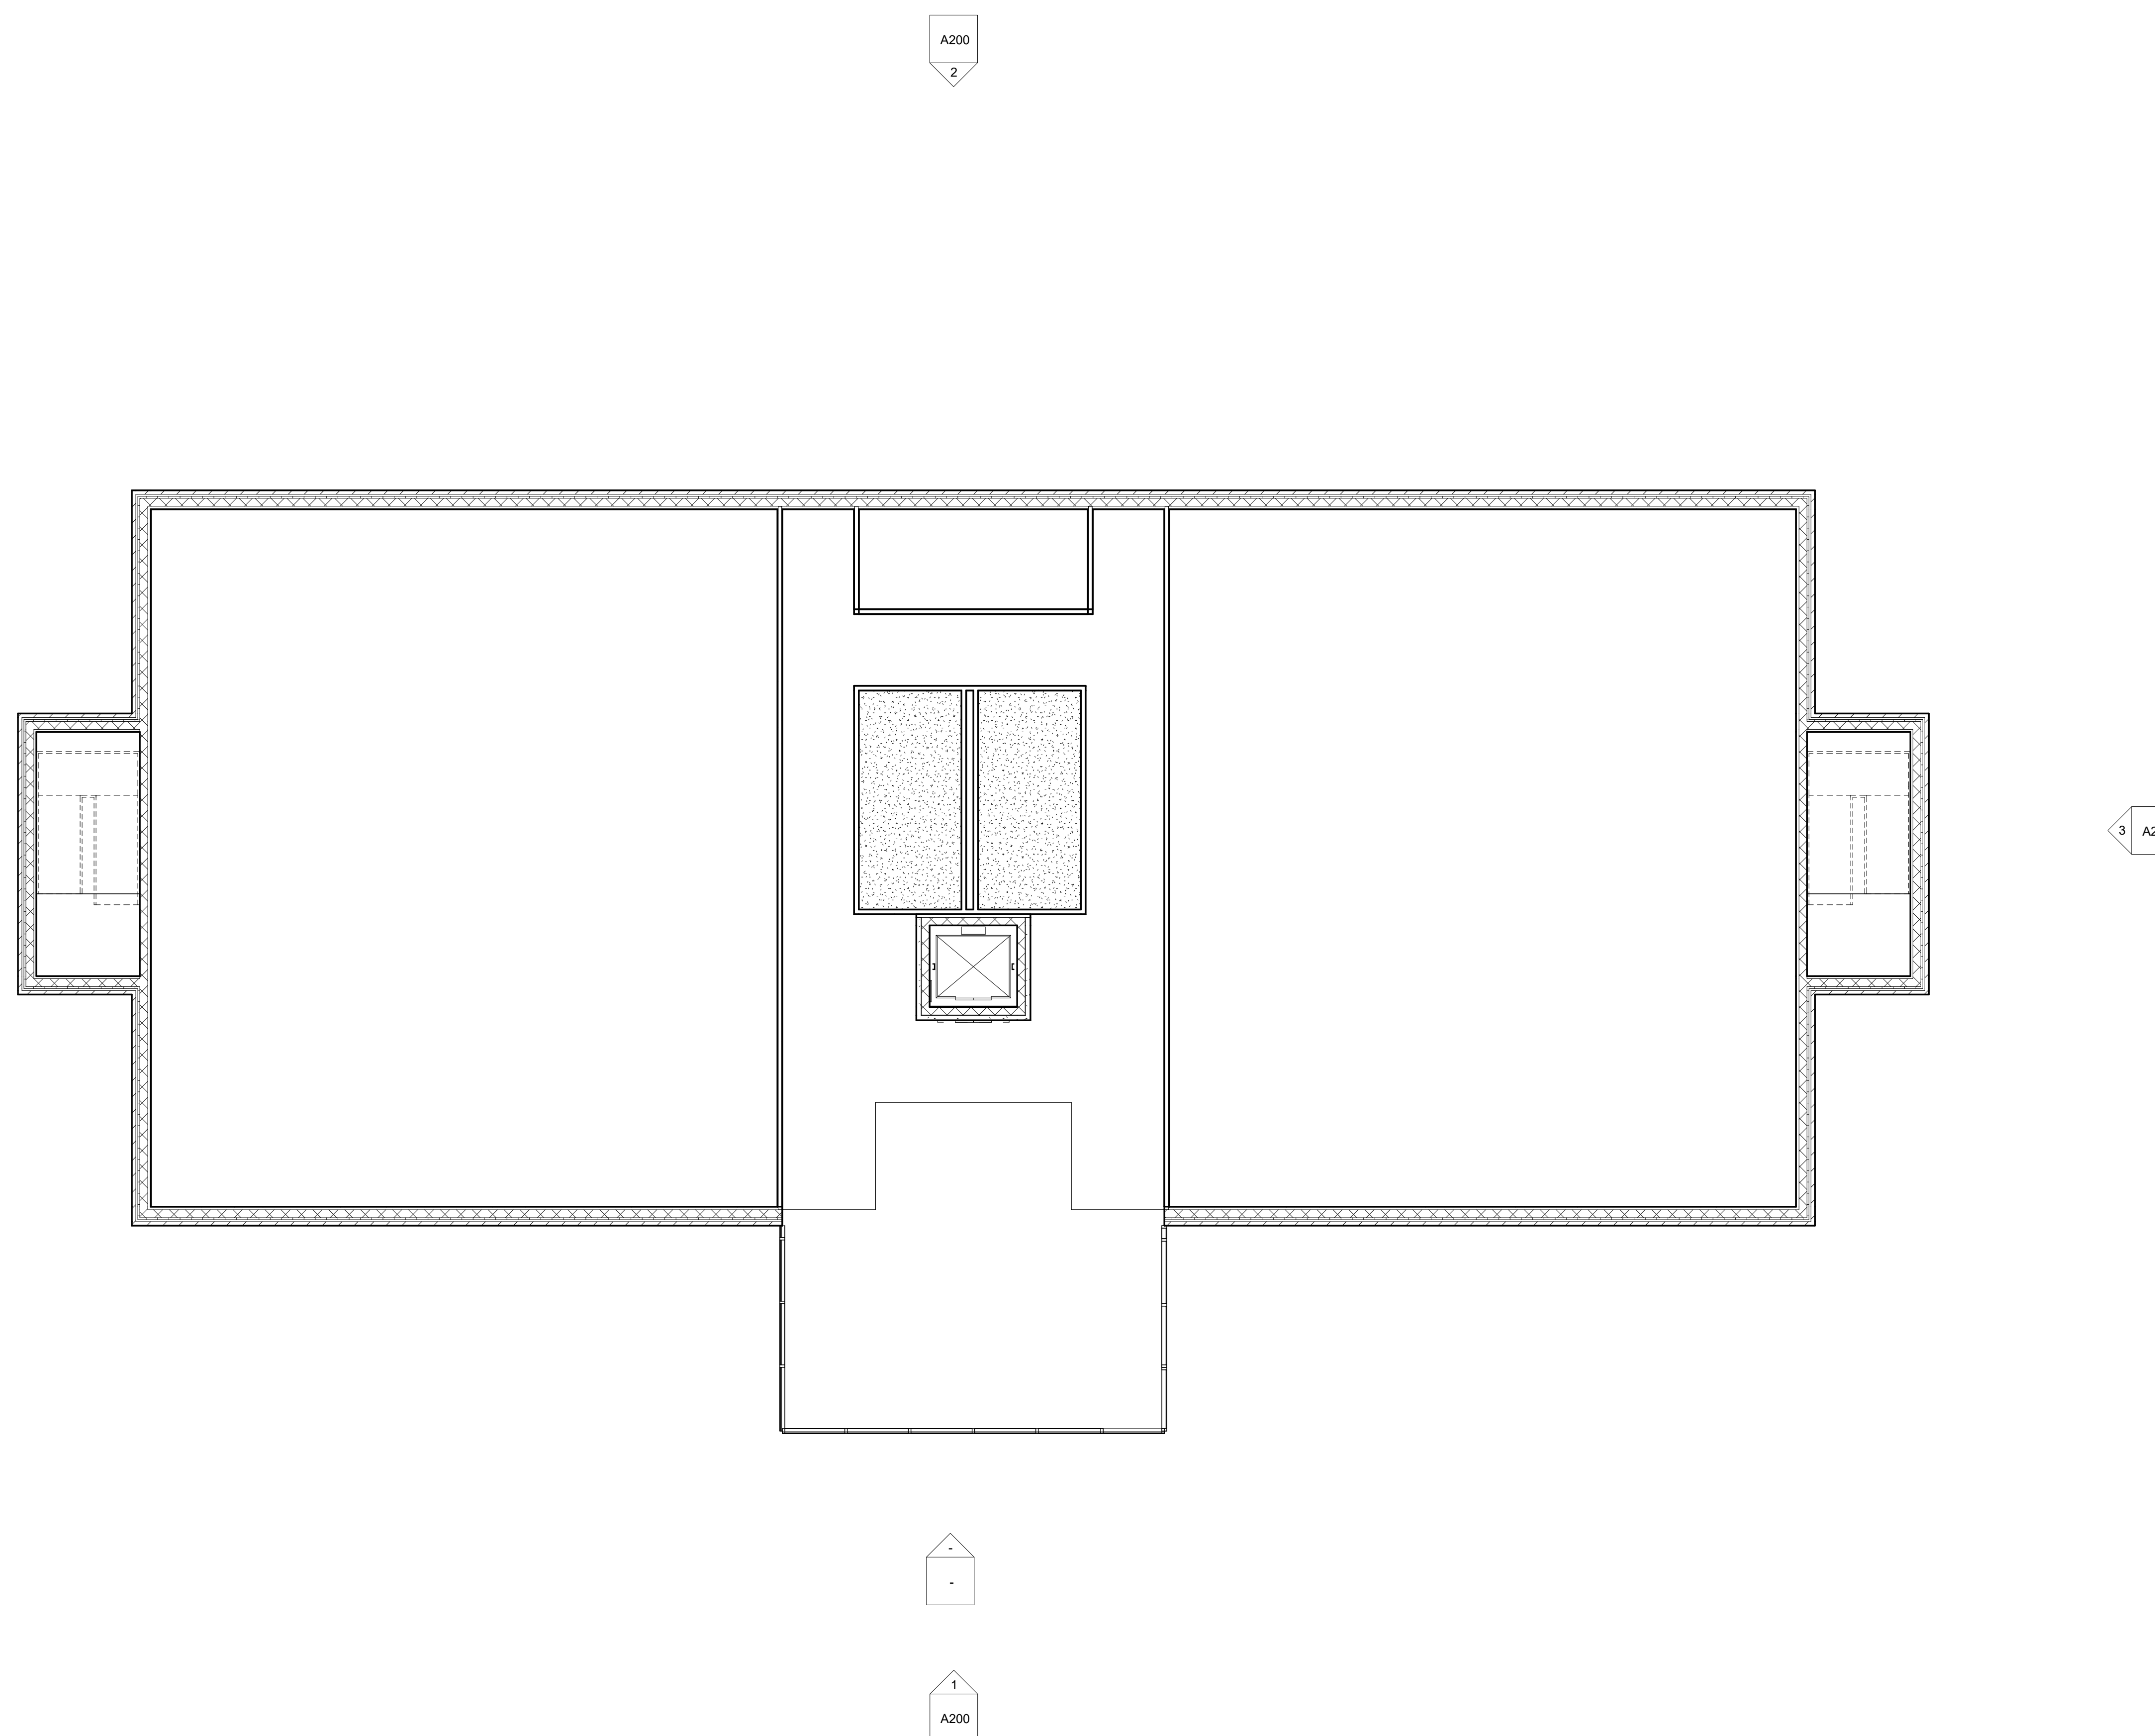



www.autodesk.com/revit

Consultant
Address
Address
Address
Phone

Consultant
Address
Address
Address
Phone

Consultant
Address
Address
Address
Phone

Consultant
Address
Address
Address
Phone

Consultant
Address
Address
Address
Phone

[illegible]

T.H.E Developers

Harbor View Offices

Level 3 Reflected Ceiling

Project Number	2026-001
----------------	----------


Date	June 3, 2026
------	--------------

Drawn By	Author
----------	--------

Checked By	Checker
------------	---------

A113

Scale	1/8" = 1'-0"
-------	--------------

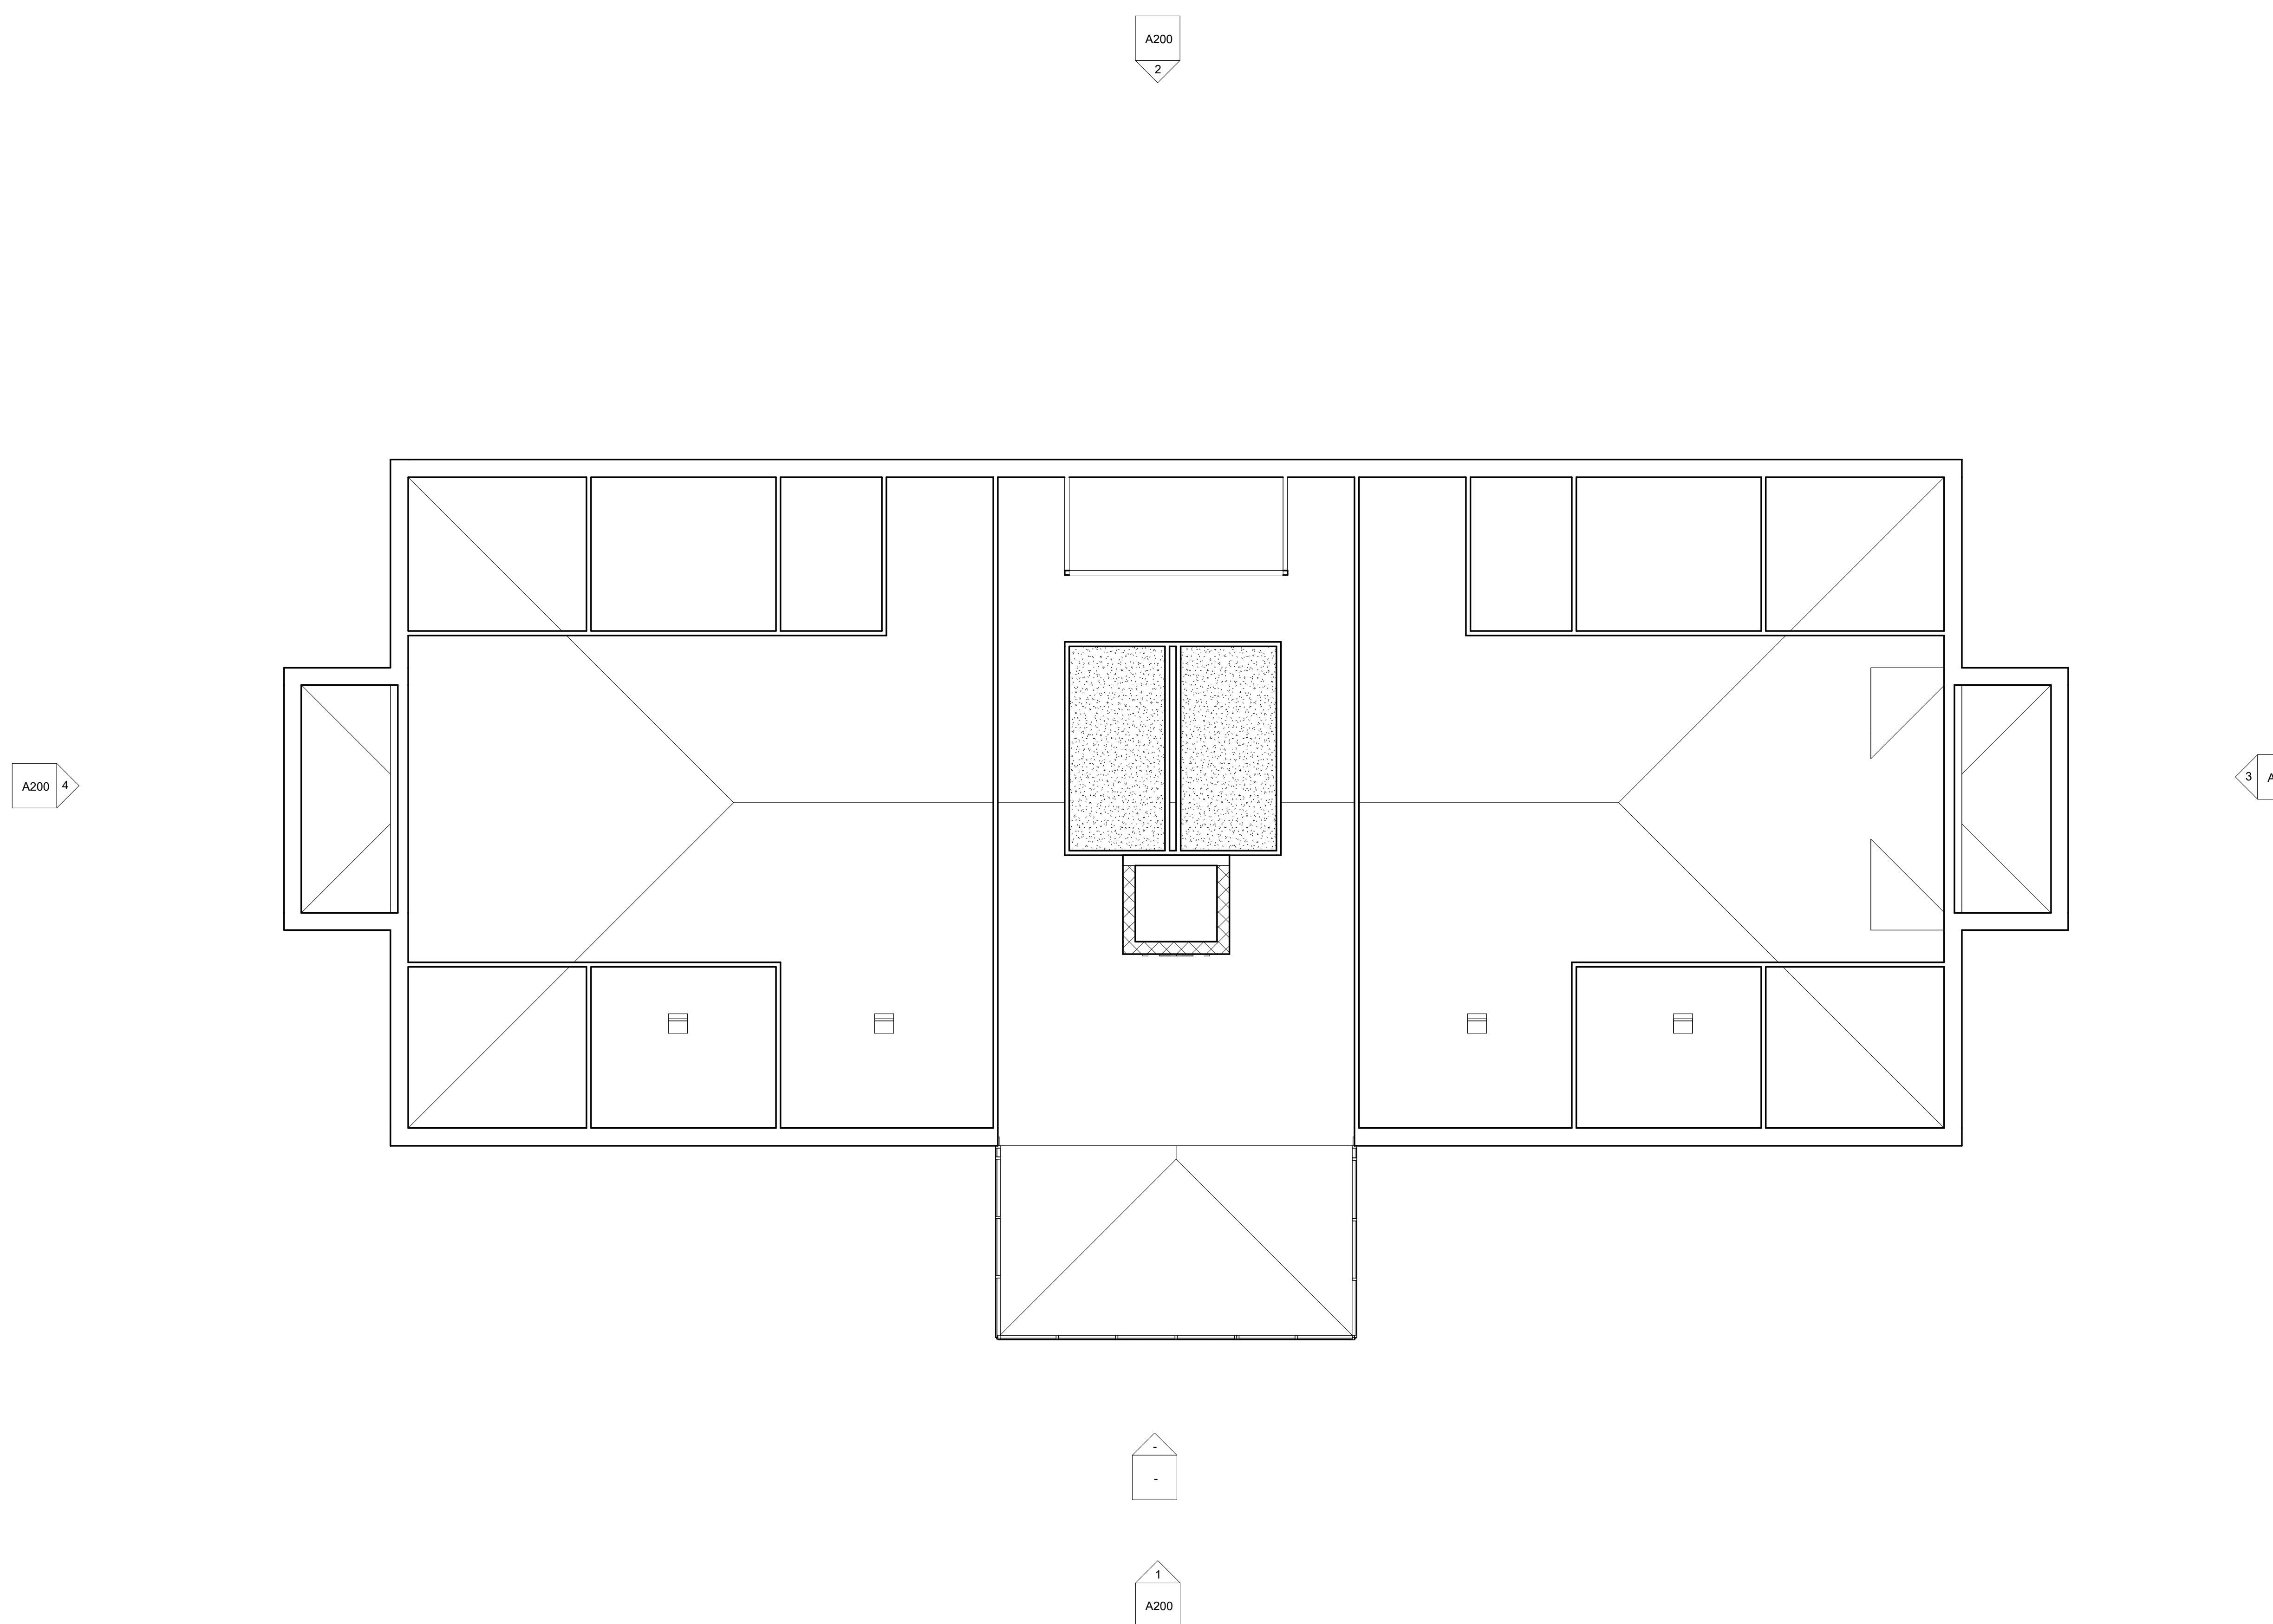[illegible]

① Level 3
1/8" = 1'-0"



www.autodesk.com/revit

Consultant
Address
Address
Address
Phone

Consultant
Address
Address
Address
Phone

Consultant
Address
Address
Address
Phone

Consultant
Address
Address
Address
Phone

Consultant
Address
Address
Address
Phone

[illegible]

T.H.E Developers

Harbor View Offices

Unnamed

Project Number	2026-001
----------------	----------

Date	June 3, 2026
------	--------------

Drawn By	Author
----------	--------

Checked By	Checker
------------	---------

A114

	Scale
--	-------



Consultant
Address
Address
Address
Phone

[illegible]





T.H.E Developers
Harbor View Offices
Exterior Elevations

Project Number	2026-001
Date	June 3, 2026
Drawn By	Author
Checked By	Checker

A200

Scale $1/8" = 1'-0"$

6/8/2026 5:35:55 PM

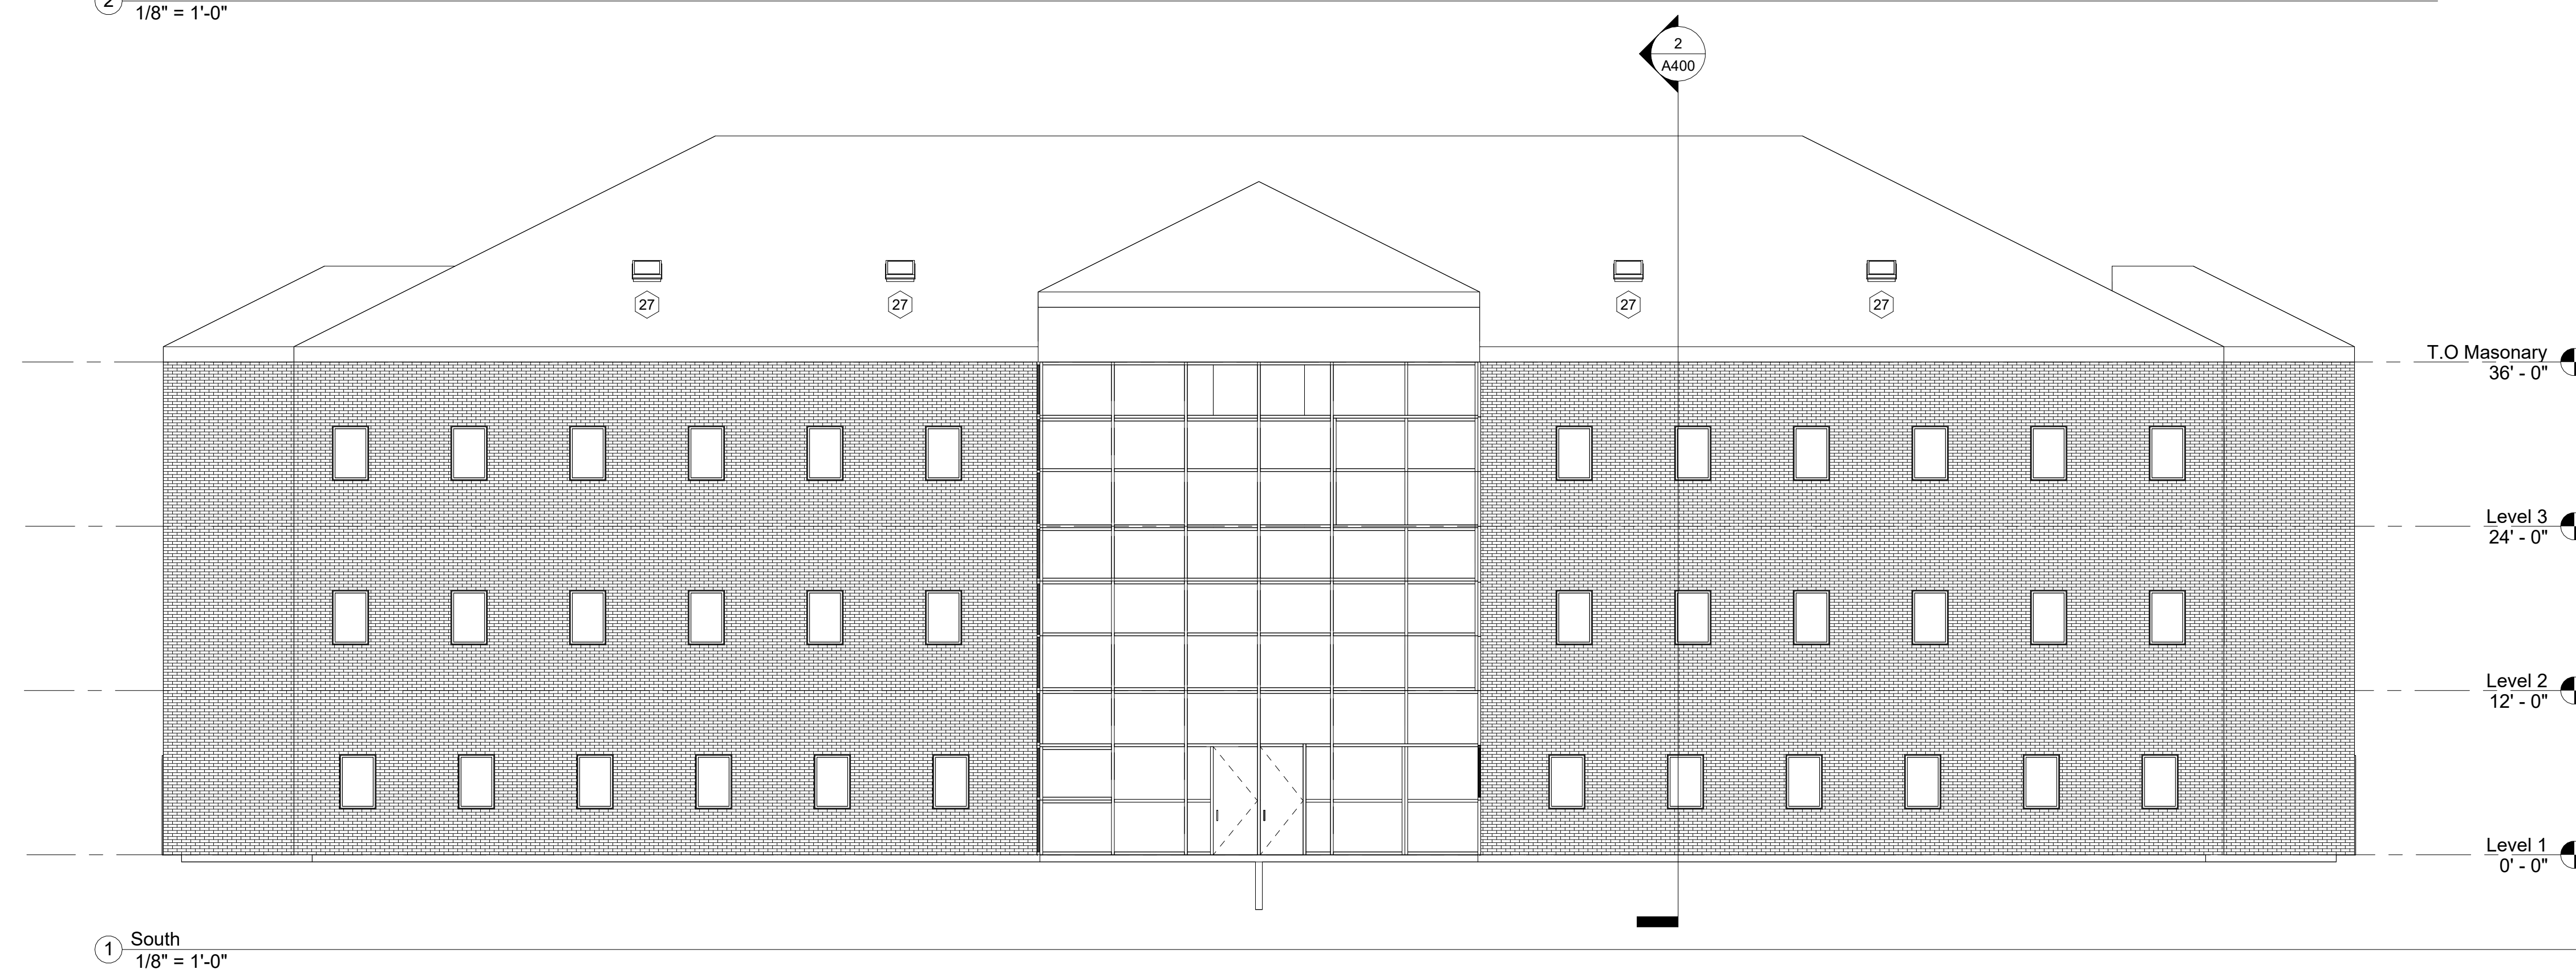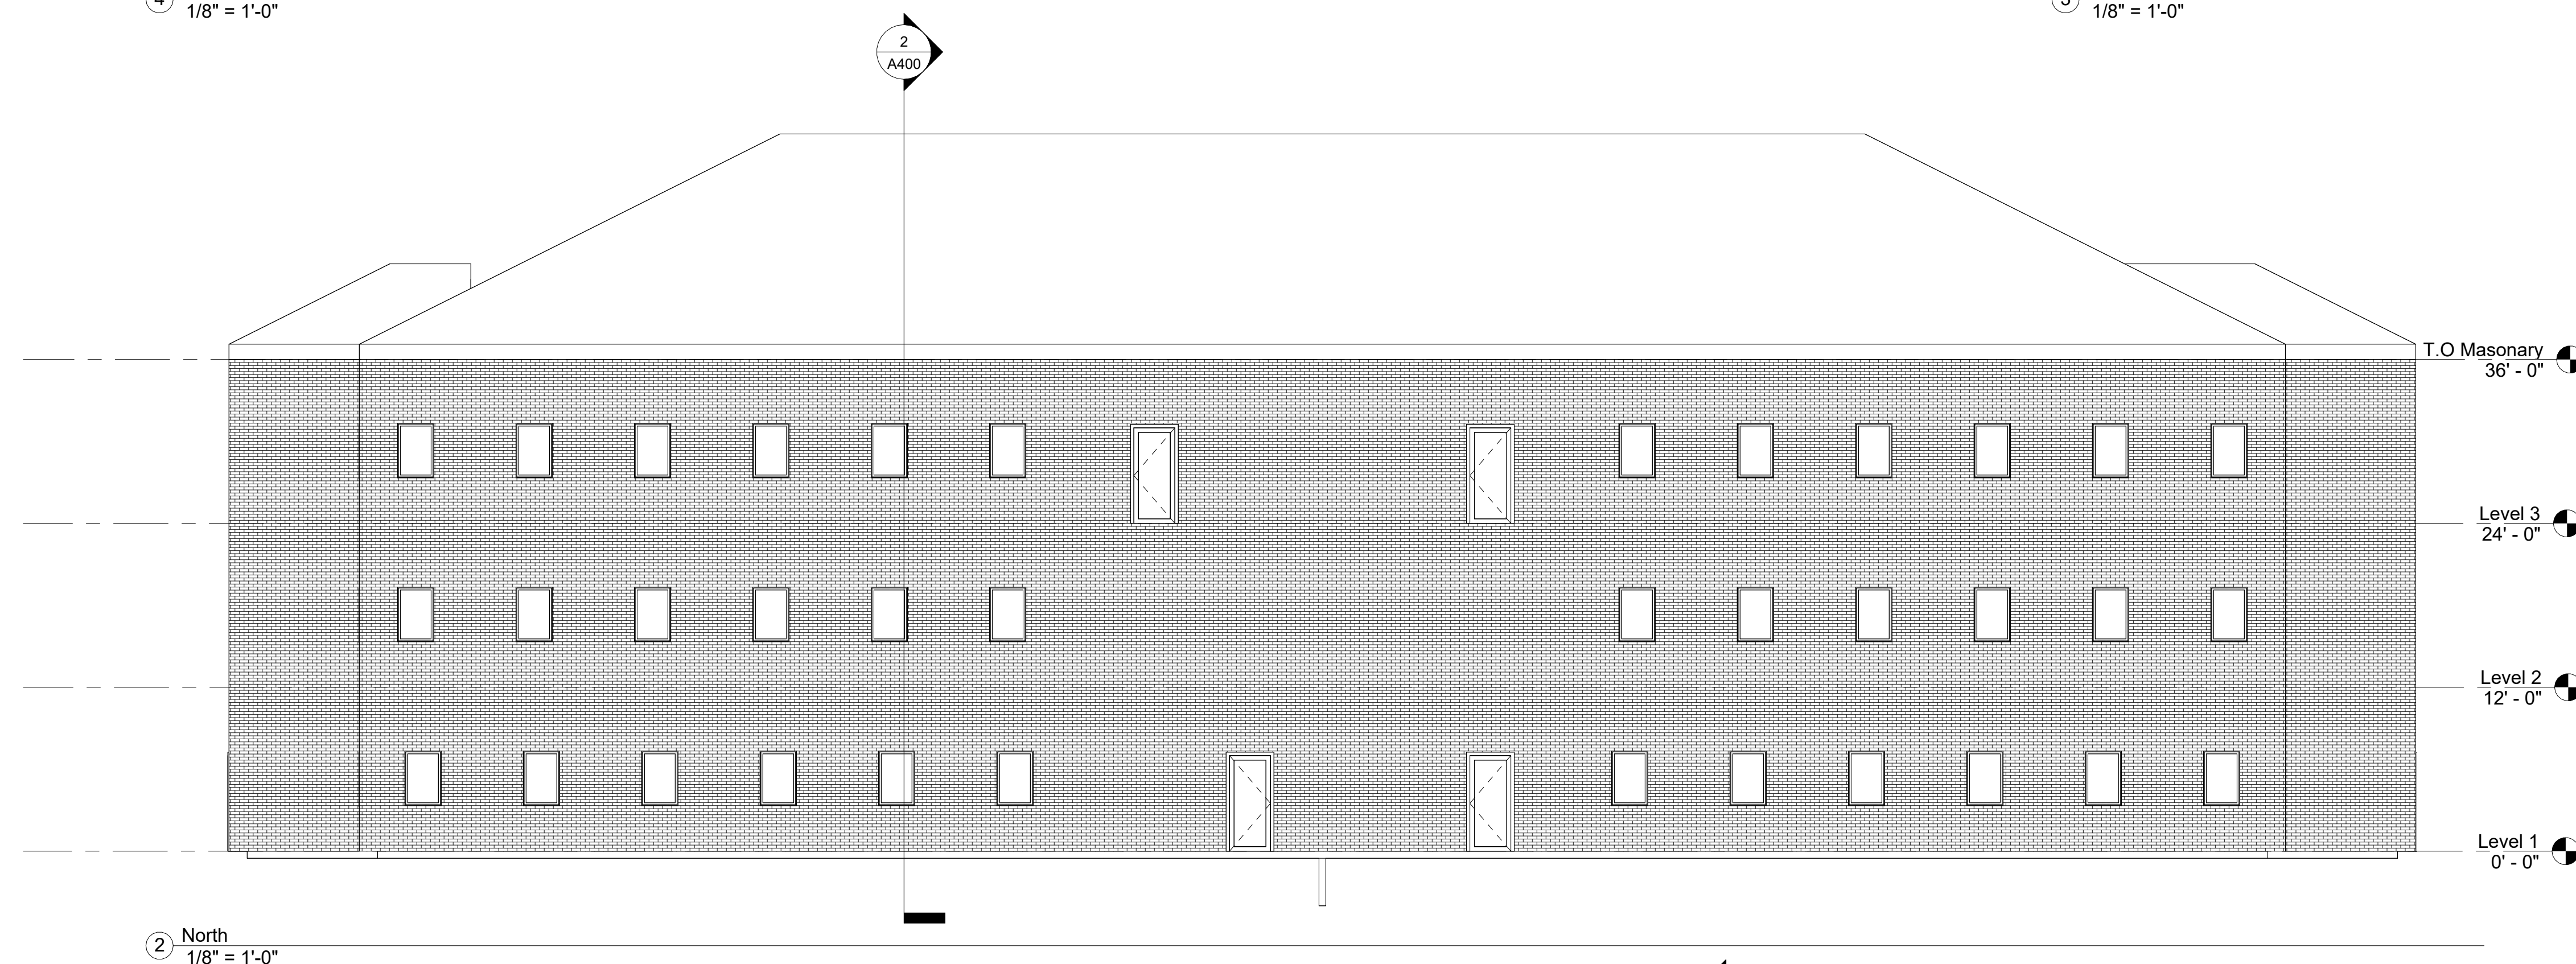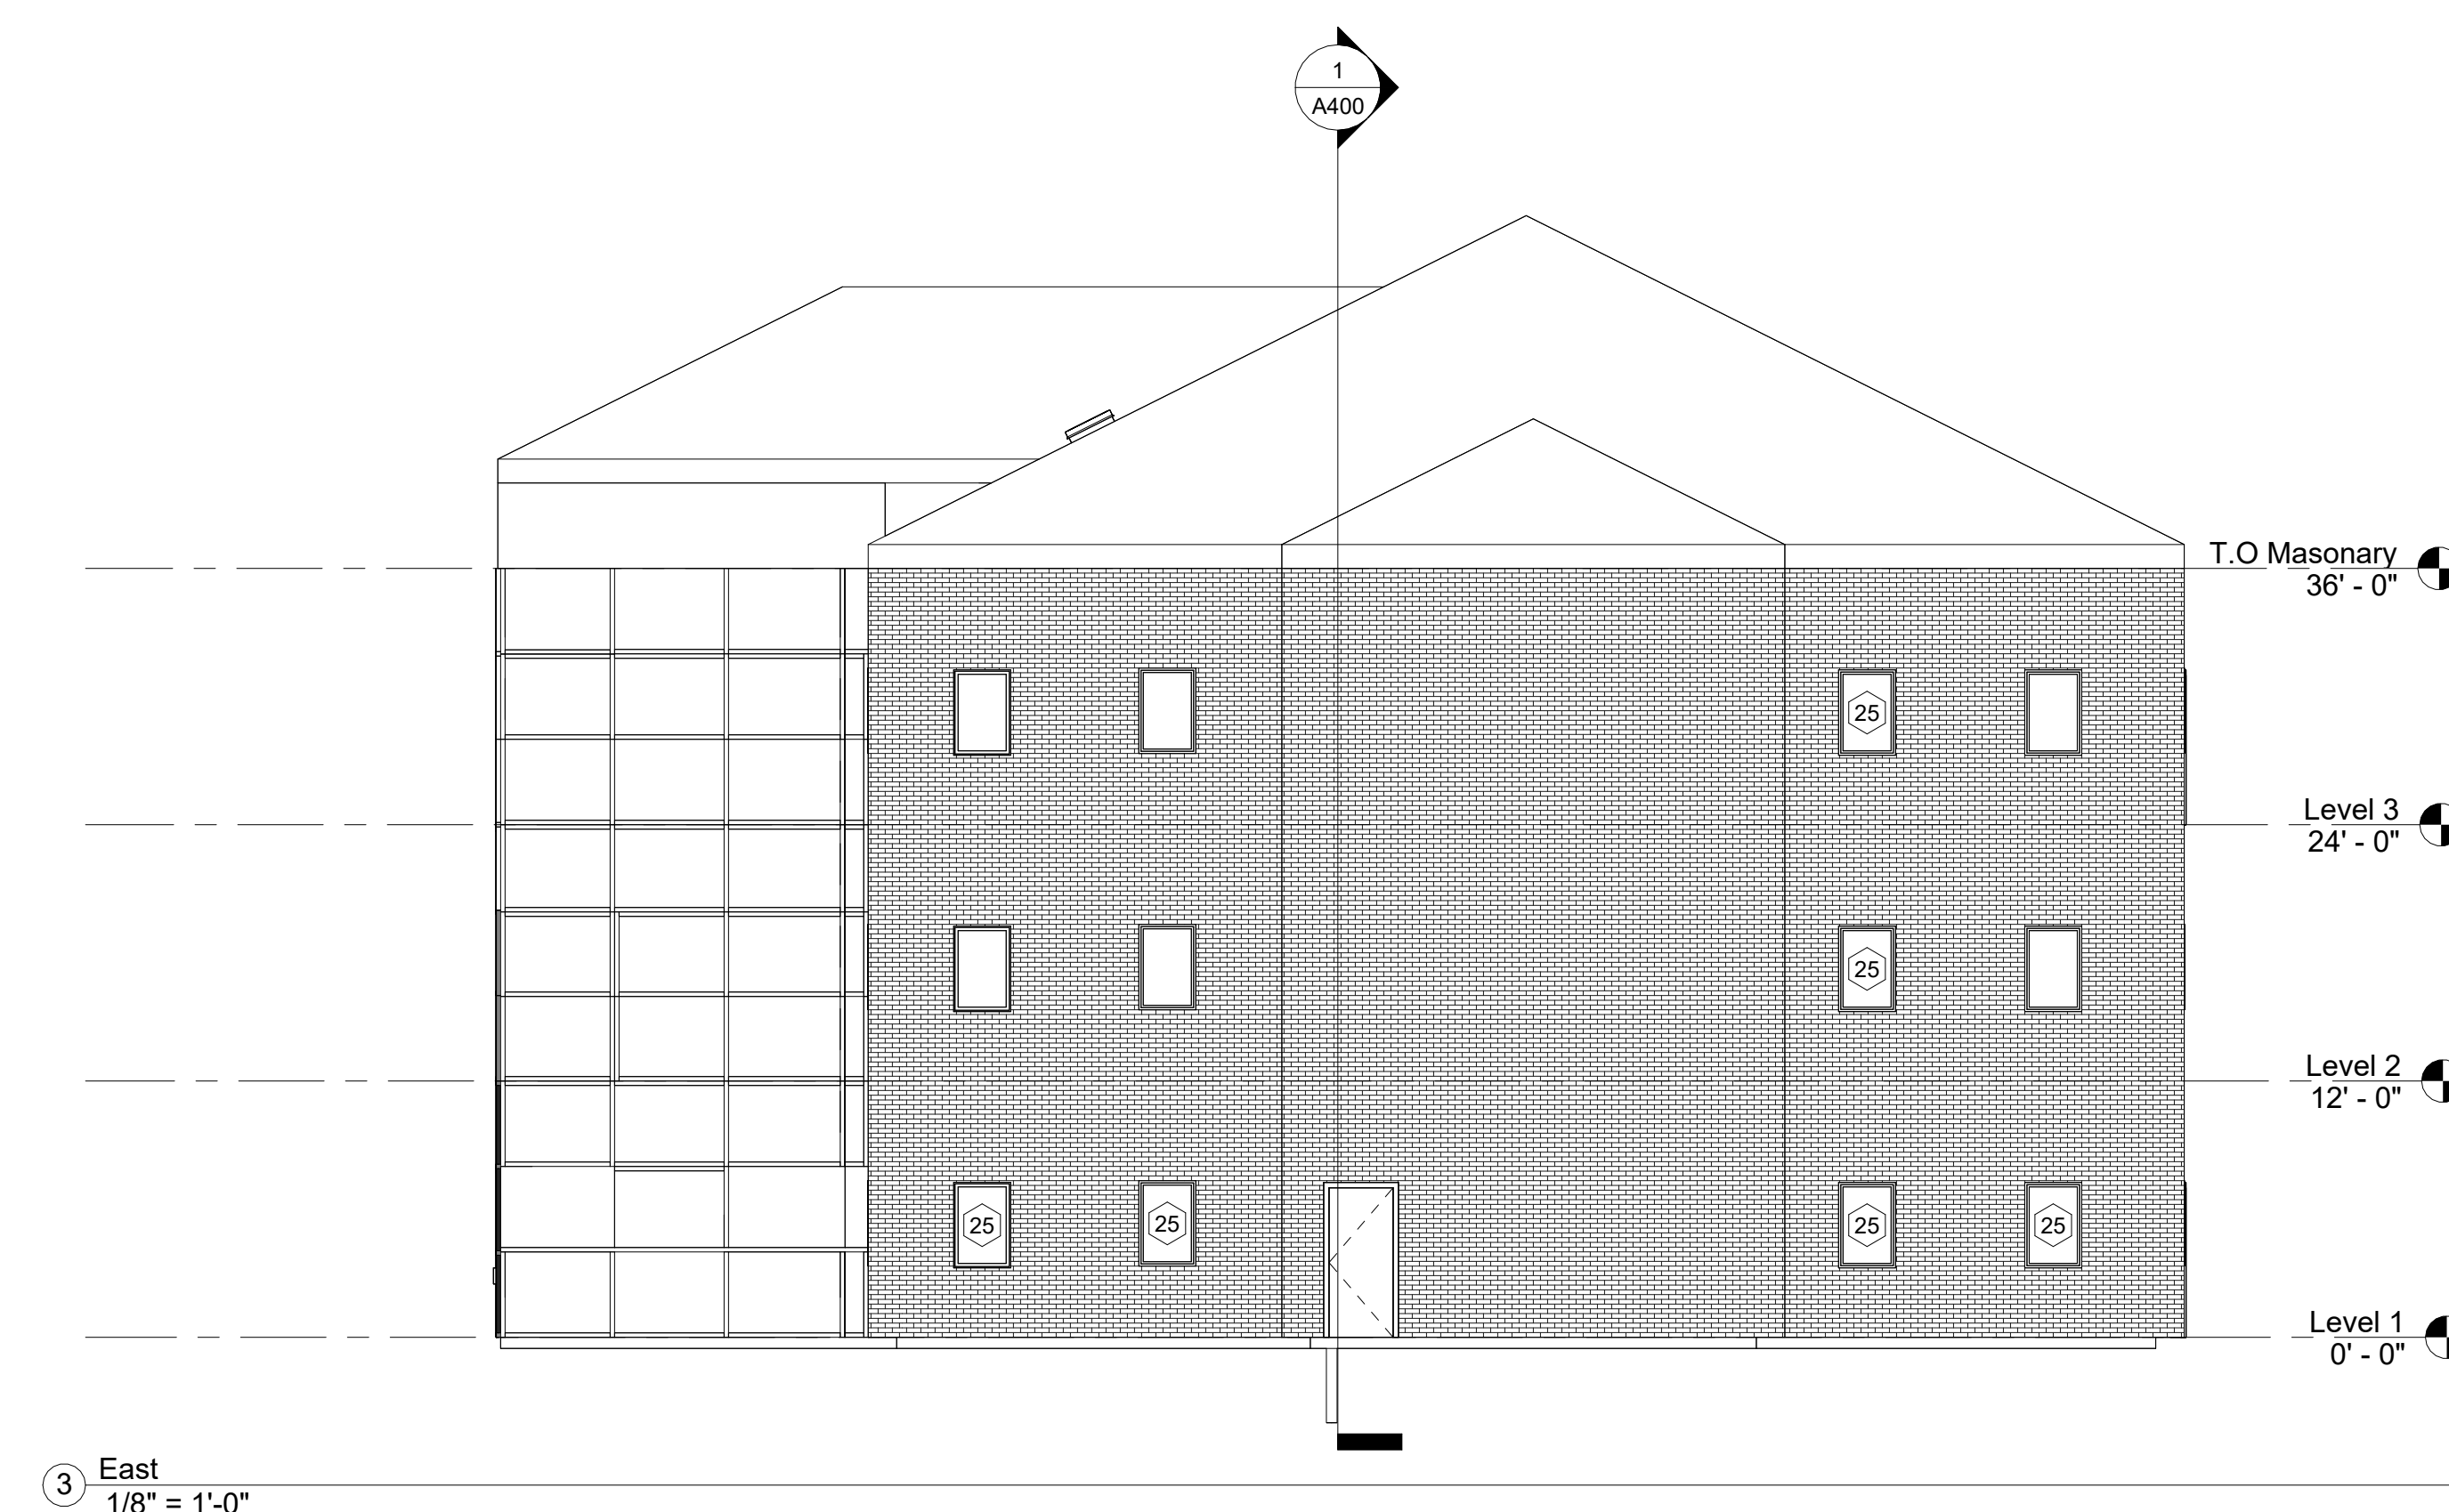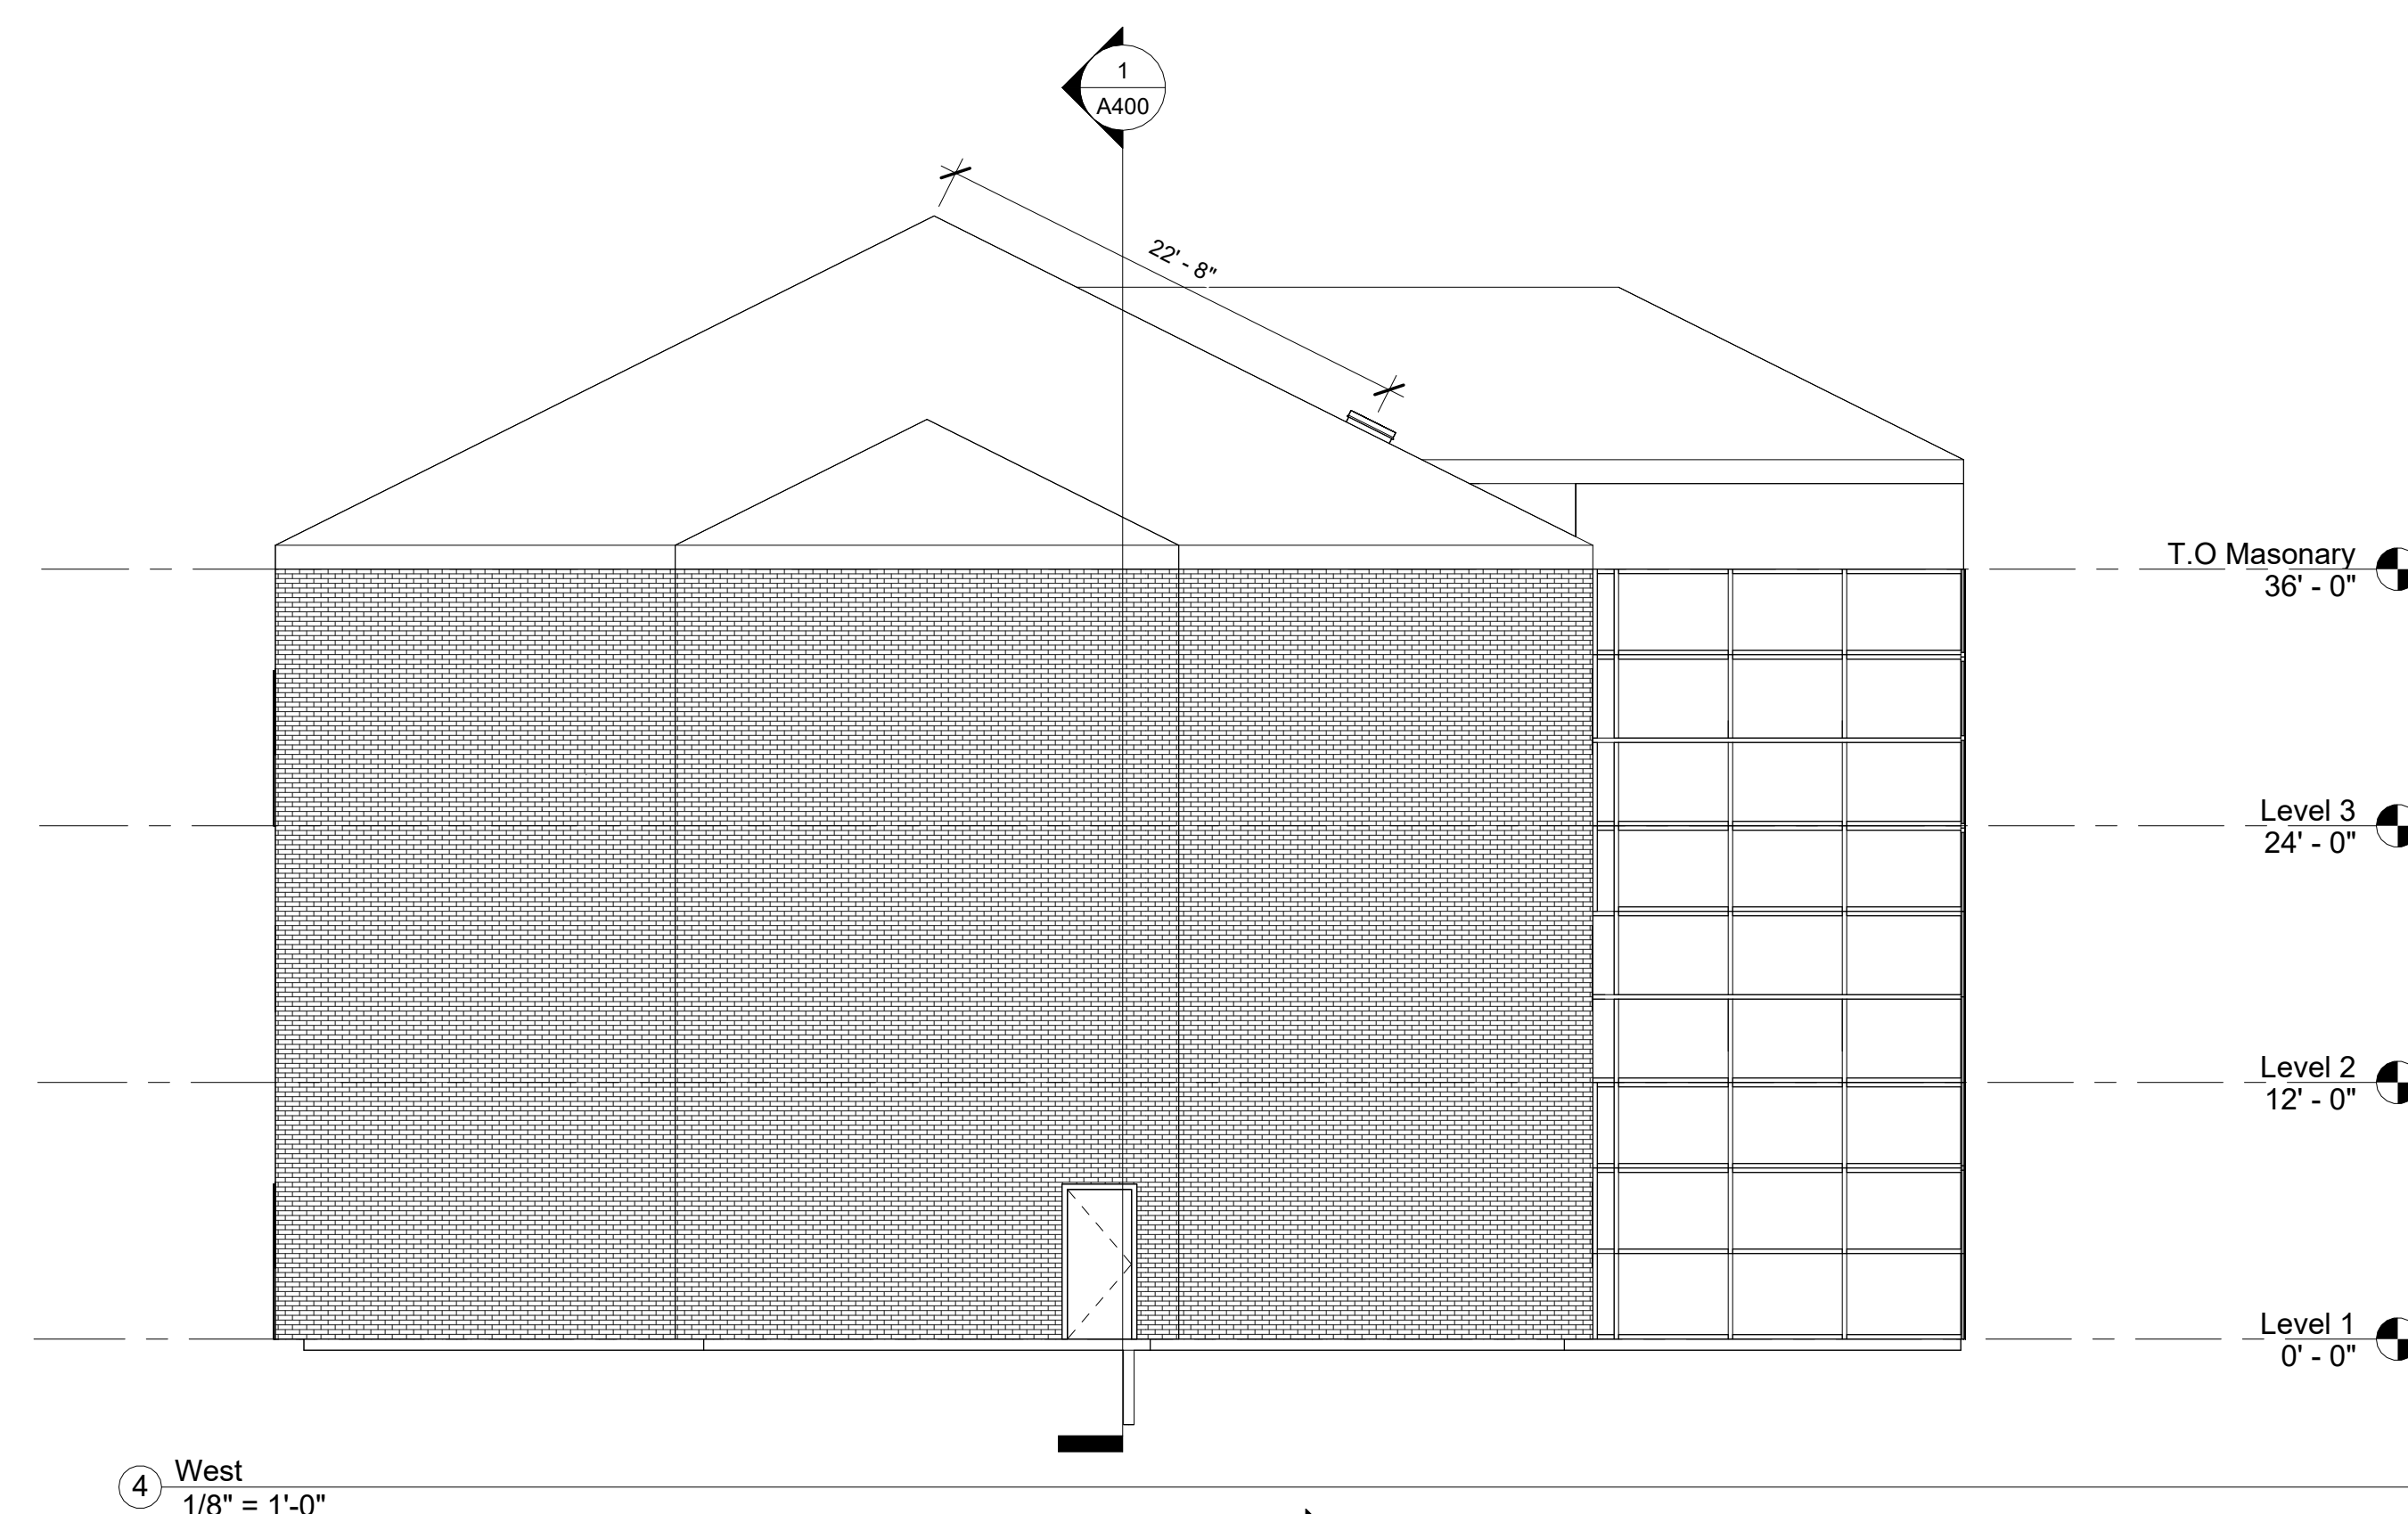




Consultant
Address
Address
Address
Phone

[illegible]

Wall Sections

Project Number	2026-001
Date	June 3, 2026
Drawn By	Author
Checked By	Checker

Scale	As indicated
-------	--------------

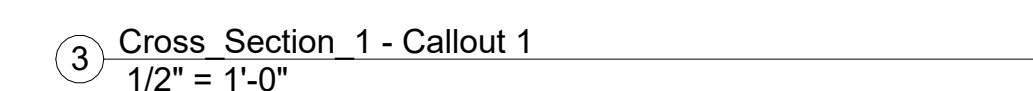



www.autodesk.com/revit


Consultant
Address
Address
Address
Phone

Consultant
Address
Address
Address
Phone


Consultant
Address
Address
Address
Phone

Consultant
Address
Address
Address
Phone

Consultant
Address
Address
Address
Phone

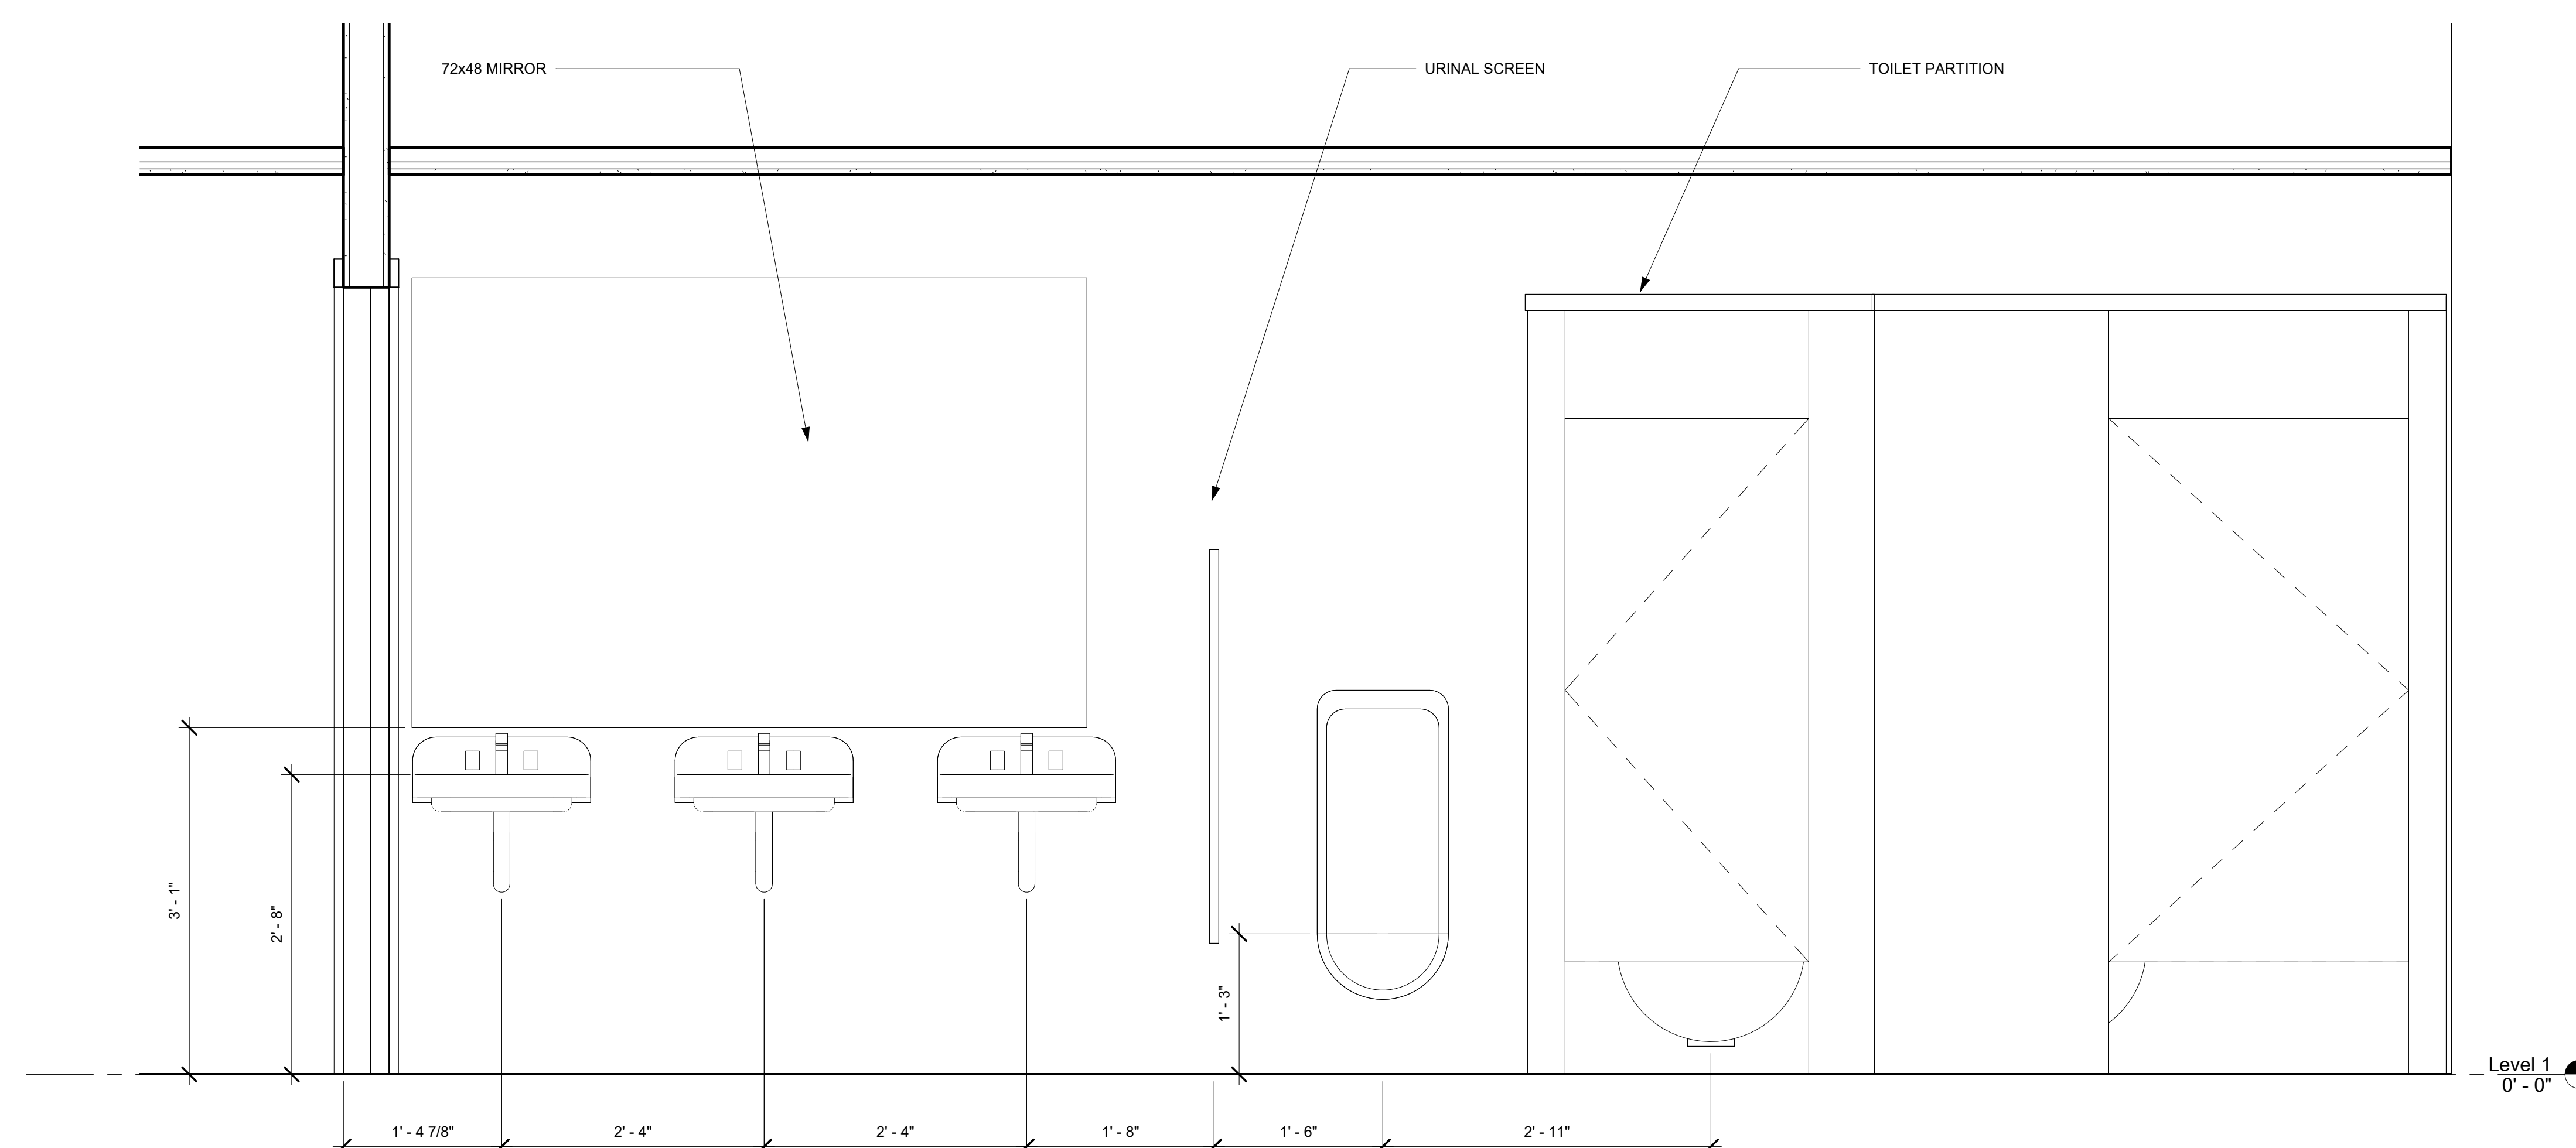

② Mens Restroom
1" = 1'-0"

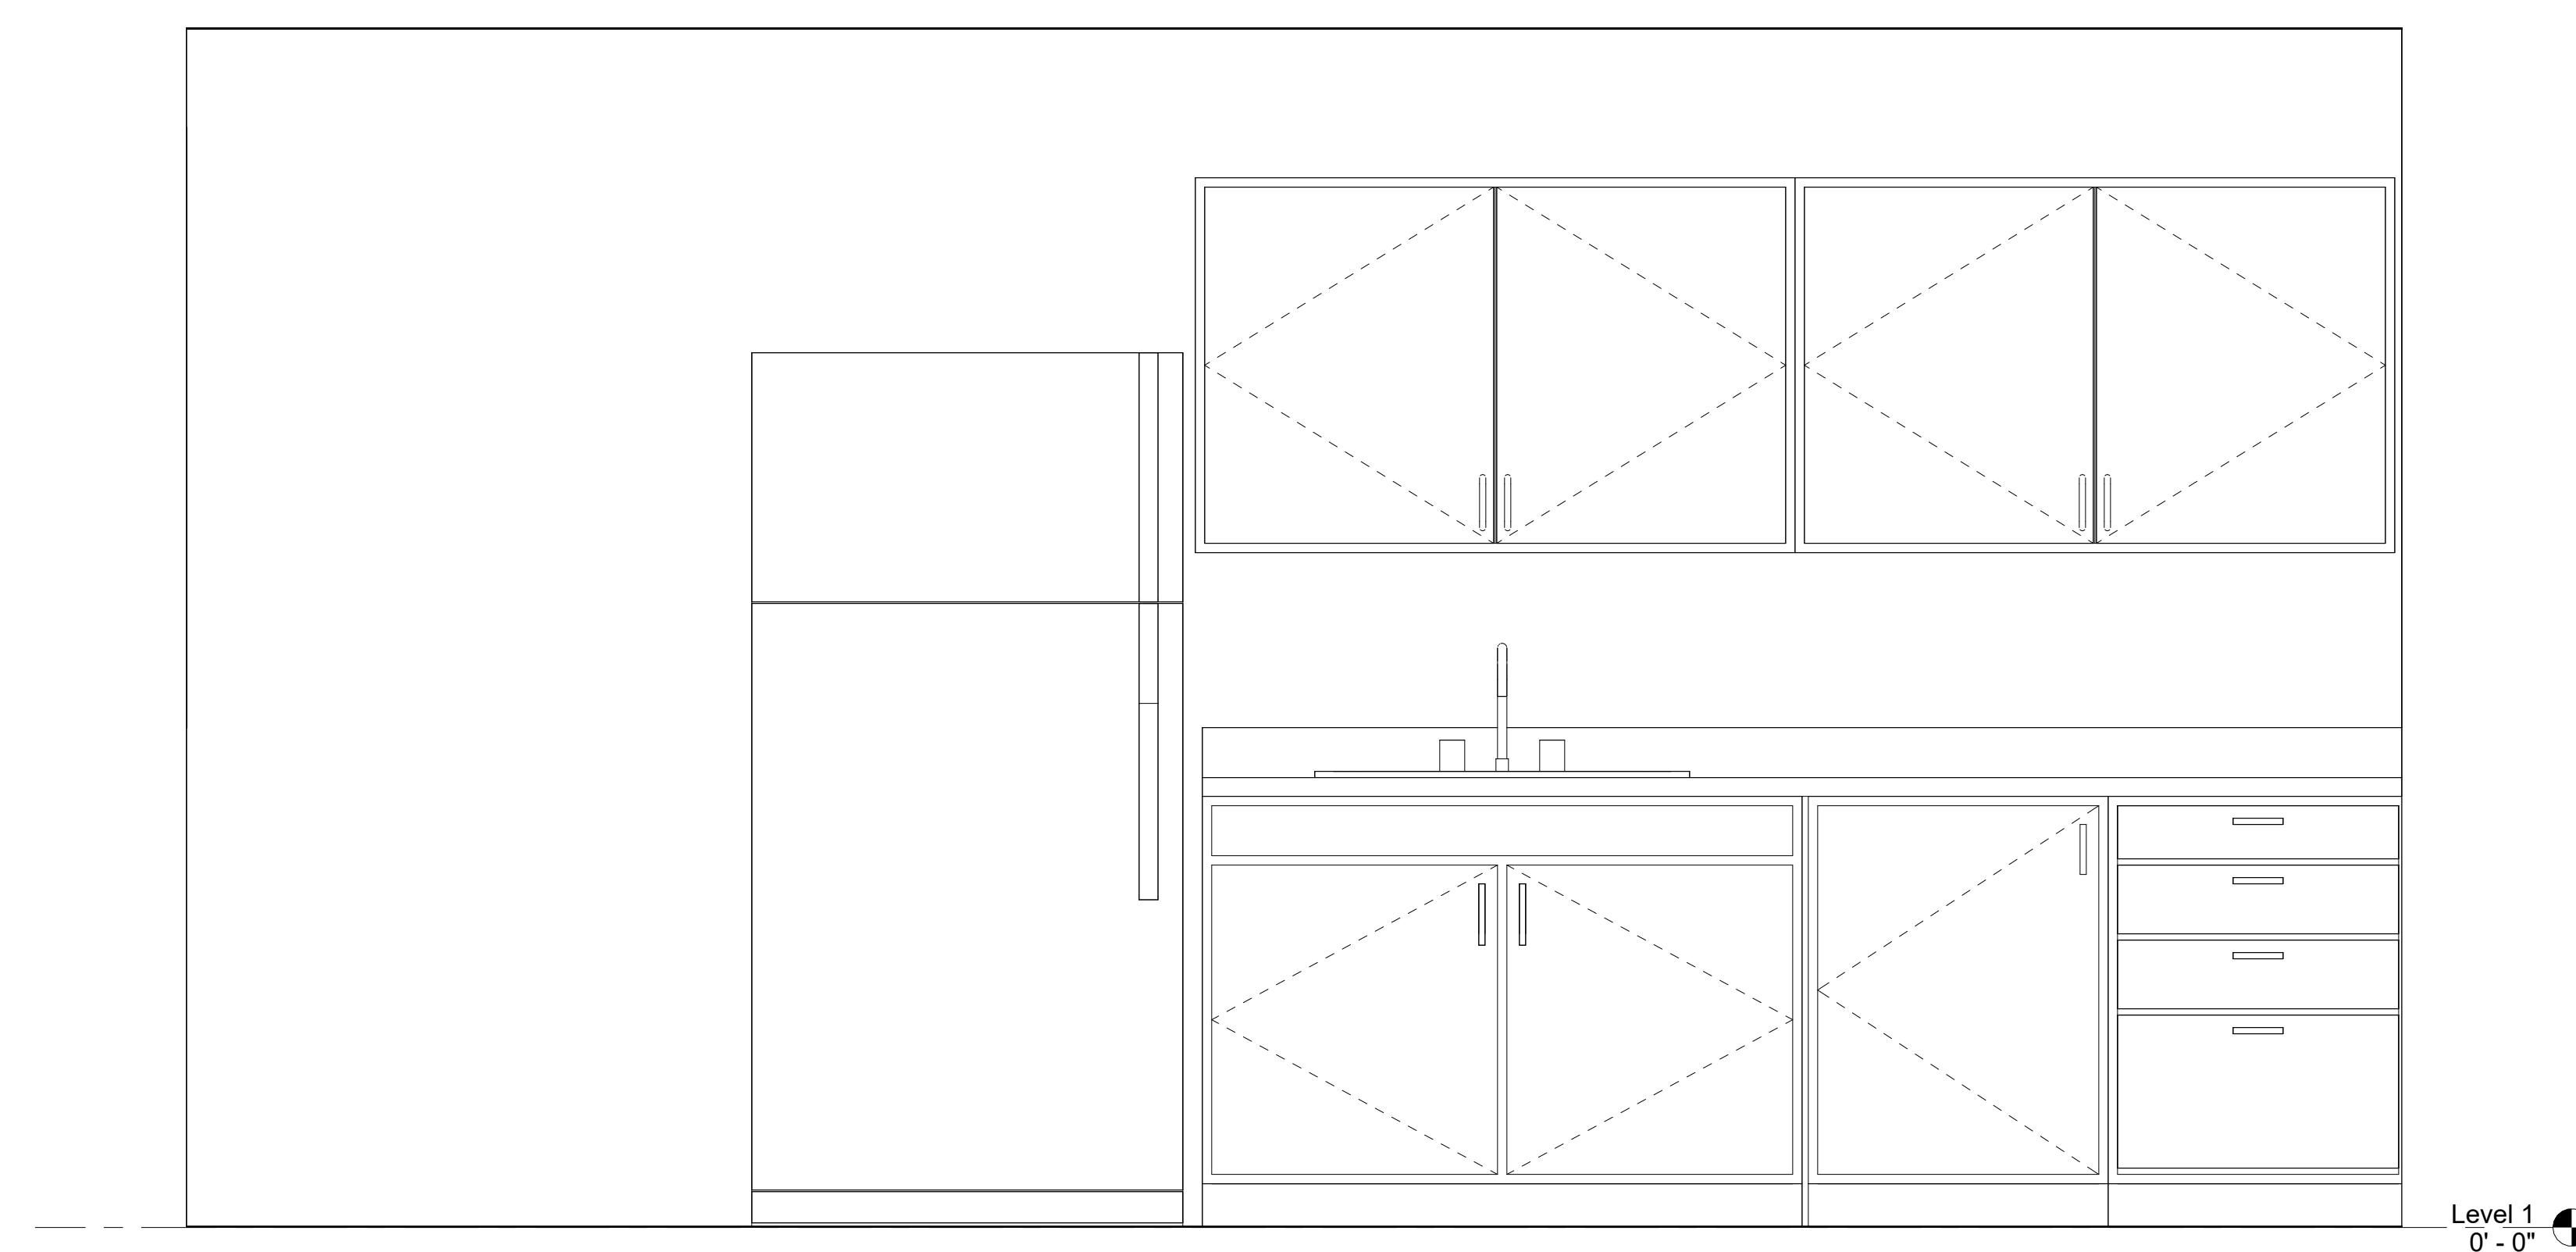

① Break Room East
1" = 1'-0"

[illegible]

T.H.E Developers

Harbor View Offices

Interior Elevations

Project Number	2026-001
----------------	----------

Date	June 3, 2026
------	--------------


Drawn By	Author
----------	--------

Checked By	Checker
------------	---------


A500

Scale	1" = 1'-0"
-------	------------


Keynote Legend	
Key Value	Keynote Text
09 29 00.C1	1/2" Gypsum Wallboard

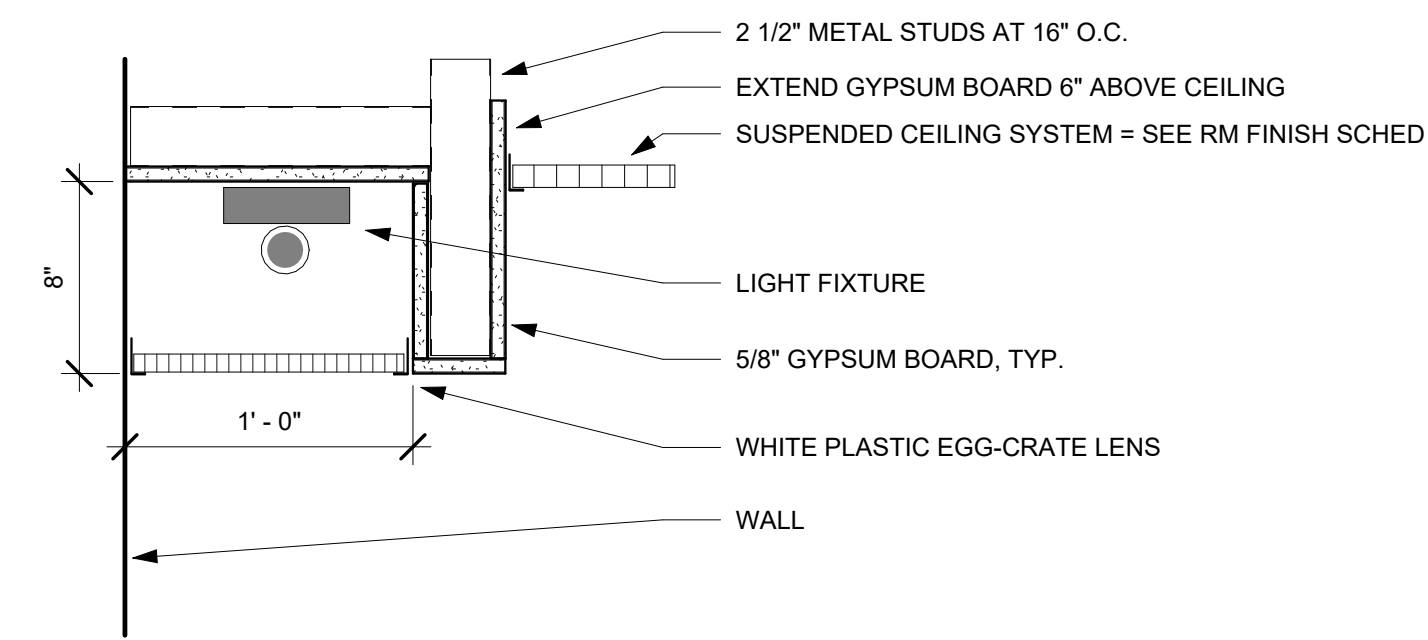


5 Toilet Room Ceiling Detail
1 1/2" = 1'-0"

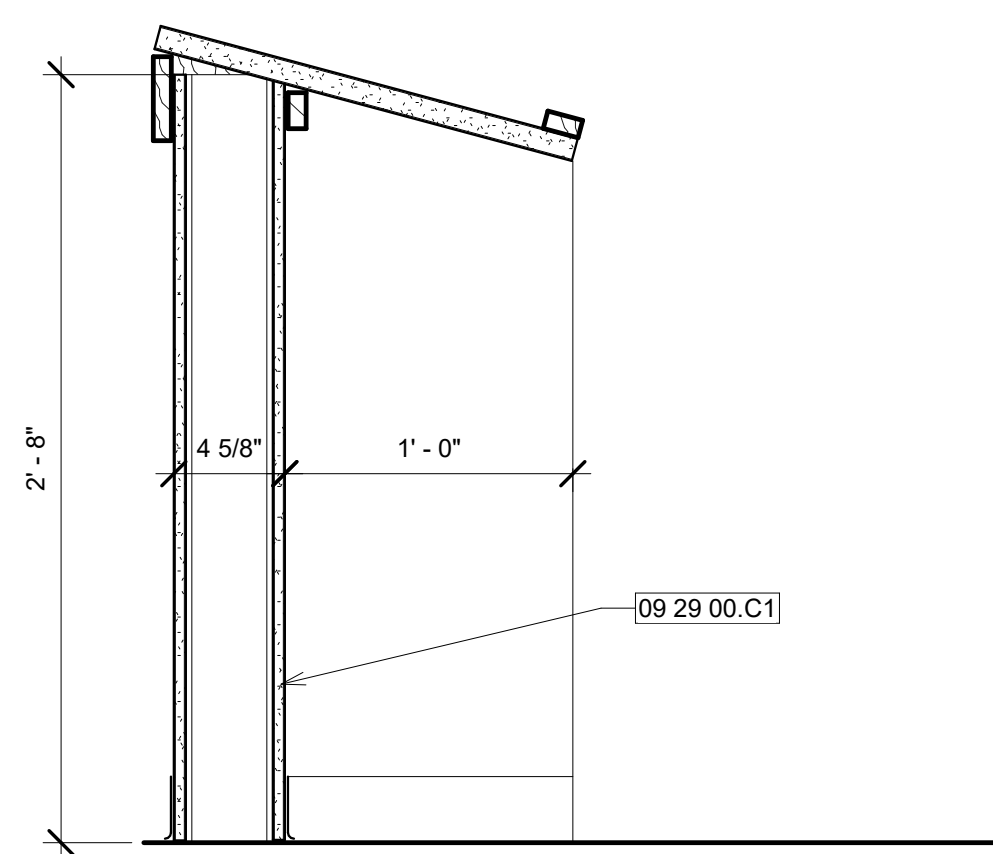


7 Fixed Student Desk - KEYNOTES
1 1/2" = 1'-0"

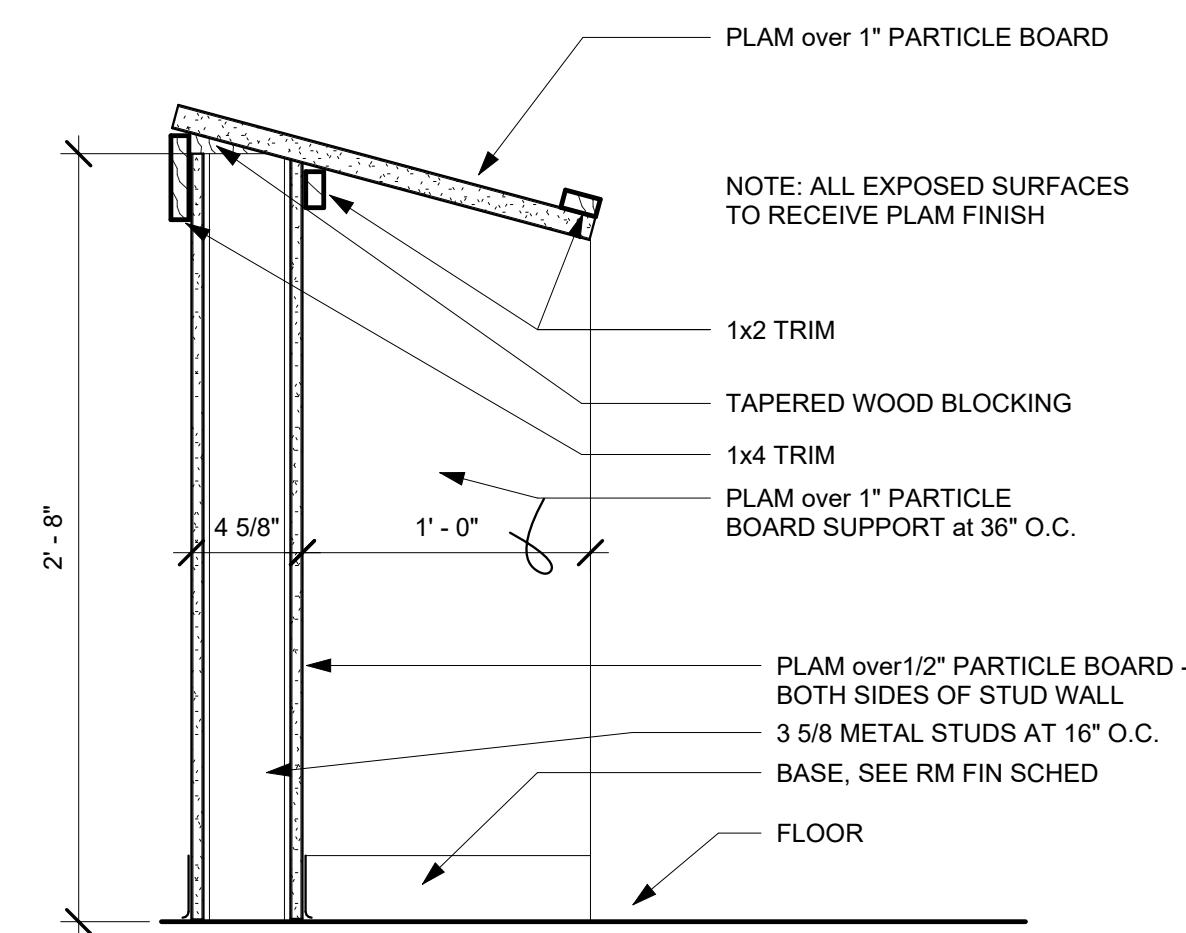


③ Fixed Student Desk
1 1/2" = 1'-0"

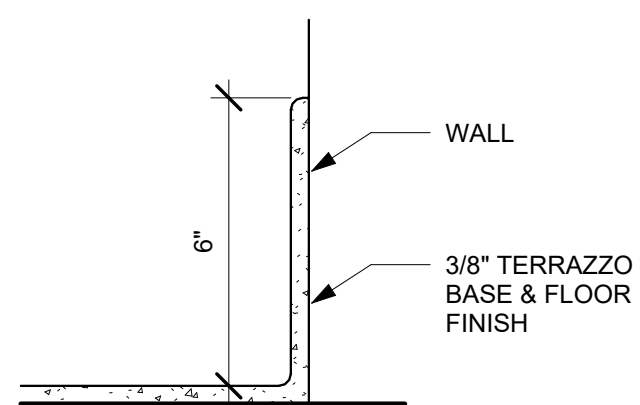


6 Terrazzo Base Detail
3" = 1'-0"

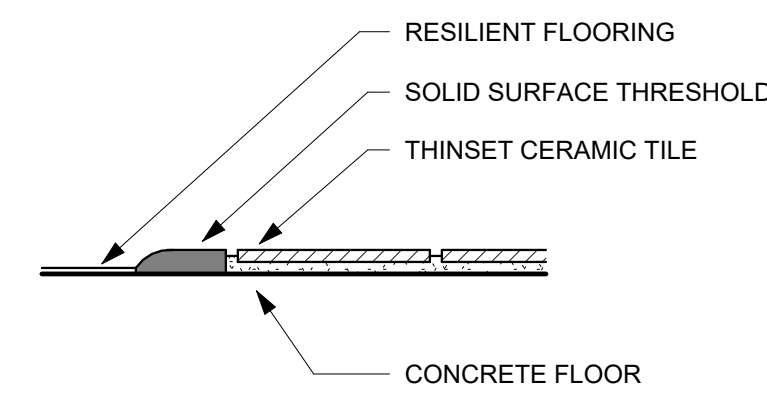

8 Floor Transition Detail
3" = 1'-0"

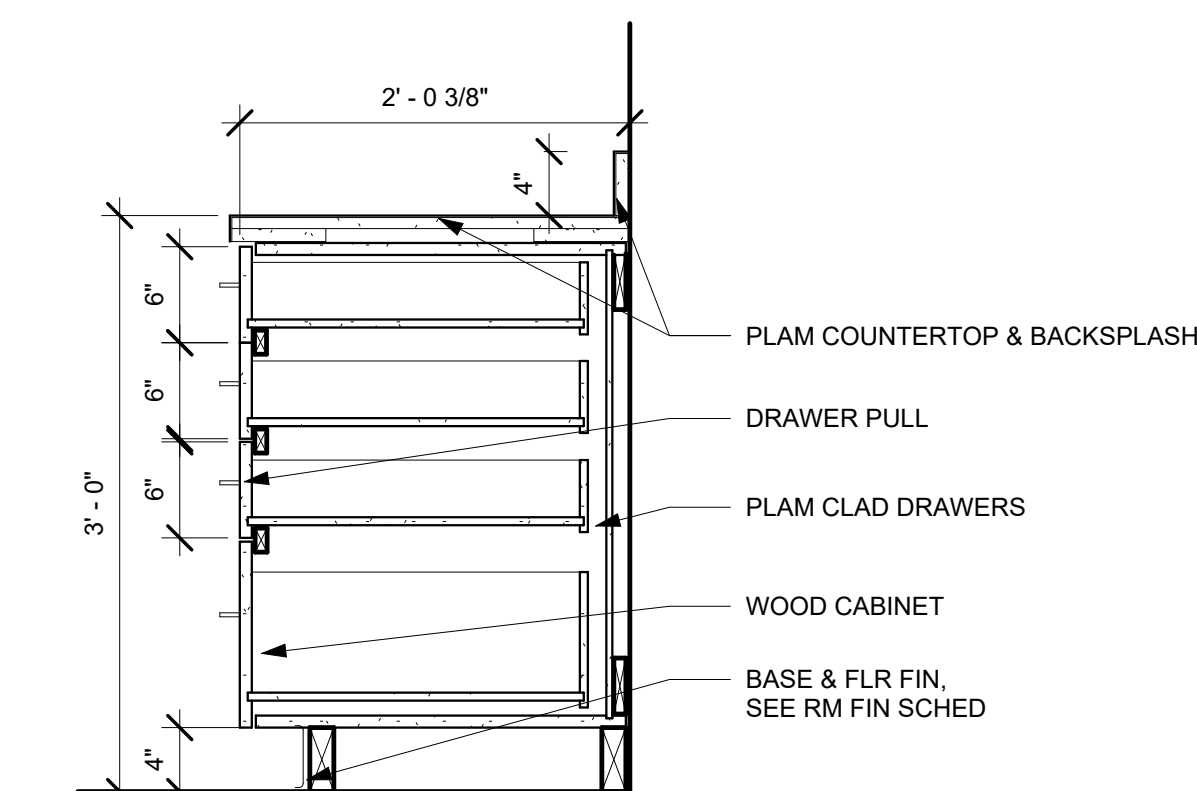

② Base Cabinet Detail - Drawers
1" = 1'-0"

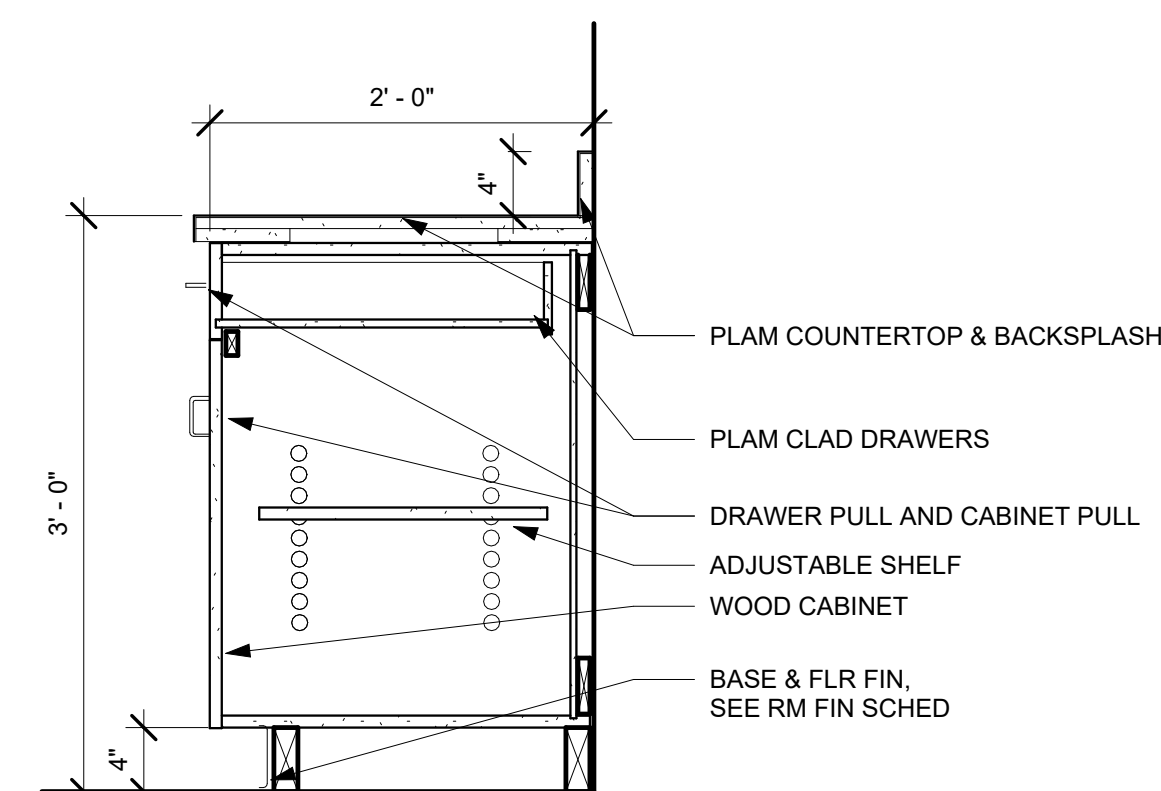

1 Base Cabinet Detail
1" = 1'-0"



www.autodesk.com/revit

Consultant
Address
Address
Address
Phone

Consultant
Address
Address
Address
Phone

Consultant
Address
Address
Address
Phone

Consultant
Address
Address
Address
Phone

Consultant
Address
Address
Address
Phone

[illegible]

T.H.E Developers

Harbor View Offices

Details

Project Number	2026-001
----------------	----------

Date	June 3, 2026
------	--------------

Drawn By	Author
----------	--------

Checked By	Checker
------------	---------

A600

Scale	As indicated
-------	--------------



www.autodesk.com/revit


Consultant
Address
Address
Address
Phone

Consultant
Address
Address
Address
Phone


Consultant
Address
Address
Address
Phone

Consultant
Address
Address
Address
Phone

Consultant
Address
Address
Address
Phone

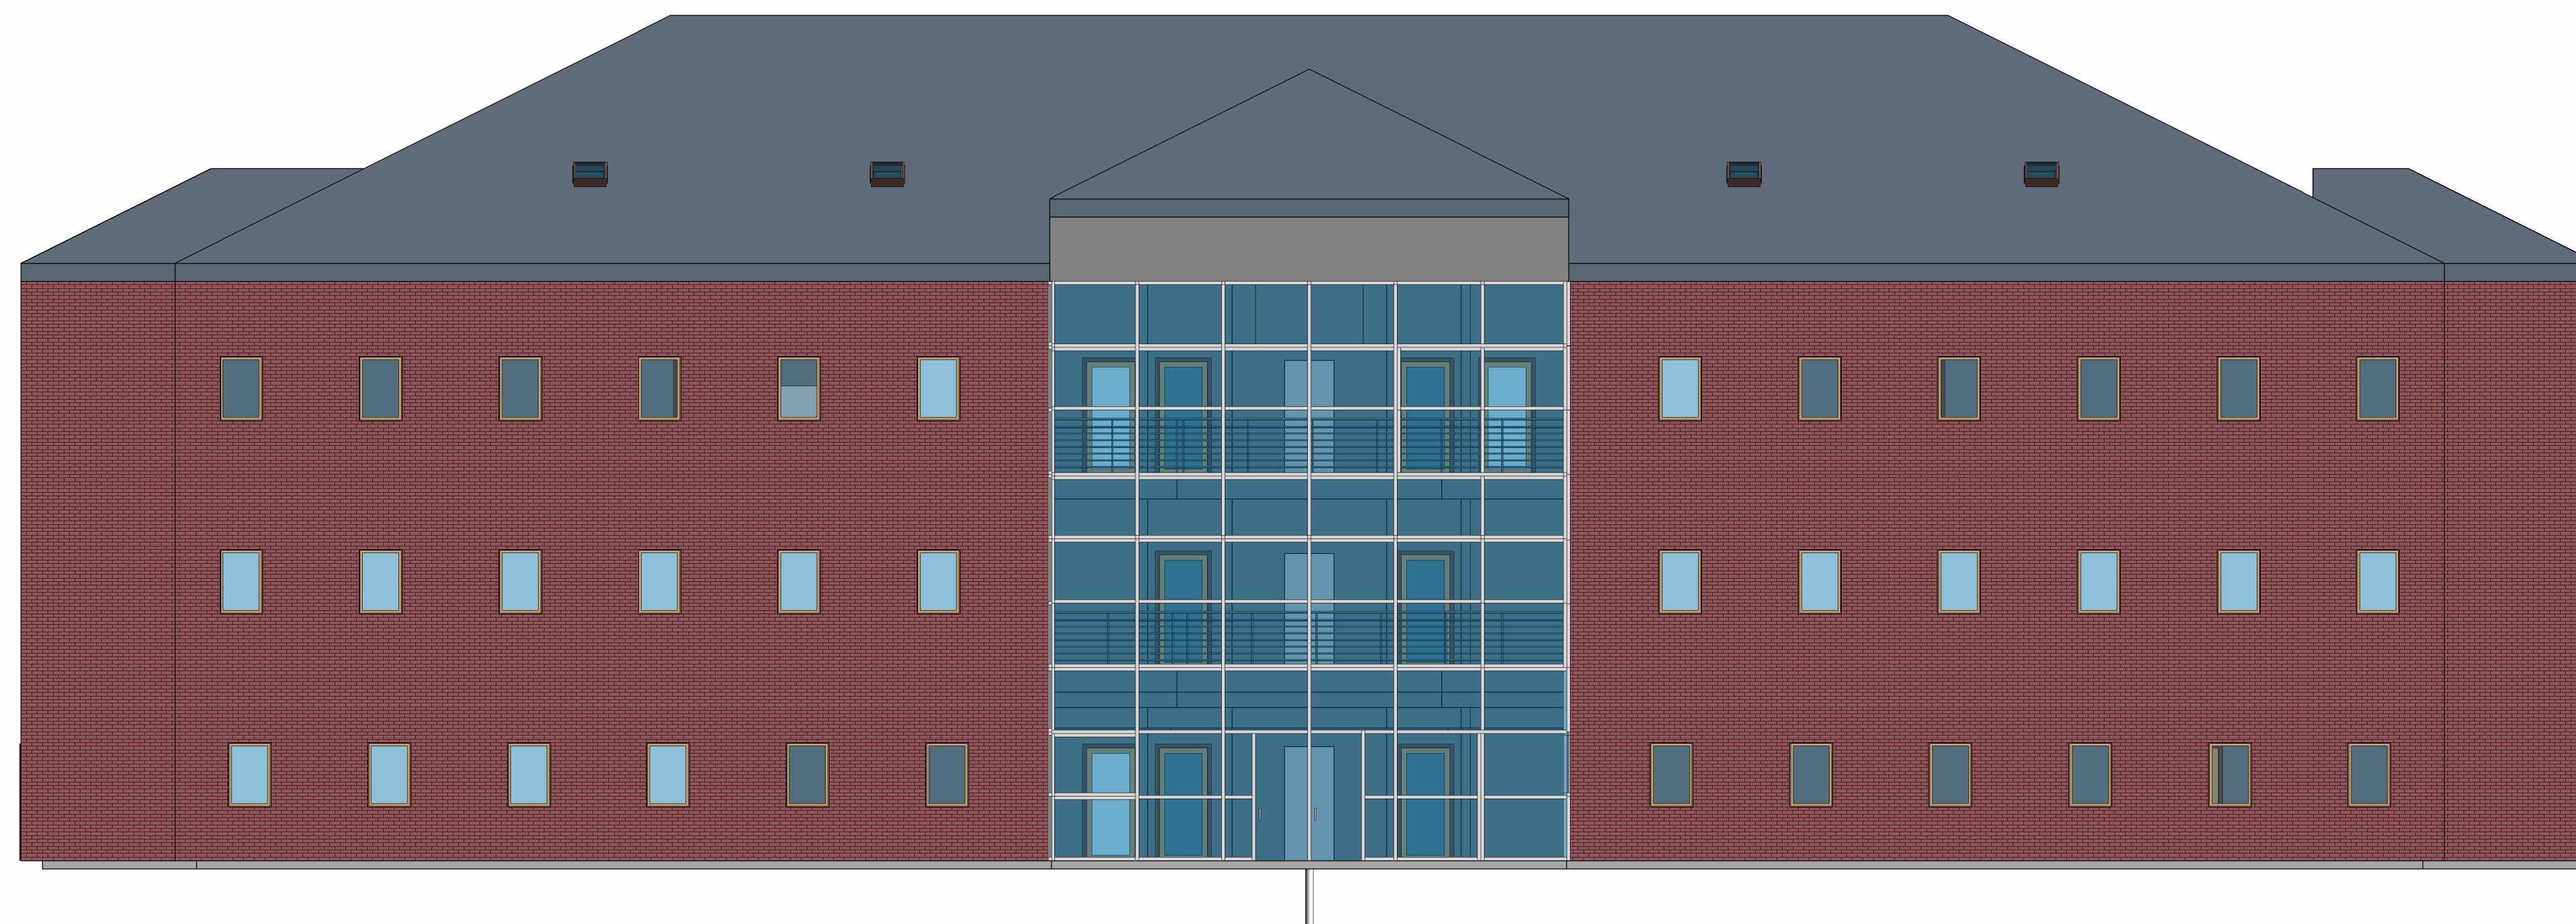

1 Atrium Roof Option 2

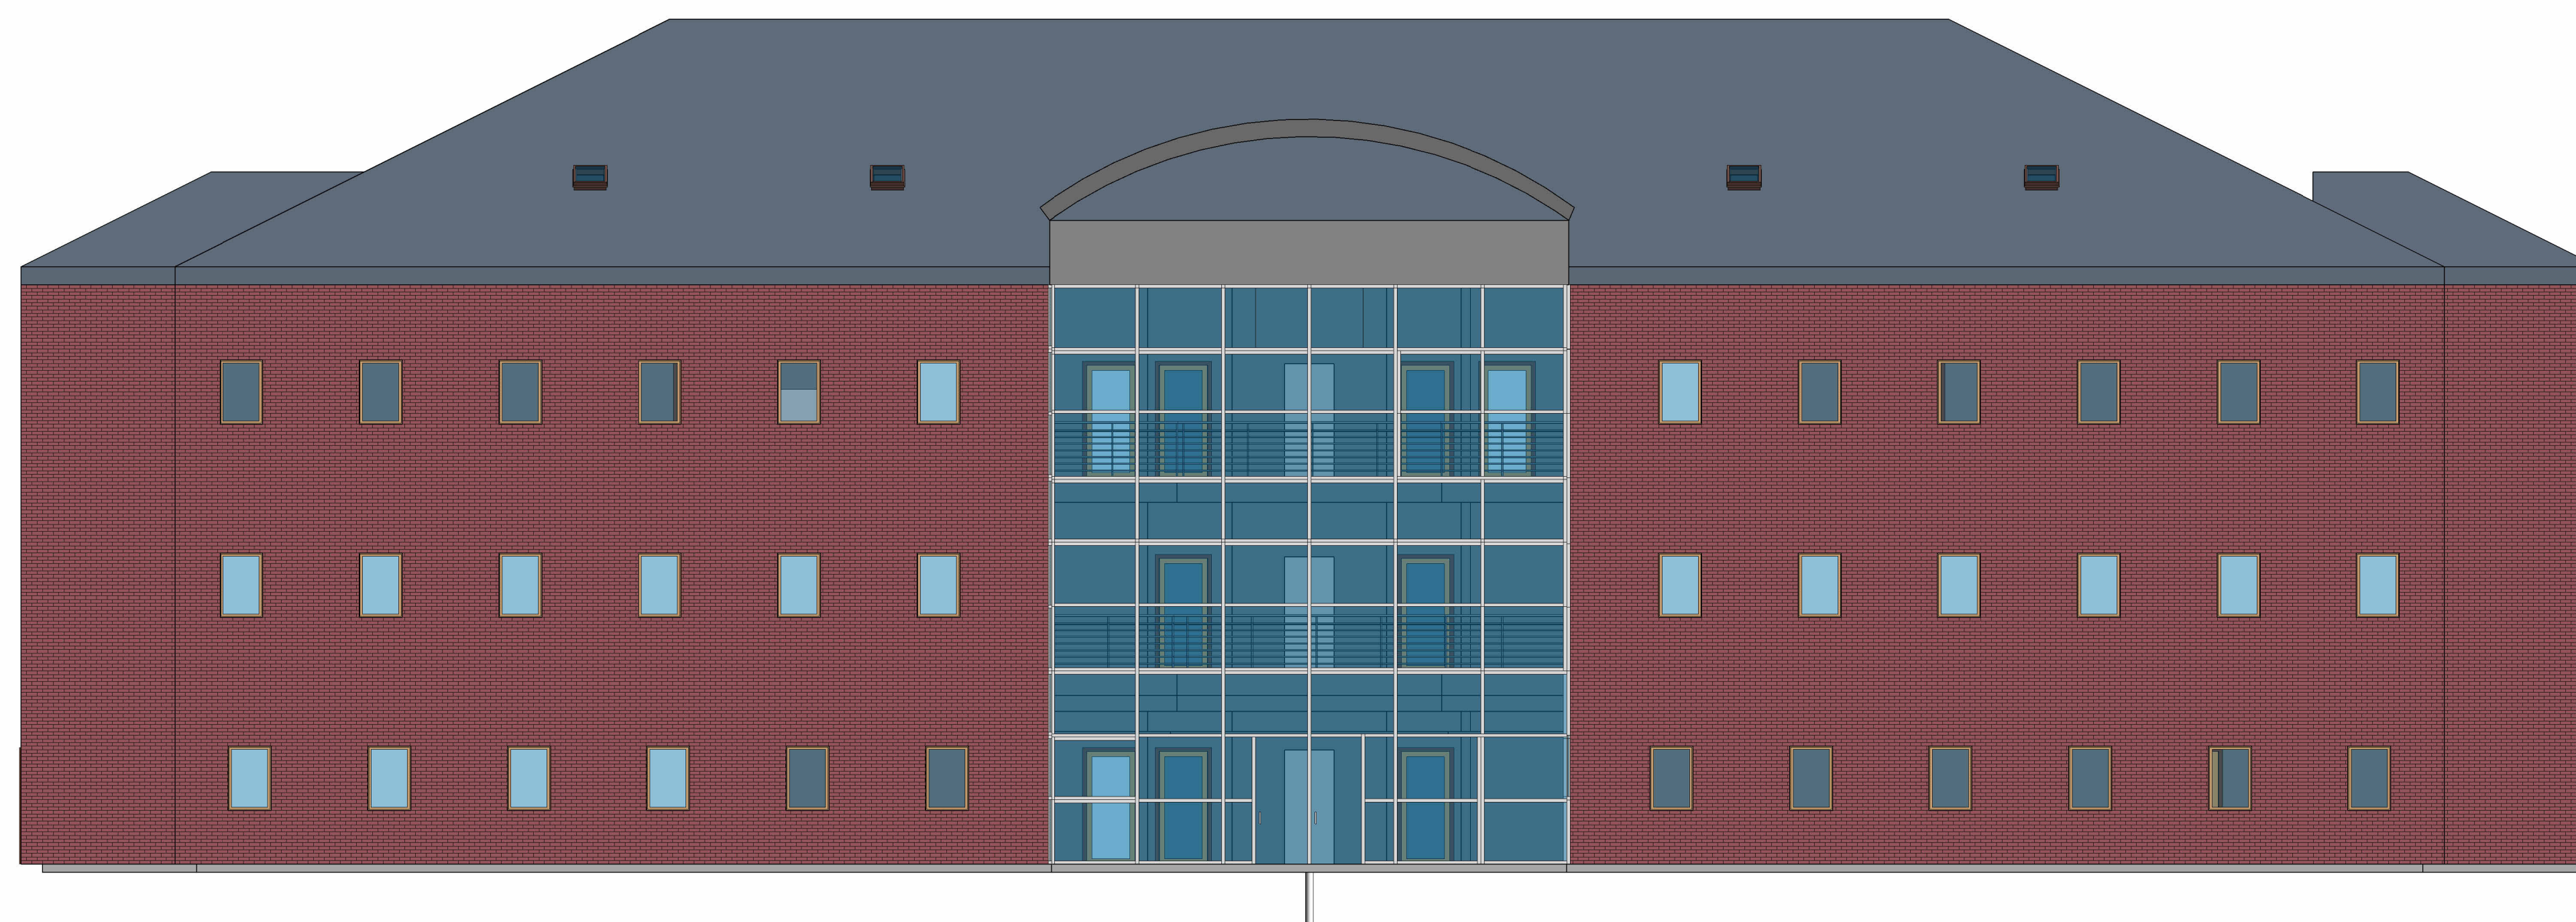

2 Curtainwall Option 2

[illegible]

T.H.E Developers

Harbor View Offices

Design Options

Project Number	2026-001
----------------	----------

Date	June 3, 2026
------	--------------

Drawn By	Author
----------	--------

A900

	Scale
--	-------