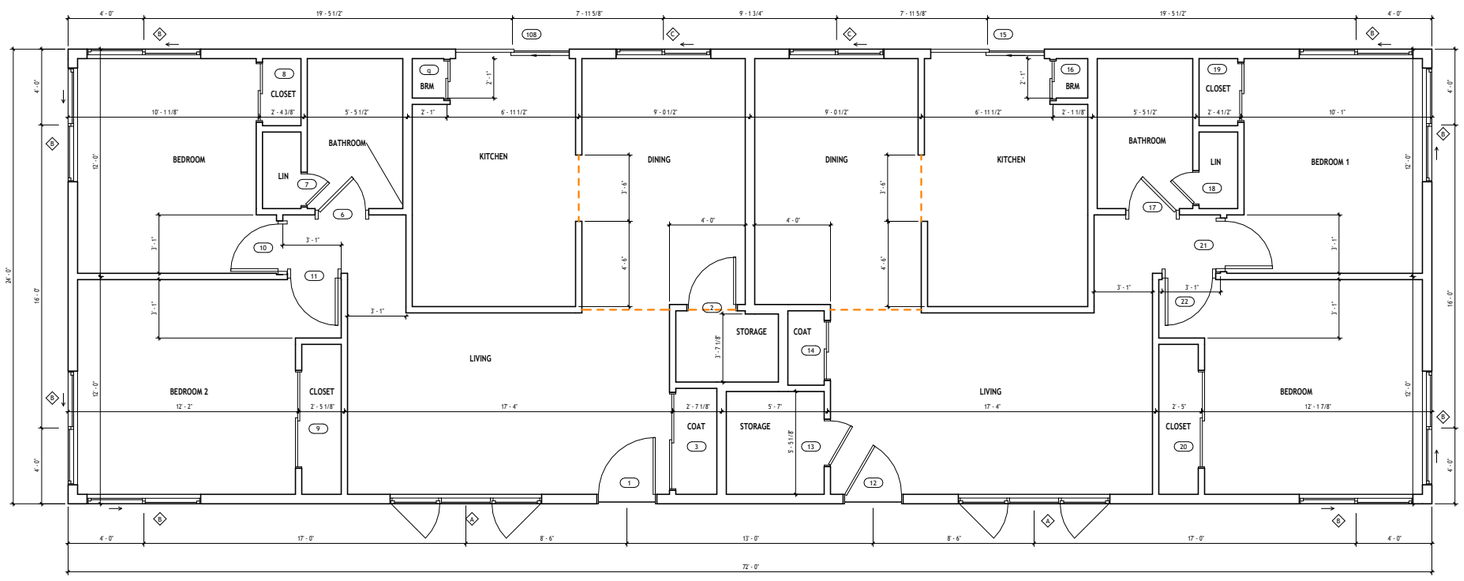

1 FLOOR PLAN
3/8" = 1'-0"

N

AUTODESK

www.autodesk.com/revit

Consultant
Address
Address
Address
Phone

Consultant
Address
Address
Address
Phone

Consultant
Address
Address
Address
Phone

Consultant
Address
Address
Address
Phone

Consultant
Address
Address
Address
Phone

No.	Description	Date

TULSA COMMUNITY COLLEGE 2-UNIT PHASE-5

SITE FLOR PLAN

Project Number	Project Number
Date	Issue Date
Drawn By	ADEL KNODE
Checked By	BRADFORD

A101

Scale	3/8" = 1'-0"

4/26/2026 2:44:32 PM

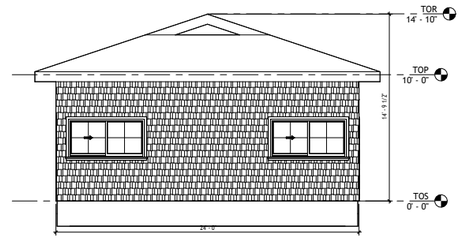

4 EAST ELEVATION
1/4" = 1'-0"

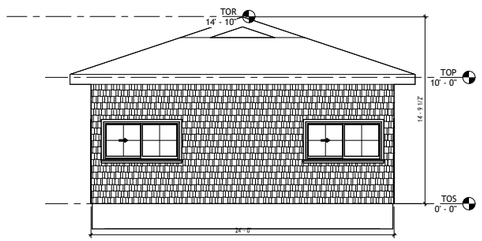

2 WEST ELEVATION
1/4" = 1'-0"

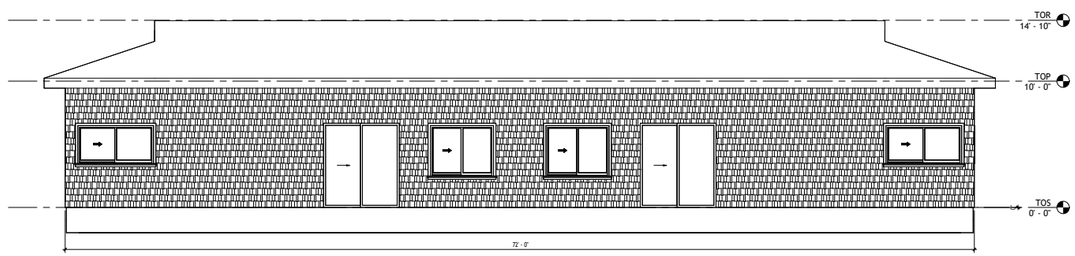

3 SOUTH ELEVATION
1/4" = 1'-0"

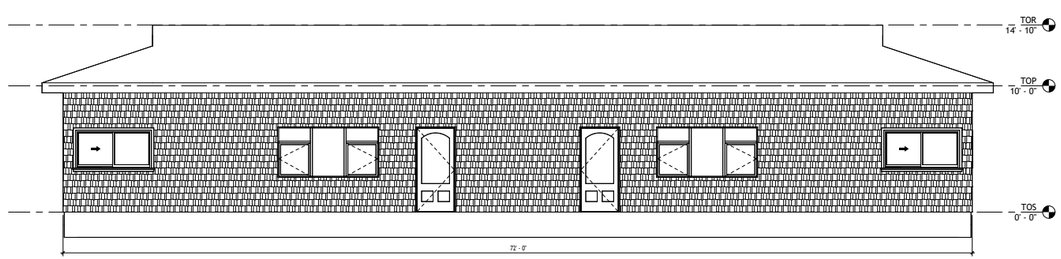

1 NORTH ELEVATION
1/4" = 1'-0"

AUTODESK

www.autodesk.com/revit

Consultant
Address
Address
Address
Phone

Consultant
Address
Address
Address
Phone

Consultant
Address
Address
Address
Phone

Consultant
Address
Address
Address
Phone

Consultant
Address
Address
Address
Phone

No.	Description	Date

TULSA COMMUNITY COLLEGE 2-UNIT PHASE-5

BUILDING ELEVATIONS

Project Number	Project Number
Date	Issue Date
Drawn By	ADEL KNODE
Checked By	BRADFORD

A201

Scale 1/4" = 1'-0"

4/26/2026 2:44:33 PM

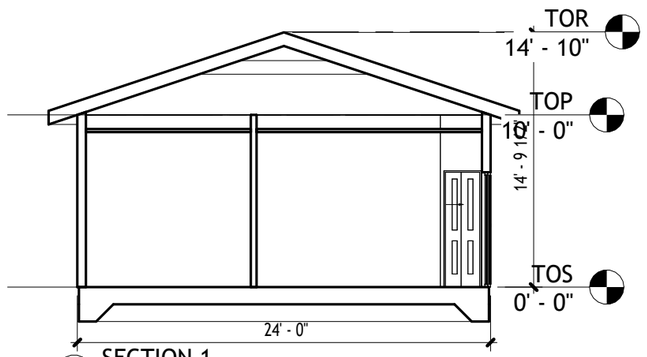

3 SECTION 1
1/8" = 1'-0"

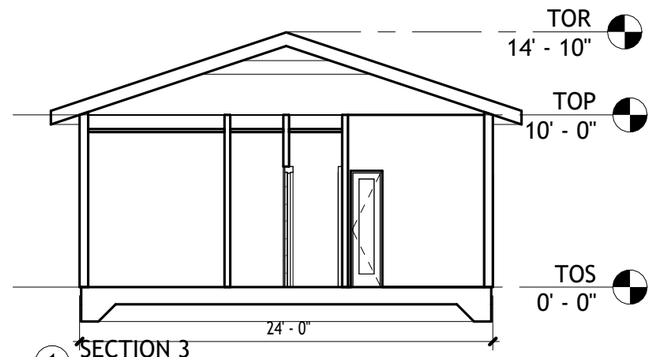

1 SECTION 3
1/8" = 1'-0"

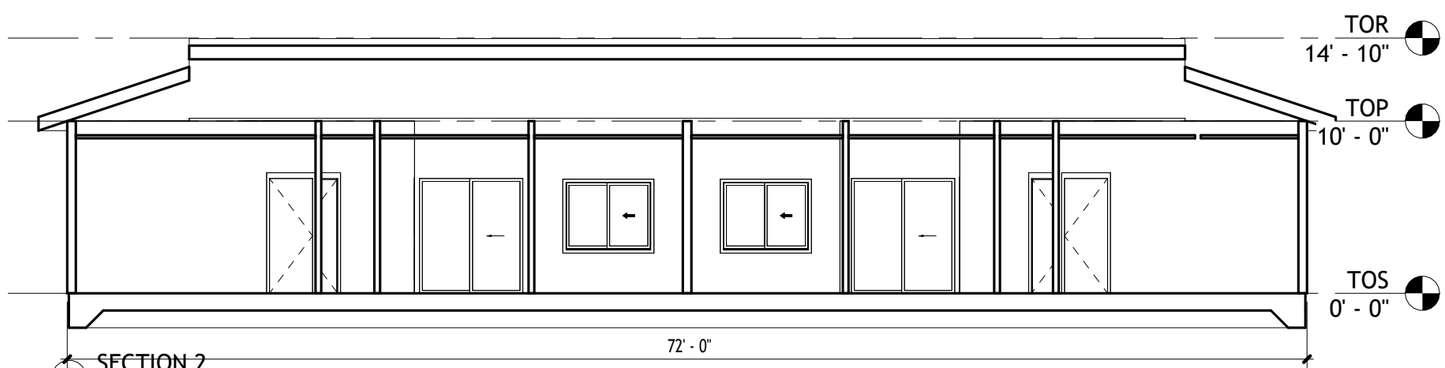

2 SECTION 2
1/8" = 1'-0"

AUTODESK

www.autodesk.com/revit

TULSA COMMUNITY COLLEGE
2-UNIT PHASE-5

No.	Description	Date

BUILDING SECTIONS

Project number	Project Number	A301
Date	Issue Date	
Drawn by	ADEL KNODE	
Checked by	BRADFORD	Scale 1/8" = 1'-0"

4/26/2026 2:44:33 PM

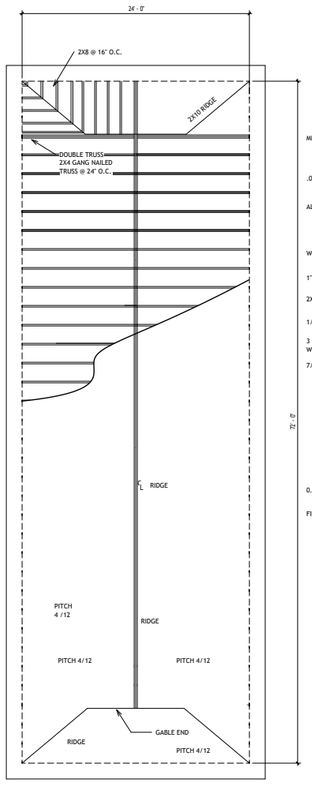

1 ROOF FRAMING PLAN
3/16" = 1'-0"

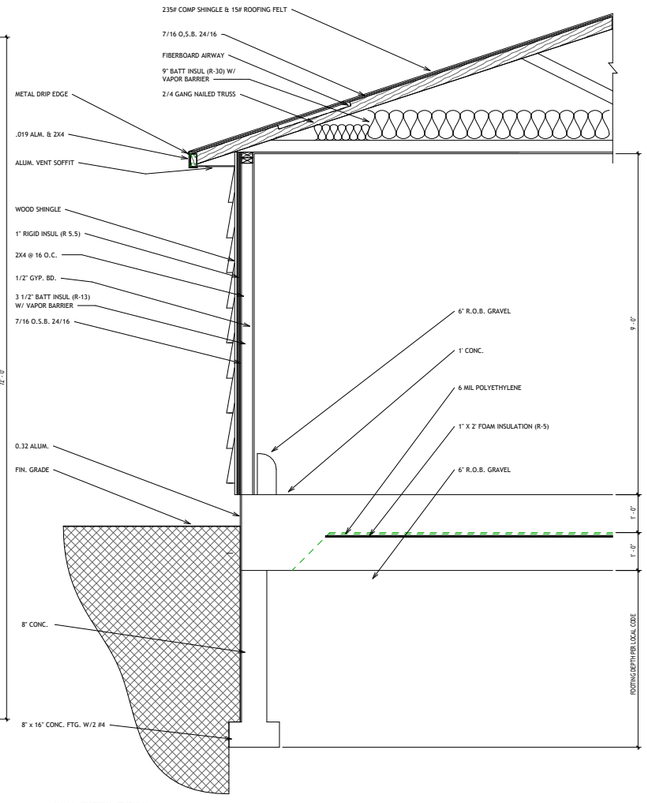

2 WALL SECTION (TYPICAL)
3/4" = 1'-0"

WEST SIDE DOOR SCHEDULE: (ALL UNITS PREHUNG / PREFIT W/HARDWARE)							
TAG	LOCATION	SIZE (INCHES)	THICKNESS	MATERIAL	FRAME MATERIAL	TYPE	COMMENTS
12	LIVING	36 X 80	1- 3/8	OAK	OAK	A	
13	STORAGE	30 X 80	1- 3/8	OAK	OAK	B	
14	COAT	36 X 80	1- 3/8	OAK	OAK	D	SLIDING
15	KITCHEN	72 X 80	2	GLASS	OAK	E	
16	BROOM	24 X 80	1- 3/8	OAK	OAK	D	SLIDING
17	BATHROOM	30 X 80	1- 3/8	OAK	OAK	B	
18	LINEN	20 X 80	1- 3/8	OAK	OAK	C	
19	BEDROOM 1 CLOS	36 X 80	1- 3/8	OAK	OAK	D	SLIDING
20	BEDROOM 2 CLOS	60 X 80	1- 3/8	OAK	OAK	D	SLIDING
21	BEDROOM 1	30 X 80	1- 3/8	OAK	OAK	B	
22	BEDROOM 2	30 X 80	1- 3/8	OAK	OAK	B	

3 DOOR SCHEDULE EAST
3/4" = 1'-0"

WEST SIDE DOOR SCHEDULE: (ALL UNITS PREHUNG / PREFIT W/HARDWARE)							
TAG	LOCATION	SIZE (INCHES)	THICKNESS	MATERIAL	FRAME MATERIAL	TYPE	COMMENTS
1	LIVING	36 X 80	1- 3/8	OAK	OAK	A	
2	STORAGE	30 X 80	1- 3/8	OAK	OAK	B	
3	COAT	60 X 80	1- 3/8	OAK	OAK	D	SLIDING
4	KITCHEN	72 X 80	2	GLASS	OAK	E	
5	BROOM	24 X 80	1- 3/8	OAK	OAK	D	SLIDING
6	BATHROOM	30 X 80	1- 3/8	OAK	OAK	B	
7	LINEN	20 X 80	1- 3/8	OAK	OAK	C	
8	BEDROOM 1 CLOS	36 X 80	1- 3/8	OAK	OAK	D	SLIDING
9	BEDROOM 2 CLOS	60 X 80	1- 3/8	OAK	OAK	D	SLIDING
10	BEDROOM 1	30 X 80	1- 3/8	OAK	OAK	B	
11	BEDROOM 2	30 X 80	1- 3/8	OAK	OAK	B	

4 DOOR SCHEDULE WEST
3/4" = 1'-0"

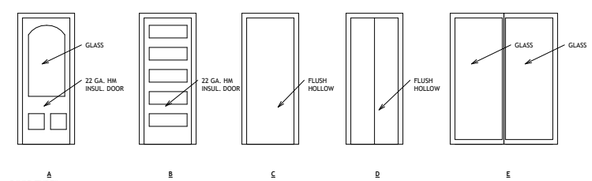

8 DOOR TYPES
3/8" = 1'-0"

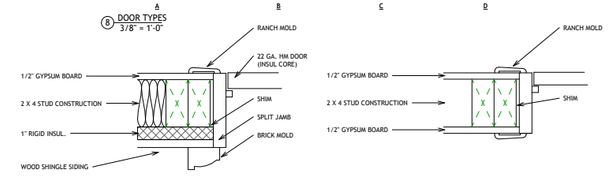

9 FRAME TYPES
3" = 1'-0"

WINDOW SCHEDULE				
TAG	SIZE	TYPE	GLASS	COMMENTS
A	8' X 6'	CASEMENT	1" INSUL	
B	6' X 3'	SLIDING	1" INSUL	
C	5' X 4'	SLIDING	1" INSUL	

5 WINDOW SCHEDULE
3/4" = 1'-0"

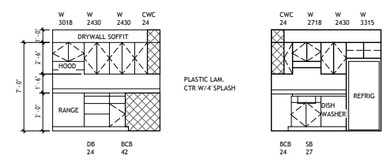

6 KITCHEN ELEVATIONS
1/4" = 1'-0"

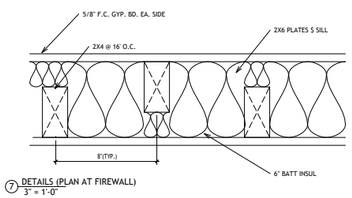

7 DETAILS (PLAN AT FIREWALL)
3" = 1'-0"

AUTODESK

www.autodesk.com/revit

Consultant
Address
Address
Address
Phone

Consultant
Address
Address
Address
Phone

Consultant
Address
Address
Address
Phone

Consultant
Address
Address
Address
Phone

Consultant
Address
Address
Address
Phone

No.	Description	Date

TULSA COMMUNITY COLLEGE
2-UNIT PHASE-5

DETAILS

Project Number	Project Number
Date	Issue Date
Drawn By	ADEL KNODE
Checked By	BRADFORD

A501

Scale	As indicated

4/26/2026 2:44:34 PM